
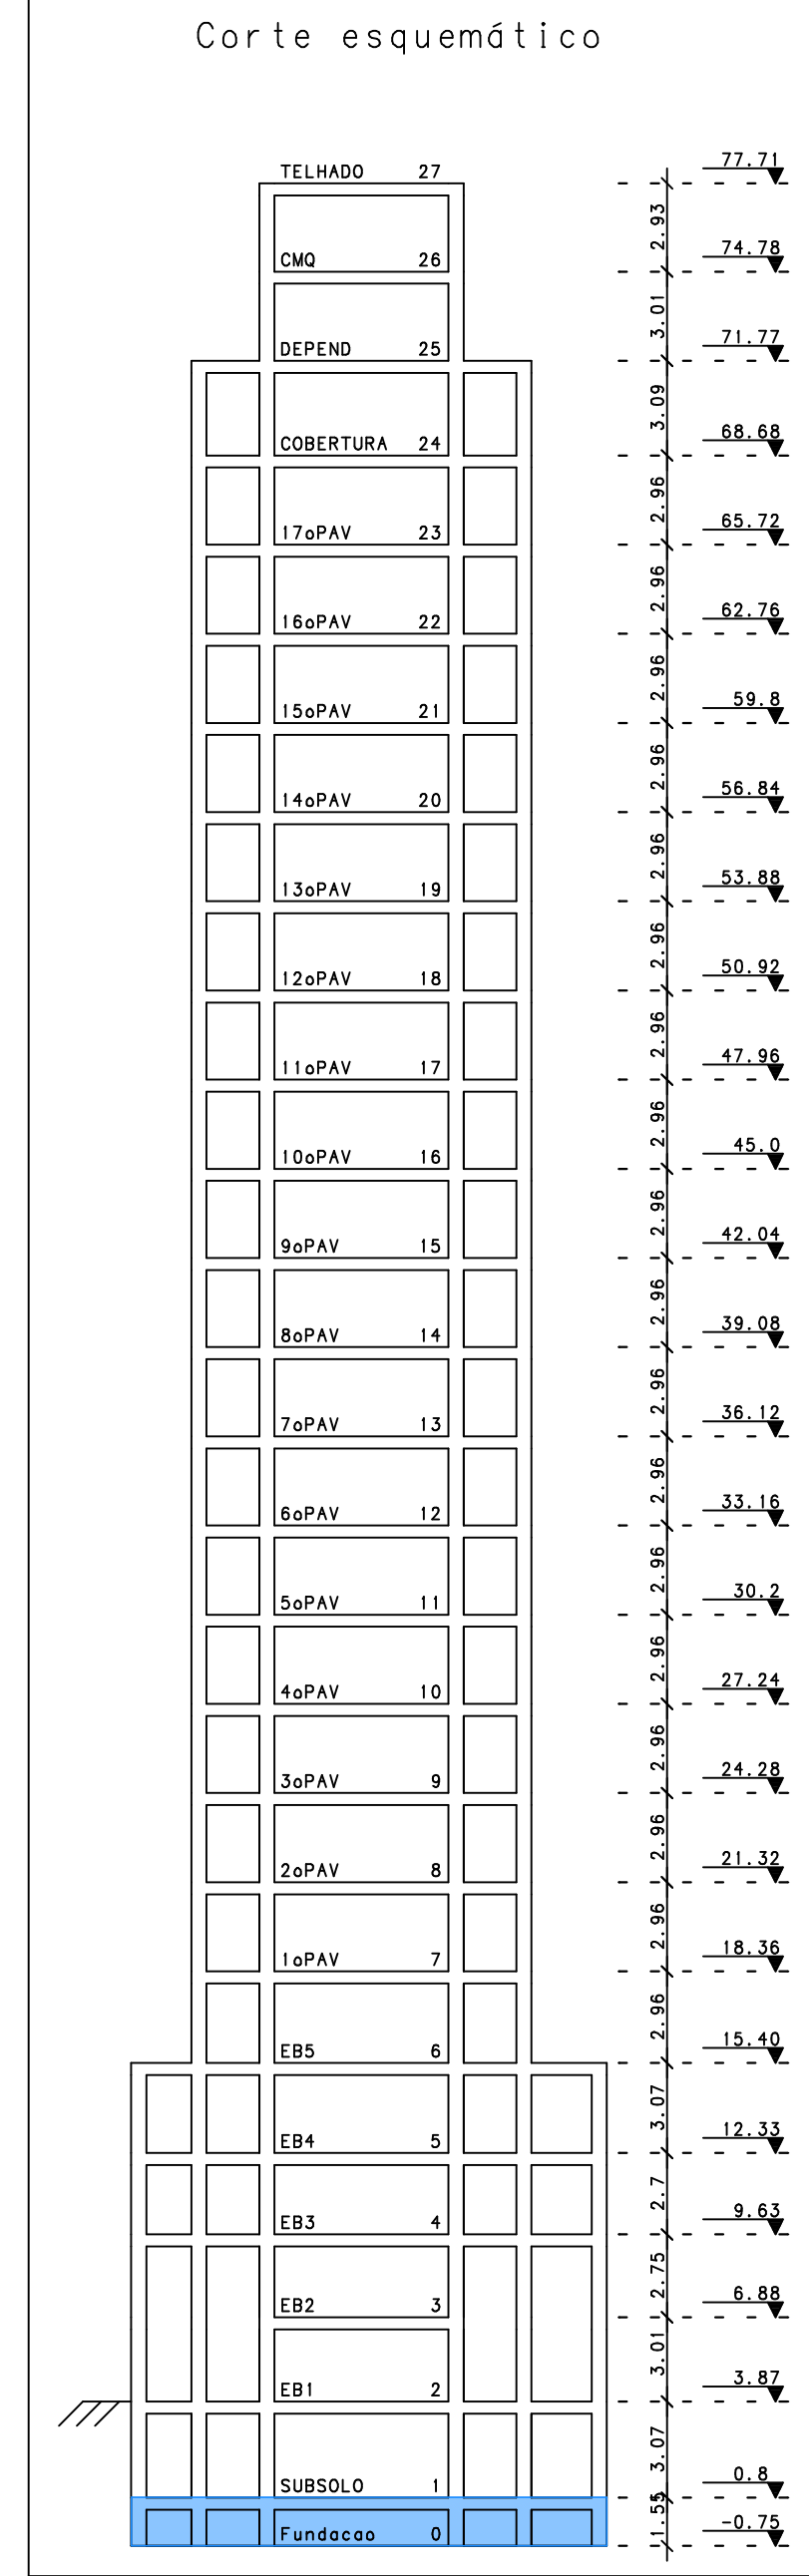
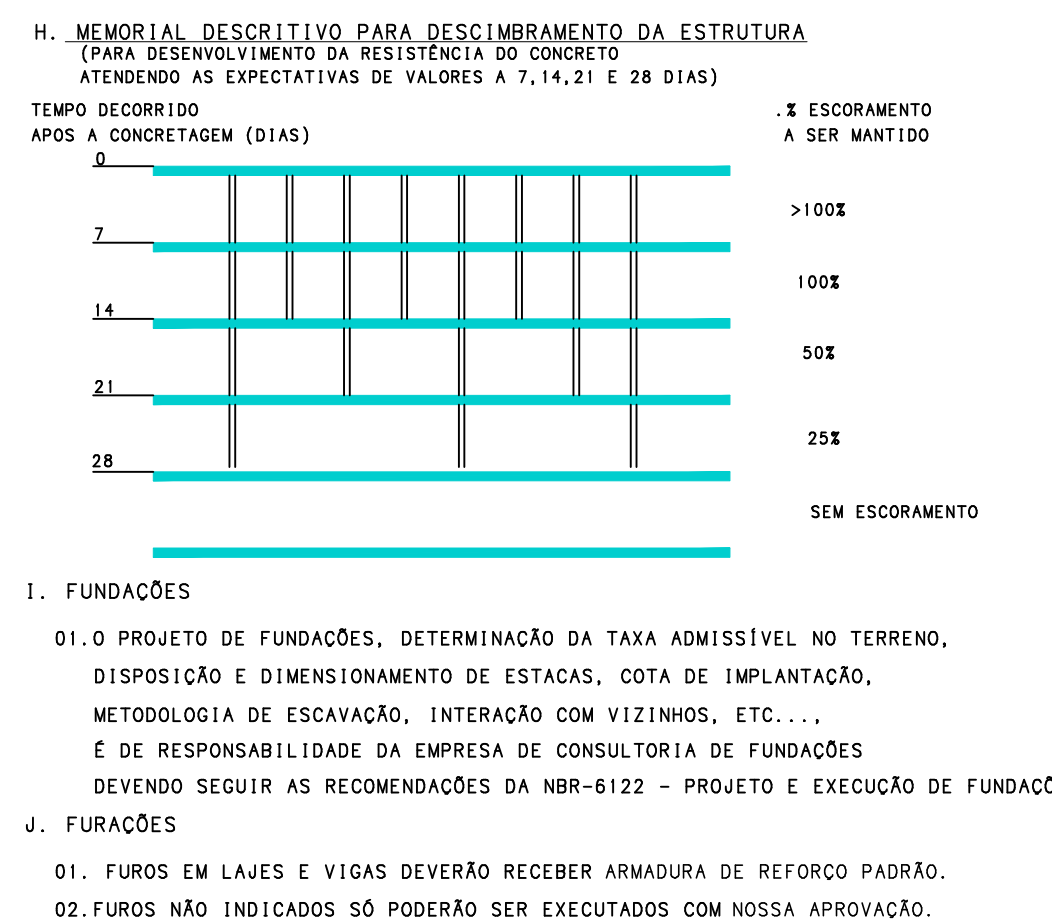


[illegible]

CONVENÇÃO DE PILARES

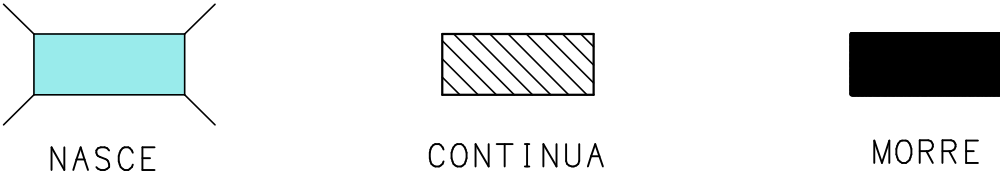


NOTAS GERAIS

- 1- DIMENSÕES EM CENTÍMETRO, NÍVEIS EM METRO
- 2- PROPRIEDADES DO CONCRETO:
- $f_{ck} > 40 \text{ MPa}$ (400 kg/cm^2)
- MÓDULO DE DEFORMAÇÃO TANGENTE INICIAL $> 26 \text{ GPa}$
- CONSUMO MÍNIMO DE CIMENTO: 320 kg/m^3
- FATOR ÁGUA/CEMENTO MÁXIMO: 0,55
- 3- UTILIZAR OBRIGATORIAMENTE EM CONJUNTO COM O DESENHO DE FURAÇÃO

ATENÇÃO/PLOTAGEM

OS ARQUIVOS DXF SERVEM APENAS COMO BASE PARA A ARQUITETURA E DEMAIS COMPLEMENTOS. O PLANTAR APENAS O ARQUIVO PDF - **COLORIDO** CASO CONTRÁRIO PODERA HAVER PERDA DE INFORMAÇÕES.

10		
09		
08		
07		
06	22/05/2026	AJUSTADO POSIÇÃO DA GRUA E VIGAS
05	06/01/2025	EMISSION INICIAL
REV.	DATA	DESCRIÇÃO

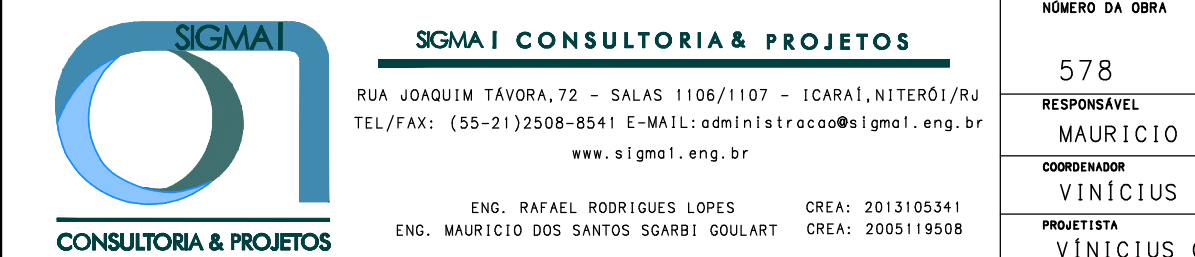

		OSCEDE № ST 0
---	---	---------------

EMPENHAMENTO E LOCAL	PROJETO
PDM 1050	ESTRUTUR
RUA PRUDENTE DE MORAIS, 1050 - IPANEMA, RIO DE JANEIRO - RJ	TAB
	EXECUTIV
TÍTULO DO DESERVO	ESCALA
FORMA	1:50
PISO DO SUBSOLO	DATA
(TETO DO SUBSOLO)	22/05/2026
	ARQUIVO

DIMENSÃO DA FOLHA: 1374x841mm (A0)