

corte A-A

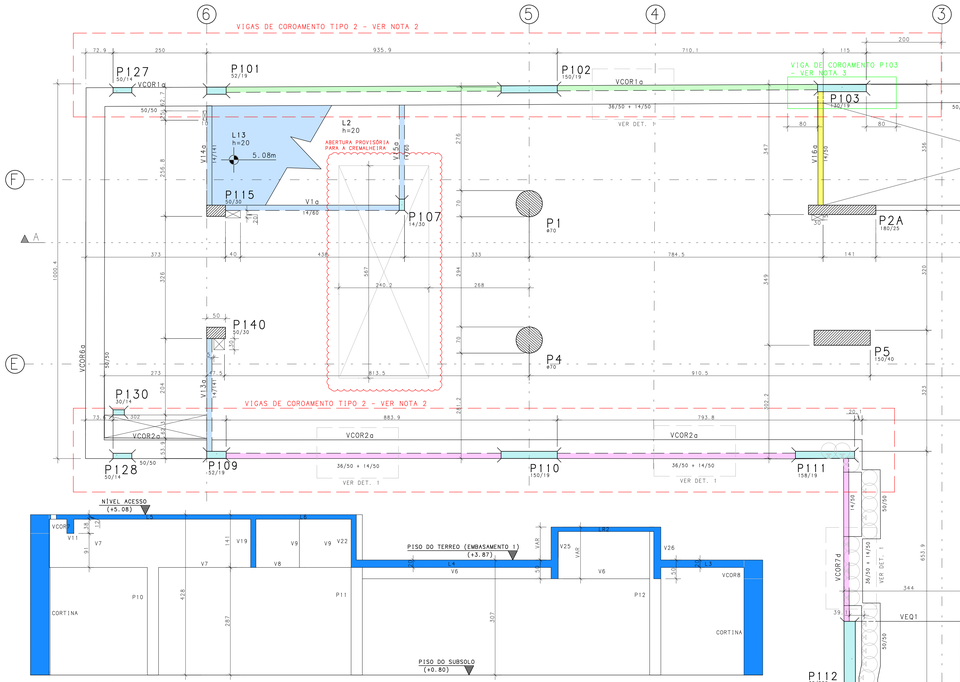


corte B-B

Corte esquemático

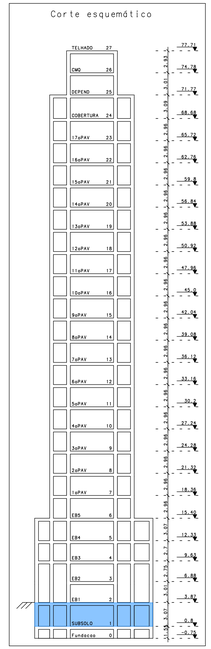


FORMA AUXILIAR 1

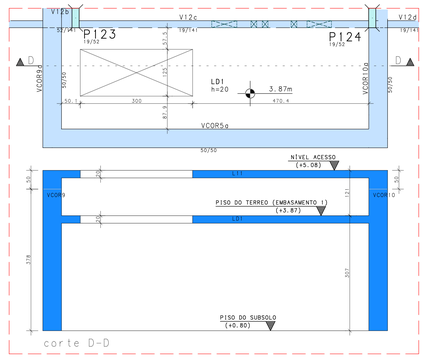

corte D-D

Lajes							
Elemento	Tipo	Altura cm	Elevação cm	PP tf/m	PERM tf/m	ACID tf/m	TOT tf/m
L1	Maciça	12		0.300	0.155	0.300	0.755
L2	Maciça	20		0.500	0.100	0.300	0.900
L3	Maciça	20		0.500	0.100	0.300	0.900
L4	Maciça	20		0.500	0.100	0.300	0.900
L5	Maciça	12	121	0.300	0.155	0.300	0.755
L6	Maciça	12	121	0.300	0.155	0.300	0.755
L7	Maciça	12	121	0.300	0.155	0.300	0.755
L8	Maciça	12	121	0.300	0.155	0.300	0.755
L9	Maciça	12	121	0.300	0.155	0.300	0.755
L10	Maciça	12	121	0.300	0.155	0.300	0.755
L11	Maciça	20		0.500	0.200	0.300	0.900
L12	Maciça	20		0.500	0.100	0.300	0.900
L13	Maciça	20	121	0.500	0.100	0.300	0.900
L14	Maciça	12	121	0.300	0.155	0.300	0.755
L15	Maciça	12	121	0.300	0.155	0.300	0.755
LR1	Maciça	15		0.375	0.100	0.300	0.775
LR2	Maciça	12		0.300	0.155	0.300	0.755

DETALHE 1: VIGAS DE COROAMENTO

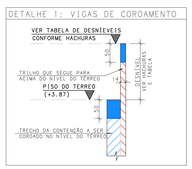


NOTA 1: O PILAR P8 DEVE SER CONCRETADO COM FCK DE 45 MPa ATÉ O NÍVEL +21.32 (PISO DO 2º PAVIMENTO)

NOTA 2: AS VIGAS DE COROAMENTO ESTÃO DIVIDIDAS EM TIPOS 1 E 2. AS VIGAS DE COROAMENTO ENVOLTAS EM UM RETÂNGULO VERMELHO TRACEJADO SÃO AS TIPO 2, QUE RECEBEM AS ESTRONCAS METÁLICAS. PARA ESTAS VIGAS, EXISTE UMA DIFERENCIAÇÃO DE ARMAÇÕES, DETALHADA NO PROJETO DE ARMADURAS. OS DEMAIS TRECHOS DE VIGAS DE COROAMENTO, SEM NENHUMA INDICAÇÃO, SÃO VIGAS DO TIPO 1.

NOTA 3: O TRECHO DA VIGA DE COROAMENTO QUE APOIA O P103, DEMARCADO POR UM RETÂNGULO VERDE, DEVERÁ SER ARMADO COM UM REFORÇO ESPECIFICIO INDICADO NO PROJETO DE ARMAÇÕES ALÉM DA ARMADURA GENÉRICA DETALHADA PARA TODA A EXTENSÃO DAS VIGAS DE COROAMENTO.

DETALHE 2

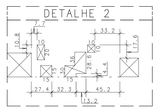


LEGENDA

RAMPAS

ENCHIMENTO

Legenda de desníveis	
Cor	Desnível cm
	30
	121
	150
	180
	190

corte C-C

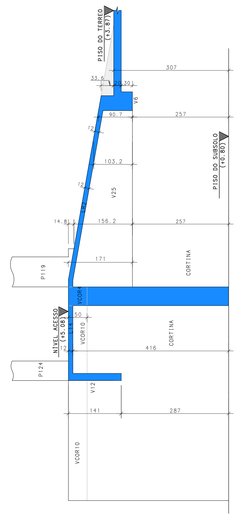

NOTAS GERAIS PARA O USO DESTE PROJETO :

A. DIREITOS AUTORAIS

ESTE PROJETO É PROPRIEDADE DE **SIGMA! CONSULTORIA & PROJETOS** FILIADO A ASSOCIAÇÃO BRASILEIRA DE ENGENHARIA E CONSULTORIA ESTRUTURAL - ABECE, SOB O Nº 01281, NÃO SENDO PERMITIDA SUA UTILIZAÇÃO PARA QUALQUER FINALIDADE QUE NÃO A ESPECIFICAMENTE DESTINADA À EXECUÇÃO DESTA OBRA, SENDO TERMINANTEMENTE VEDADA SUA COLOCAÇÃO À DISPOSIÇÃO DE TERCEIROS.

B. NORMAS TÉCNICAS DE REFERÊNCIA

NBR 6118	PROJETO DE ESTRUTURAS DE CONCRETO
NBR 6120	CARGAS PARA O CÁLCULO DE ESTRUTURAS DE EDIFICAÇÕES
NBR 6123	FORÇAS DEVIDAS AO VENTO EM EDIFICAÇÕES
NBR 5671	PARTICIPAÇÃO DOS INTERVENIENTES EM SERVIÇOS E OBRAS DE ENGENHARIA E ARQUITETURA
NBR 12654	CONTROLE TECNOLÓGICO DE MATERIAIS COMPONENTES DO CONCRETO
NBR 12655	CONCRETO - PREPARO, CONTROLE E RECEBIMENTO
NBR 5738	MOLDAGEM E CURA DE CORPOS DE PROVA CILÍNDRICOS OU PRISMÁTICOS DE CONCRETO - PROCEDIMENTO
NBR 5739	CONCRETO - ENSAIO DE COMPRESSÃO DE CORPOS-DE-PROVA CILÍNDRICOS - MÉTODO DE ENSAIO
NBR 8522	CONCRETO - DETERMINAÇÃO DO MÓDULO DE DEFORMAÇÃO ESTÁTICA E DIAGRAMA TENSÃO x DEFORMAÇÃO - MÉTODO DE ENSAIO
NBR 6152	MATERIAIS METÁLICOS - DETERMINAÇÃO DAS PROPRIEDADES MECÁNICAS A TRAÇÃO - MÉTODO DE ENSAIO
NBR 6153	PRODUTO METÁLICO - ENSAIO DE DOBRAMENTO SEMI-GUIADO
NBR 7477	DETERMINAÇÃO DO COEFICIENTE DE CONFORMAÇÃO SUPERFICIAL DE BARRAS E FIOS DE AÇO DESTINADOS A ARMADURAS DE CONCRETO ARMADO - MÉTODO DE ENSAIO
NBR 7480	BARRAS E FIOS DE AÇO DESTINADOS A ARMADURAS PARA CONCRETO ARMADO - ESPECIFICAÇÃO

C. GEOMETRIA

OS ELEMENTOS DE CONFORMABILIDADE DO PROJETO ESTRUTURAL FACE AOS PROJETOS DE ARQUITETURA, INSTALAÇÕES E DEMAIS DISCIPLINAS,TAIS COMO COTAS, NÍVEIS, DIMENSÕES DAS PEÇAS ESTRUTURAIS, POÇOS DE ELEVADORES, ESCADAS, ETC. DEVEM SER VALIDADOS PELOS ARQUITETOS RESPONSÁVEIS PELO DESENVOLVIMENTO DO PROJETO EXECUTIVO.

D. MATERIAIS

01. CONCRETO
VER EM NOTAS GERAIS
02.AÇO EM ARMADURA PASSIVA
02.1. AÇO CA-50A / CA-60B
03. FORMAS E ESCORAMENTOS
03.1.O PROJETO E DIMENSIONAMENTO DAS FORMAS E ESCORAMENTOS NÃO FAZ PARTE DO ESCOPO DE NOSSOS SERVIÇOS.

E. EXECUÇÃO DA ESTRUTURA.

A EXECUÇÃO DA ESTRUTURA É DE RESPONSABILIDADE DA EMPRESA CONSTRUTORA E DEVERÁ CONTAR COM A CONSULTORIA DE UM TECNOLOGISTA DE MATERIAIS O ENGENHEIRO RESPONSÁVEL PELA EXECUÇÃO DEVERÁ OBSOCEER AS RECOMENDAÇÕES DA NBR 14931-EXECUÇÃO DE ESTRUTURAS DE CONCRETO-PROCEDIMENTOS

F. CARGAS ADOTADAS PARA ESTE PROJETO
01. CARGAS ACIDENTAIS CONFORME NBR 6123
02. CARGAS ACIDENTAIS NÃO PARTICULARES CONFORME NBR 6120 DE ACORDO COM PROJETO ARQUITETONICO APROVADA EM PREFEITURA
03. PESO PRÓPRIO DO CONCRETO : 2500 kgf / m3
04. ALVENARIAS (COM REVESTIMENTOS) :1300 kgf / m3
+ ESPESSURA DA ALVENARIA ACABADA CONFORME PROJ. ARQUITETÔNICO
05. LAJES (CONTRAPISO + REVESTIMENTOS) :100 kgf / m2
OBS : AS CARGAS EVENTUAIS INFORMADAS NAS PRANCHAS DE FORMAS PREVALECEM SOBRE AS CARGAS AQUI INDICADAS.

G.CORRIMENTOS.

	PAV. REVESTIDOS	
	COBERTOS	DEMAIS PAV.
01. LAJES: POSITIVA/NEGATIVA	2,0/1,5 cm	2,0/2,0 cm
02. VIGAS:	2,5 cm	2,5 cm
03. PILARES:	3,0 cm	3,0 cm
04. BLOCOS SOBRE ESTACAS / SAPATAS:	3,0 cm	
05. CINTAS / LAJES DE SUBPRESSÃO:	2,0 cm	
06. PAREDES DE SUBSOLO:	3,0 cm	
07. RESERVATÓRIOS:	3,0 cm	

OBS: 1) DEVERÁ HAVER CONTROLE RIGOROSO DE QUALIDADE E RÍGIDOS LIMITES DE TOLERÂNCIA DAS MEDIDAS DURANTE A EXECUÇÃO.
2) CORRIMENTOS INFORMADOS NOS DESENHOS DE ARMAÇÃO PREVALECEM EM RELAÇÃO À TABELA ACIMA.

H. MEMORIAL DESCRITIVO PARA DESCIMBRAMENTO DA ESTRUTURA
(PARA DESENVOLVIMENTO DA RESISTÊNCIA DO CONCRETO ATENDENDO AS EXPECTATIVAS DE VALORES A 7,14,21 E 28 DIAS)

TEMPO DECORRIDO APÓS A CONCRETAGEM (DIAS)	% ESCORAMENTO A SER MANTIDO
1	>100%
7	100%
14	50%
21	25%
28	SEM ESCORAMENTO

I. FUNDAÇÕES

01.O PROJETO DE FUNDAÇÕES, DETERMINAÇÃO DA TAXA ADMISSÍVEL NO TERRENO, DISPOSIÇÃO E DIMENSIONAMENTO DE ESTACAS, COTA DE IMPLANTAÇÃO, METODOLOGIA DE ESCAVAÇÃO, INTERAÇÃO COM VIZINHOS, ETC.... É DE RESPONSABILIDADE DA EMPRESA DE CONSULTORIA DE FUNDAÇÕES DEVENDO SEGUIR AS RECOMENDAÇÕES DA NBR-6122 - PROJETO E EXECUÇÃO DE FUNDAÇÕES

J. FURAÇÕES

01. FUROS EM LAJES E VIGAS DEVERÃO RECEBER ARMADURA DE REFORÇO PADRÃO.
02.FUROS NÃO INDICADOS SÓ PODERÃO SER EXECUTADOS COM NOSSA APROVAÇÃO.

CONVENÇÃO DE PILARES

NASCE | CONTINUA | MORRE

NOTAS GERAIS

1- DIMENSÕES EM CENTIMETRO, NÍVEIS EM METRO
2- PROPRIEDADES DO CONCRETO:
- Fck > 40 MPa (400 kg/cm²)
- MÓDULO DE DEFORMAÇÃO TANGENTE INICIAL > 26 GPa
- CONSUMO MÍNIMO DE CIMENTO: 320 kg/m³
- FATOR ÁGUA/CIMENTO MÁX(NO): 0.55
3- UTILIZAR OBRIGATORIAMENTE EM CONJUNTO COM O DESENHO DE FURAÇÃO

ATENÇÃO/PLOTAGEM

-OS ARQUIVOS DXF SERVEM APENAS COMO BASE PARA A ARQUITETURA E DEMAIS COMPLEMENTARES.
-PLOTAR APENAS O ARQUIVO PDF - **COLORIDO** CASO CONTRÁRIO PODERÁ HAVER PERDA DE INFORMAÇÕES

REV.	DATA	DESCRIÇÃO
11		
10		
09		
08		
07	22/05/2026	AJUSTADA POSIÇÃO DE ABERTURA DA GRUA
00	06/01/2025	CONFORME COMENTÁRIOS DA ARQUITETURA

SIGMA! CONSULTORIA & PROJETOS
RUA JOAQUIM TAVORA,72 - SALAS 1108/1107 - ICARAI,NITERÓI/RJ
TEL/FAX: (55-21)2508-8541 E-MAIL:sigma!estruturas@gmail.eng.br
www.sigma!.eng.br
ENG. RAFAEL RODRIGUES LOPES CREA: 2012105241
ENG. MAURICIO DOS SANTOS SOARES SOBLART CREA: 2005119508

NÚMERO DA OBRA: 578
RESPONSÁVEL: MAURICIO SOARES
DESENHISTA: VINICIUS CORDEIRO
PROJETISTA: VINICIUS CORDEIRO
DESENHO Nº: ST 003
EMPREENDIMENTO E LOCAL: PDM 1050 RUA PRUDENTE DE MORAIS, 1050 - IPANEMA, RIO DE JANEIRO - RJ
PROJETO: ESTRUTURA
FASE: EXECUTIVO
TÍTULO DO DESENHO: FORMA PISO DO TÉRREO (EMBASAMENTO 1) (TETO DO SUBSOLO)
ESCALA: 1:50
DATA: 22/05/2026
ARQUIVO: PDM-EST-EX-003-PR-DB1-FORMA.DWG

DIMENSÃO DA FOLHA: 1374x841mm (A0M)

SIGMA! CONSULTORIA & PROJETOS PDM-EST-EX-003-PR-DB1-FORMA.DWG 22/05/2026 17:25:18