
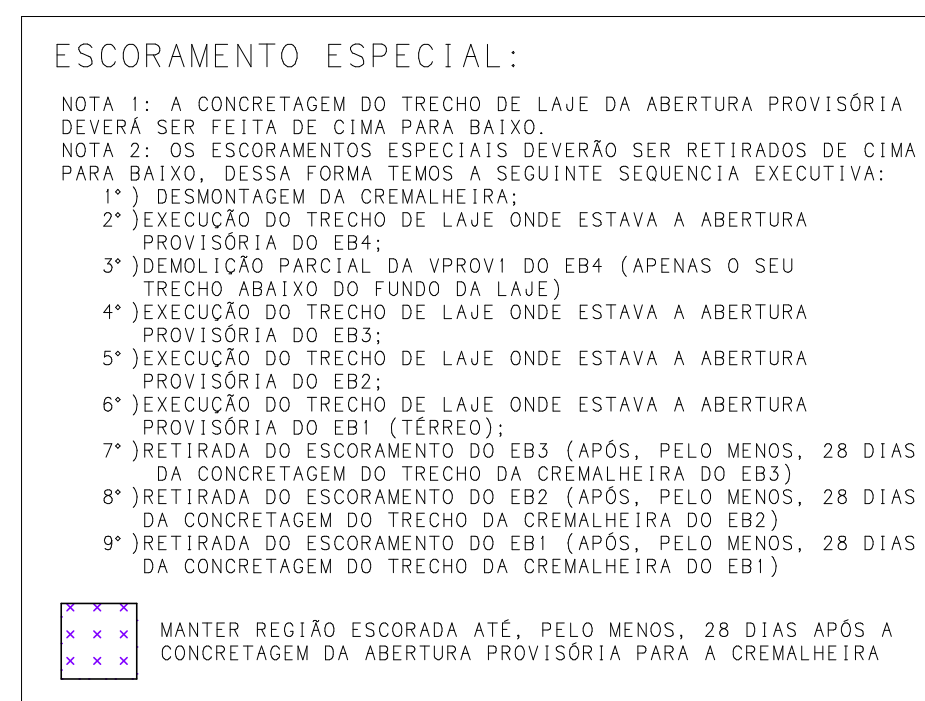




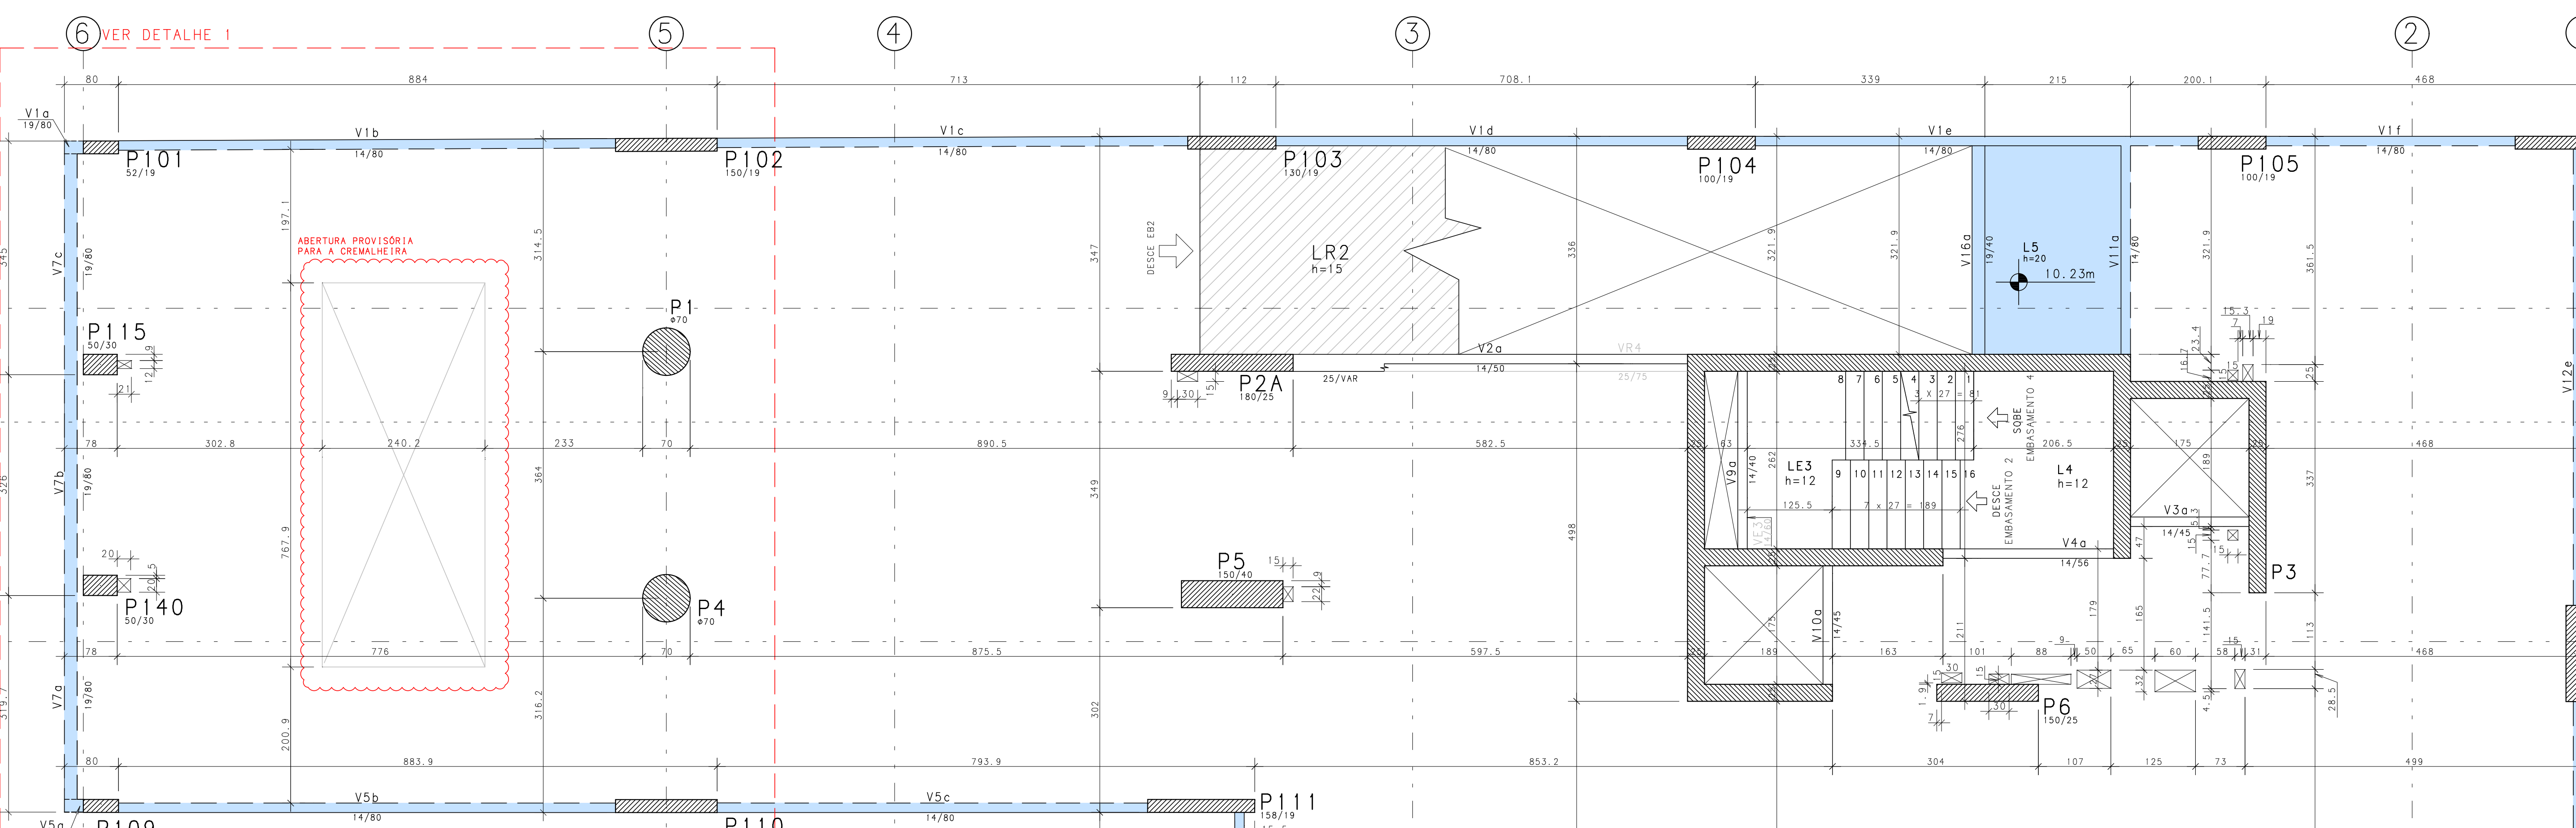


Legenda de desníveis		Lojes							
Car	Desnível cm	Elemento	Tipo	Altura cm	Elevação cm	PP t/m	FERM t/m	ACID t/m	TOT t/m
	150	L1	Mocico	20		0.500	0.200	0.250	0.950
	140	L2	Mocico	20		0.500	0.100	0.300	0.900
	130	L3	Mocico	20		0.500	0.100	0.300	0.900
	60	L4	Mocico	12		0.300	0.150	0.300	0.750
	20	L5	Mocico	20		0.500	0.100	0.250	0.850
		L62	Mocico	20	60	0.275	0.100	0.300	0.775
		LW1	Mocico	20		0.500	0.200	0.250	0.950

LEGENDA

 RAMPAS

NOTA 1: O PILAR P8 DEVE SER CONCRETADO COM FCK DE 45 MPa
ATÉ O NÍVEL +21.32 (PISO DO 2º PAVIMENTO)

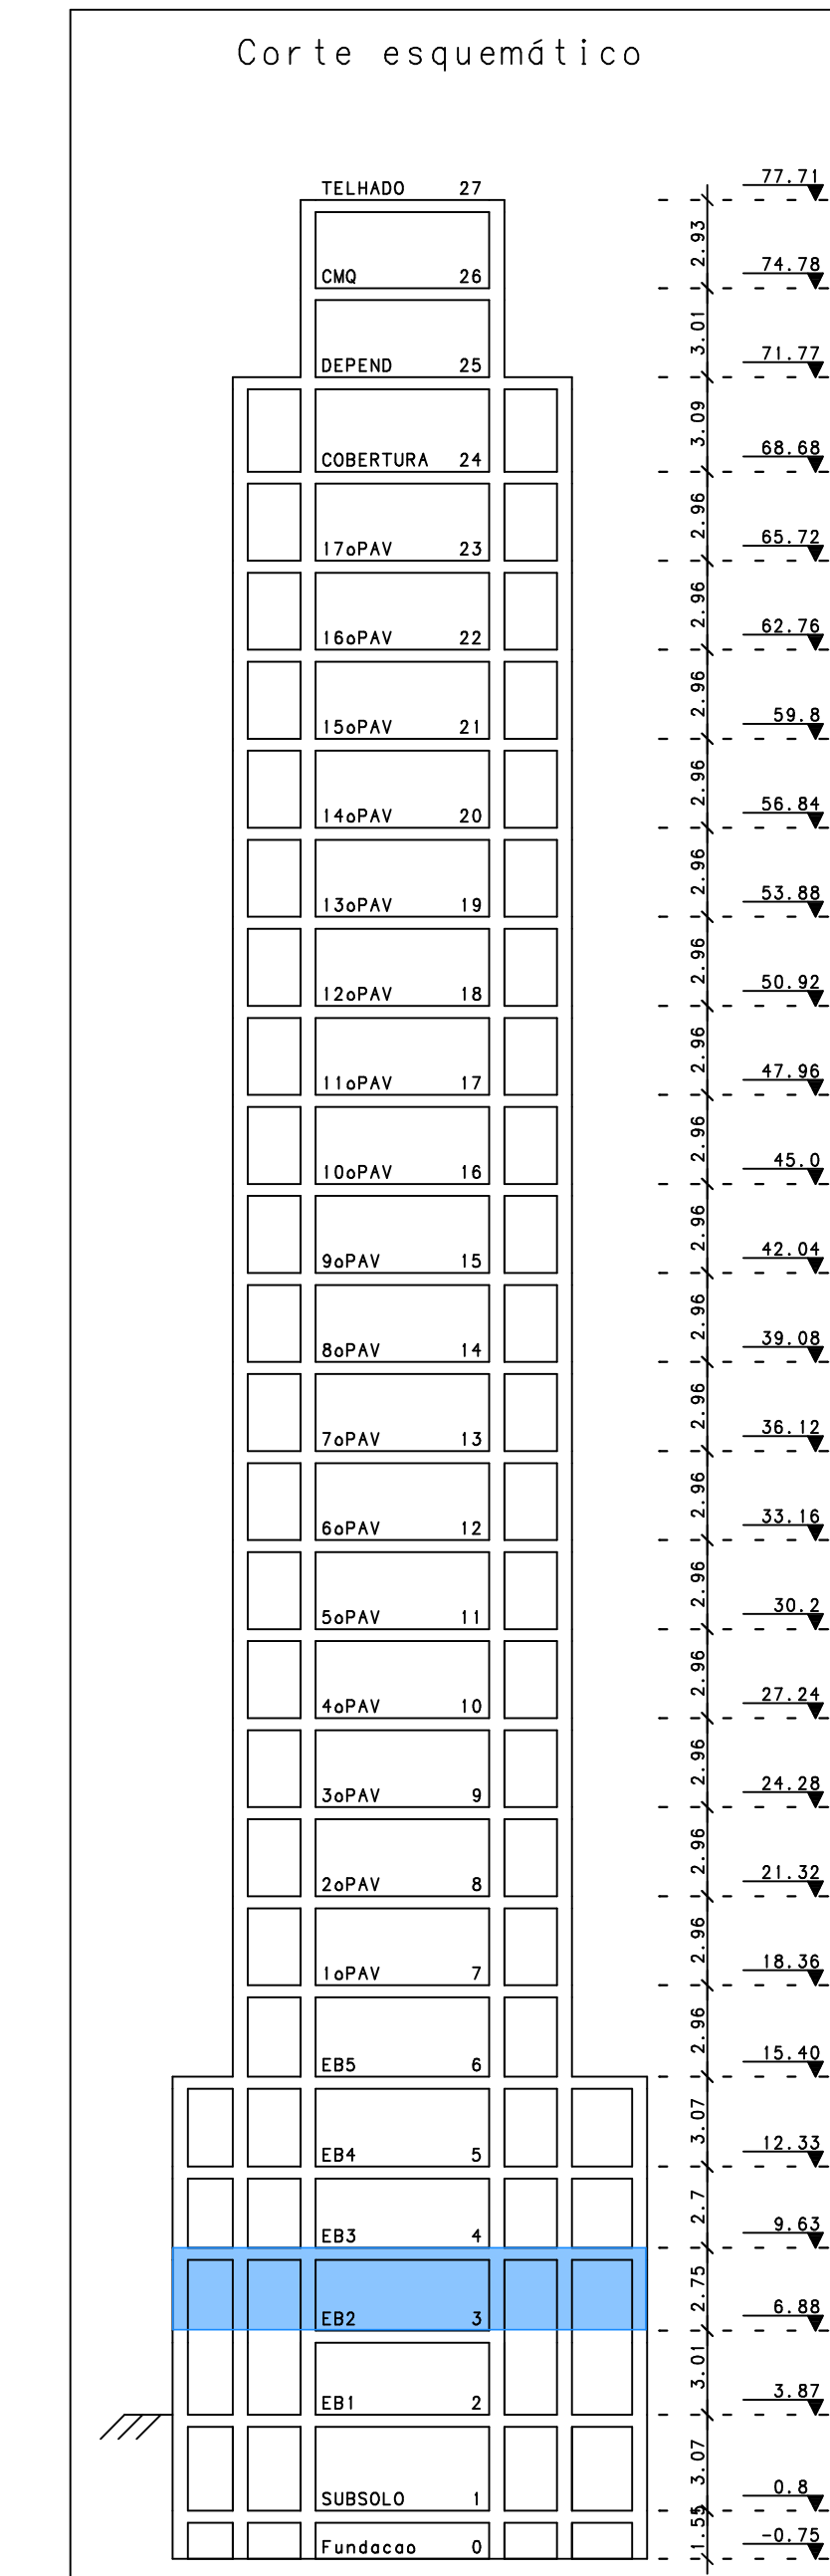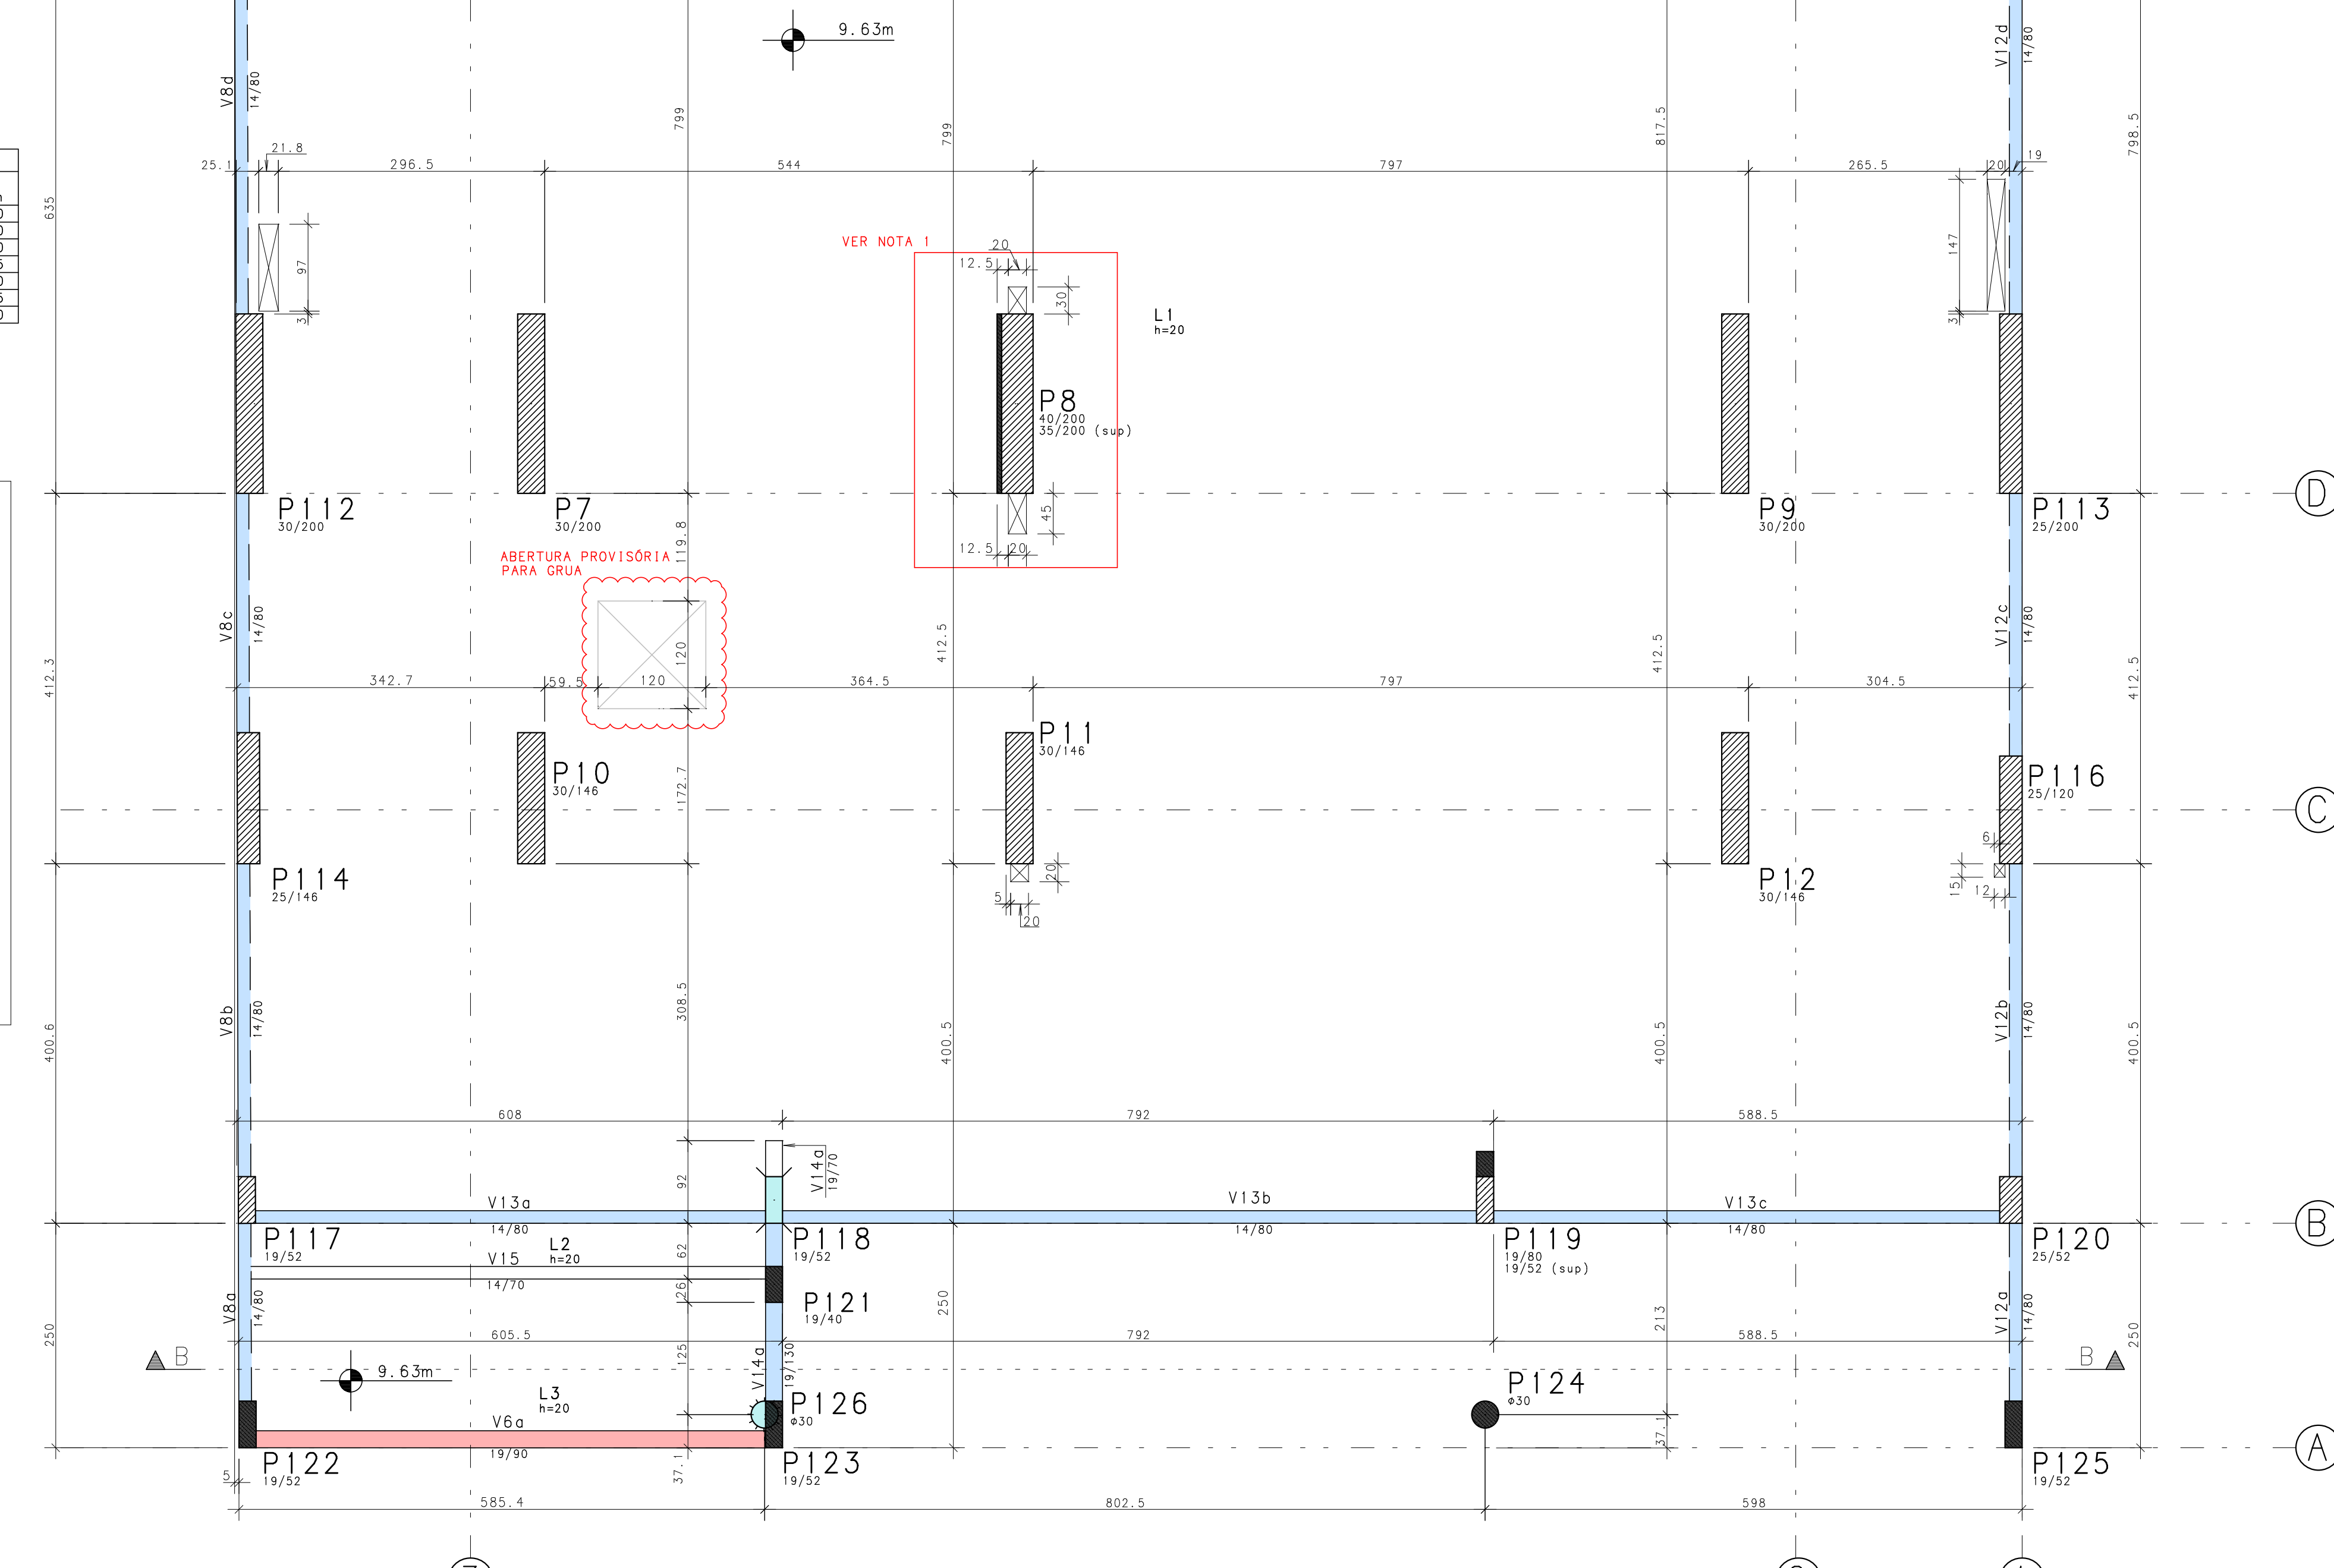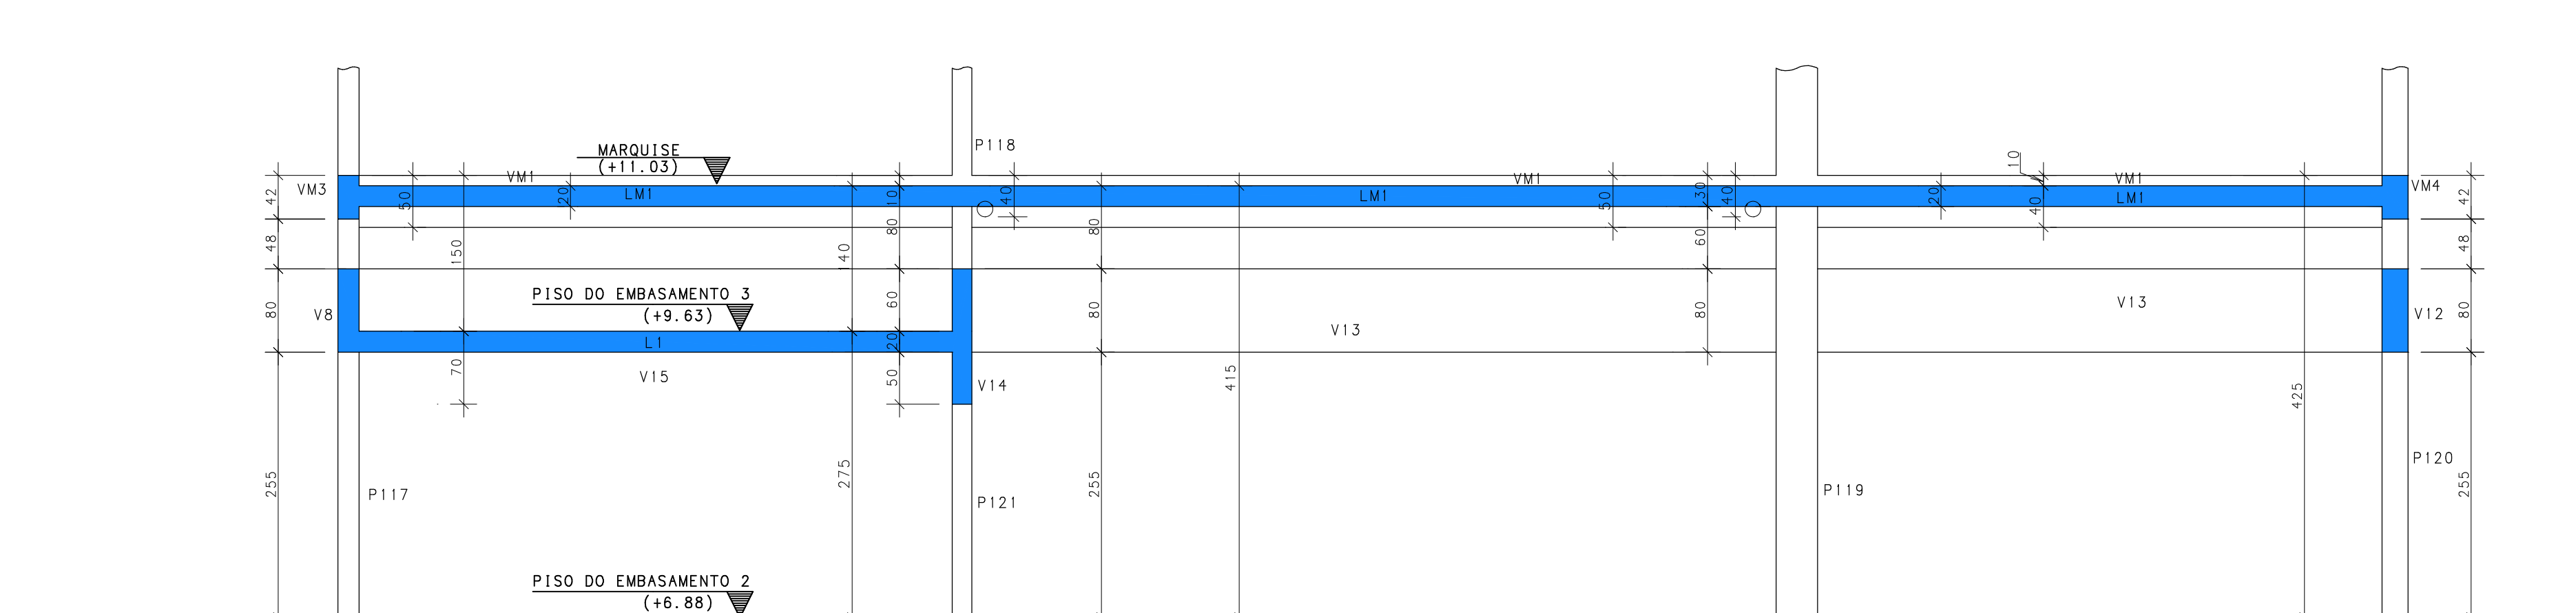

NOTAS GERAIS PARA O USO DESTES PROJETO :

A. DADOS GERAIS :

1. **EMPRESA RESPONSÁVEL POR ESTES PROJETOS :** **SIGMA CONSULTORIA & PROJETOS**

2. **EMPRESA ASSOCIADA PARA O PROJETO :** **ENGENHARIA & CONSULTORIA ESTRUTURAL - AMCE**,
C/O W. CARLOS DE MOURA, RUA JOSE DE ALMEIDA, 100, JARDIM BELLA VISTA, 05312-000, SÃO PAULO, SP.

3. **VEREDICTO :** AVALIAÇÃO DE DESEMPENHO DOS MATERIAIS E/OU SERVIÇOS PRESTADOS, QUANDO NECESSÁRIO, DESENVOLVIDA SOB COORDENAÇÃO E SUPERVISÃO DE TERCEIROS.

4. **REGRAS TÉCNICAS DE REFERÊNCIA :**

NBR 6118 - PROJETO DE ESTRUTURAS DE CONCRETO

NBR 6119 - CARGAS PARA O CÁLCULO DE ESTRUTURAS DE EDIFICAÇÕES

NBR 6120 - CARGAS DEVIDAS AO USO EM EDIFICAÇÕES

NBR 5671 - PARTICIPAÇÃO DOS INTERVENIENTOS EM SERVIÇOS E OBRAS DE ENGENHARIA E ARQUITETURA

NBR 12504 - Cálculo Técnico de Materiais e Materiais Componentes do Concreto

NBR 12505 - Cálculo Técnico de Materiais e Materiais Componentes do Concreto

NBR 12506 - Cálculo Técnico de Materiais e Materiais Componentes do Concreto

NBR 5532 - CONCRETO - EXATÃO DE COMPRESSÃO DE CORPOS-DE-PROVA CILÍNDRICOS

NBR 5538 - CONCRETO - EXATÃO DE COMPRESSÃO DE CORPOS-DE-PROVA CILÍNDRICOS

NBR 8029 - CONCRETO - DETERMINAÇÃO DO MÓDULO DE DEFORMAÇÃO ELÁSTICA E DEFORMAÇÃO TENSÃO - DEFORMAÇÃO

NBR 6152 - MATERIAIS METÁLICOS - DETERMINAÇÃO DAS PROPRIEDADES MECÂNICAS

NBR 6153 - MATERIAIS METÁLICOS - DETERMINAÇÃO DAS PROPRIEDADES MECÂNICAS

NBR 6154 - PRODUTO METAL - EXATÃO DE DORMIMENTO SIMIL-QUADRO

NBR 7477 - DETERMINAÇÃO DO COEFICIENTE DE CONFORMAÇÃO SUPERFICIAL

NBR 7480 - DETERMINAÇÃO DO COEFICIENTE DE CONFORMAÇÃO SUPERFICIAL

NBR 7481 - DETERMINAÇÃO DO COEFICIENTE DE CONFORMAÇÃO SUPERFICIAL

NBR 7482 - BARRAS E FIOS AO ESTADO DESTINADOS A ANÁLISAS PARA CONCRETO ARMADO

B. COTAGEM :

1. **DESCRIÇÃO :** OBRAS DE CONFORMAÇÃO DO PROJETO ESTRUTURAL, FACE NOS PROJETOS DE ARQUITETURA, INSTALAÇÕES E DEMAIS SUBSIDIÓRIAS, TÁIS COMO COTAS, NÍVEIS, DIMENSÕES DAS PEÇAS ESTATIZADAS, E/OU DESEMPENHO DE MATERIAIS E/OU SERVIÇOS PRESTADOS, QUANDO NECESSÁRIO, DEVIDO ÀS RESPONSABILIDADES PELO DESEMPENHO DO PROJETO ESTRUTURAL.

C. MATERIAIS :

1. **CONCRETO :**

VER EM NOTAS GERAIS

2. **ACAO :** AC-20, AC-25, AC-30, AC-35, AC-40

3. **FORMA :** FORMAS PLANEJADAS

4. **PROTEÇÃO E DORMIMENTO DAS BARRAS E ESCORAMENTOS NÃO FAZ PARTE DO PROJETO E DEVEM SER SOLICITADOS.**

D. EXECUÇÃO DA ESTRUTURA :

A EXECUÇÃO DA ESTRUTURA E DE RESPONSABILIDADE DA EMPRESA CONTRATADORA E DEVERÁ SER DEVIDAMENTE SUPERVISADA POR UM TECNÓLOGO DA ESTRUTURA, DESEMPENHO RESPONSÁVEL. PARA O PROJETO DEVER OBRIGATORIAMENTE SER RECOMENDADA A CARGA ADOTADA PARA ESTE PROJETO.

5. **CARGA ADOTADA PARA ESTE PROJETO :**

6. **RESUMO DA EXECUÇÃO DE ESTIMATIVA DE CONCRETO - PRECISÃO :**

7. **RESUMO DA EXECUÇÃO DE ESTIMATIVA DE CONCRETO - PRECISÃO :**

99. **RESUMO DA EXECUÇÃO DE ESTIMATIVA DE**

4. MEMORIAL DESCRITIVO PARA DESCRIMINHAMENTO DA ESTRUTURA (PARA DESCRIMINHAMENTO DA RECEITA DO CONDOMÍNIO ATENDENDO AO DESCRIMINHAMENTO DE PÁGORES 1, 7, 12, 13 E 28 D145)

TEMPO DECORRIDO JUNO 4.000 (CONDOMÍNIO 2145)	E ESCORRIMENTO E SEM MANTENIDO
0	>100%
7	100%
12	50%
13	25%
28	SEM ESCORRIMENTO


1. FUNDAÇÕES

01. O PROJETO DE FUNDAÇÕES, DETERMINAÇÃO DA TAXA ADMISSÍVEL NO TERRENO, DISPOSIÇÃO E DIMENSIONAMENTO DE ESTACAS, COTA DE IMPLANTAÇÃO, METODOLOGIA DE EXECUÇÃO, INTERAÇÃO COM VIZINHOS, ETC... E SE RESPONSABILIDADE DA EMPRESA DE CONTROLE DE OBRAS DE FUNDAÇÕES DEVERÁ SEGUIR AS RECOMENDAÇÕES DA NBR-8122 - PROJETO E EXECUÇÃO DE FUNDAÇÕES

4. FUNDOS

4.1. FUNDOS EM LÍQUIDE E VIGAS DEVERÃO RECEBER AMPLAÇÃO DE RETENÇÃO PARALELA. PAROS PARA INDICAÇÃO DO PODERER ETER EXECUTADOS COM NÚCLEO AMPLADO.

CONVENÇÃO DE PILARES

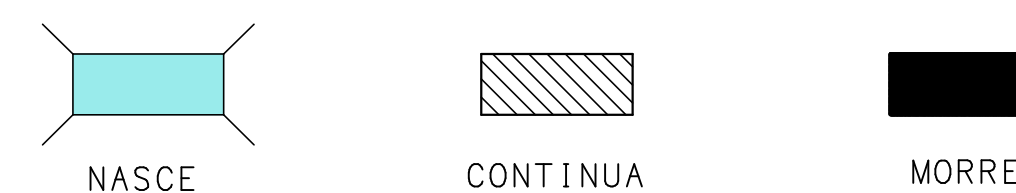

NOTAS GERAIS

- 1- DIMENSÕES EM CENTÍMETRO, NÍVEIS EM METRO
2- PROPRIEDADES DO CONCRETO:
- $f_{ck} > 40 \text{ MPa}$ (400 kg/cm^2)
- MÓDULO DE DEFORMAÇÃO TANGENTE INICIAL $> 26 \text{ GPa}$
- CONSUMO MÍNIMO DE CIMENTO: 320 kg/m^3
- FATOR ÁGUA/CIMENTO MÁXIMO: 0.55
3- UTILIZAR OBRIGATORIAMENTE EM CONJUNTO COM O DESENHO DE FURAÇÃO

ATENÇÃO/PLOTAGEM

-OS ARQUIVOS DXF SERVEM APENAS COMO BASE PARA A ARQUITETURA E DEMAIS COMPLEMENTARES.
-PLOTAR APENAS O ARQUIVO PDF-COLORIDO CASO CONTRÁRIO PODERA HAVER PERDA DE INFORMAÇÕES

05		
04	05/08/2026	AJUSTADO CONFORME MARKUP
03	17/07/2026	AJUSTADO CONFORME MARKUP
02	22/05/2026	AJUSTADA POSIÇÃO DE ABERTURA DA GRUA E VR4
01	10/03/2026	CONFORME COMENTARIOS DO AUDITOR
00	06/01/2025	EMISSÃO INICIAL



EMPREENHIMENTO E LOCAL	PROJETO
PDM 1050	ESTRUTURA

RUA PRUDENTE DE MORAIS, 1050 - IPANEMA, RIO DE JANEIRO - RJ	FASE EXECUTIVO
TÍTULO DO DESENHO	ESCALA

FORMA	1:50
DISO DO EMPASAMENTO 3	DATA

P130 DO EMBASAMENTO 3 (TETO DO EMBASAMENTO 2)	05/08/2026 ARQUIVO
--	-----------------------

DIMENSÃO DA FOLHA: 1374x841mm (A0)