


SIGMA 3 CONSULTORIA & PROJETOS - RUA JOAQUIM TAVARA, 72 - SALAS 108/110 - IPRANEMA, RIO DE JANEIRO - RJ 22.070-000 33.213.12

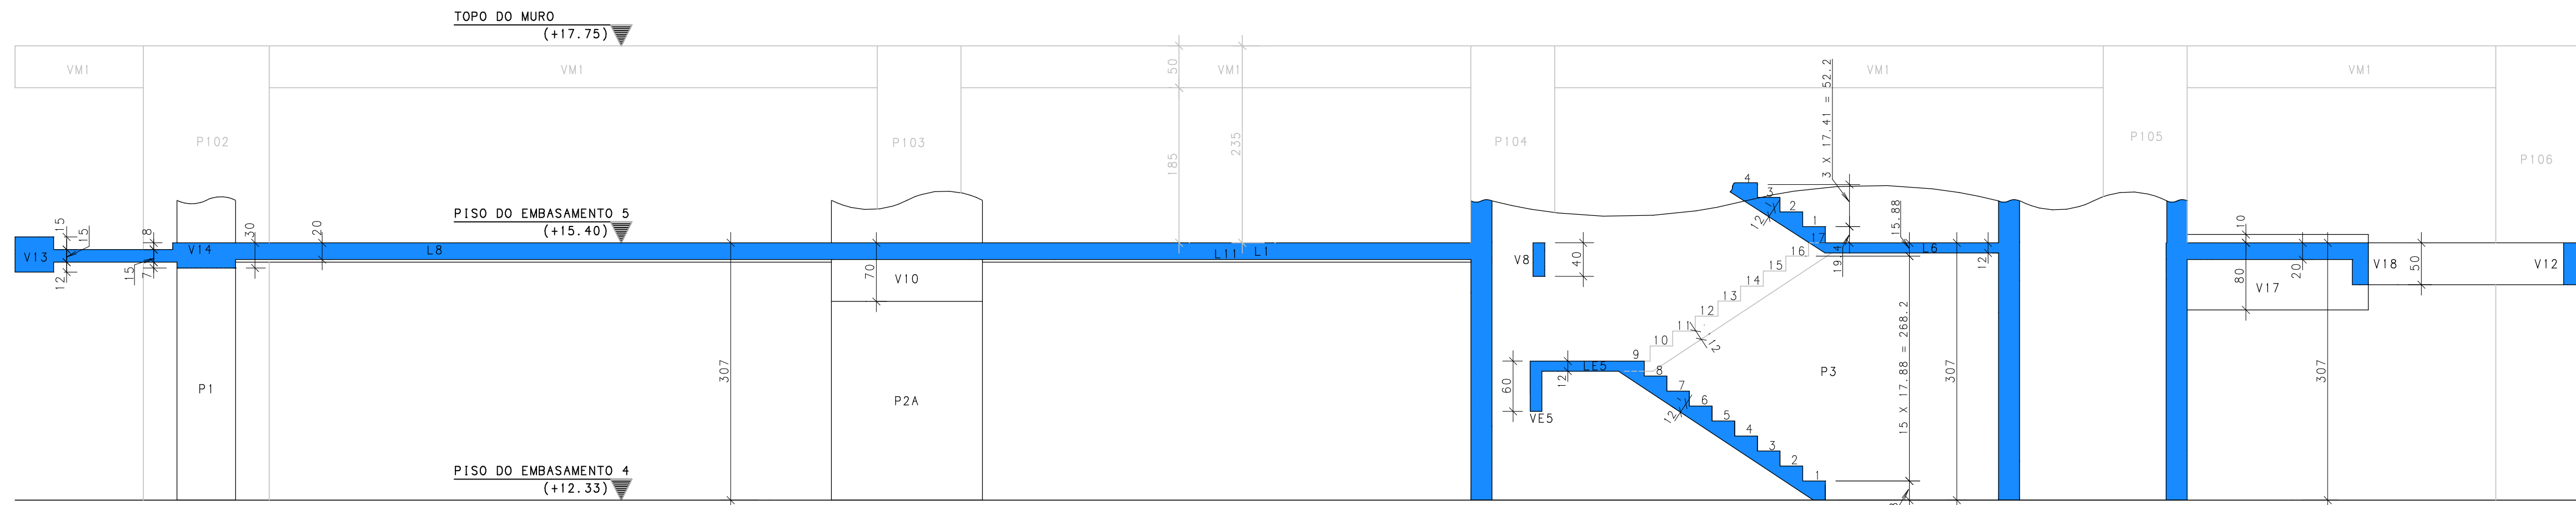

FORMA AUXILIAR 1 - (+17.75m)

