



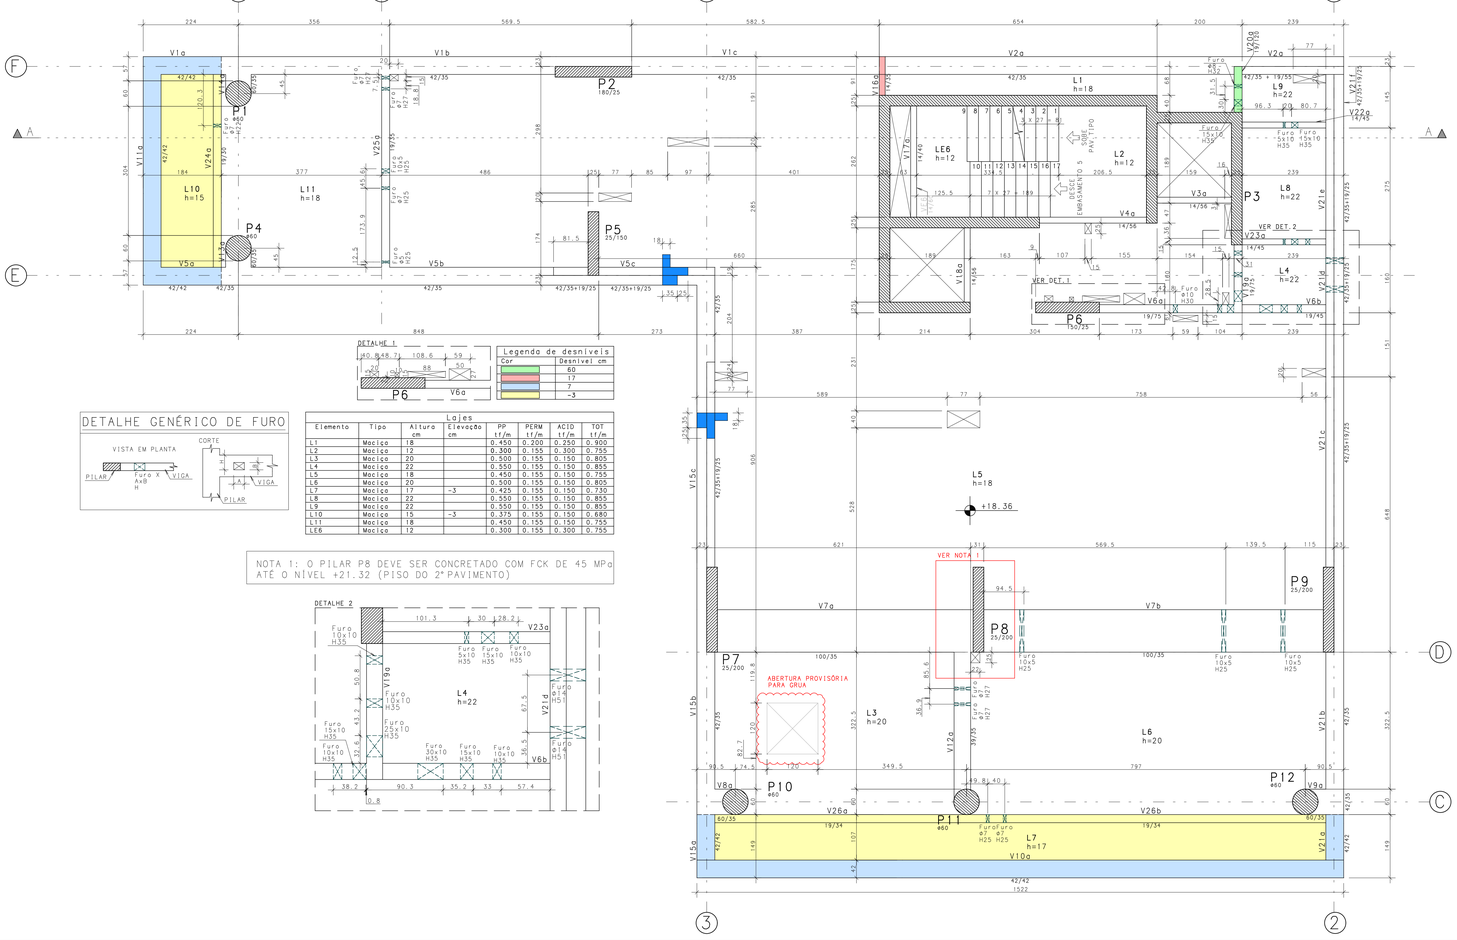

Corte esquemático

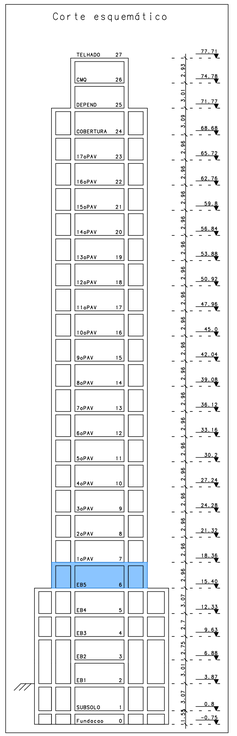

NOTAS GERAIS PARA O USO DESTE PROJETO :

A. DIREITOS AUTORAIS

ESTE PROJETO É PROPRIEDADE DE **SIGMA1 CONSULTORIA & PROJETOS** FILIADO A ASSOCIAÇÃO BRASILEIRA DE ENGENHARIA E CONSULTORIA ESTRUTURAL - ABECE. SOB O Nº 0789, NÃO SENDO PERMITIDA SUA UTILIZAÇÃO PARA QUALQUER FINALIDADE QUE NÃO SE RELACIONE COM A EXECUÇÃO ESPECIFICA DESTA OBRA, SENDO TERMINANTEMENTE VEDADA SUA COLOCAÇÃO À DISPOSIÇÃO DE TERCEIROS.

B. NORMAS TÉCNICAS DE REFERÊNCIA

NBR 6118	PROJETO DE ESTRUTURAS DE CONCRETO
NBR 6120	CARGAS PARA O CÁLCULO DE ESTRUTURAS DE EDIFICAÇÕES
NBR 6123	FORÇAS DEVIDAS AO VENTO EM EDIFICAÇÕES
NBR 5671	PARTICIPAÇÃO DOS INTERVENIENTES EM SERVIÇOS E OBRAS DE ENGENHARIA E ARQUITETURA
NBR 12654	CONTROLE TECNOLÓGICO DE MATERIAIS COMPONENTES DO CONCRETO
NBR 12655	CONCRETO – PREPARO, CONTROLE E RECEBIMENTO
NBR 5738	MOLDAGEM E CURA DE CORPOS CILÍNDRICOS OU PRIS MÁTICOS DE CONCRETO – MÉTODO DE ENSAIO
NBR 5739	CONCRETO – ENSAIO DE COMPRESSÃO DE CORPOS-DE-PROVA CILÍNDRICOS – MÉTODO DE ENSAIO
NBR 8522	CONCRETO – DETERMINAÇÃO DO MÓDULO DE DEFORMAÇÃO ESTÁTICA E DIAGRAMA TENSÃO x DEFORMAÇÃO – MÉTODO DE ENSAIO
NBR 6152	MATERIAIS METÁLICOS-DETERMINAÇÃO DAS PROPRIEDADES MECÂNICAS A TRAÇÃO-MÉTODO DE ENSAIO
NBR 6153	PRODUTO METÁLICO – ENSAIO DE DOBRAMENTO SEMI-GUIADO
NBR 7477	DETERMINAÇÃO DO COEFICIENTE DE CONFORMAÇÃO SUPERFICIAL DE BARRAS E FIOS DE AÇO DESTINADOS A ARMADURA DE CONCRETO ARMADO MÉTODO DE ENSAIO
NBR 7480	BARRAS E FIOS DE AÇO DESTINADOS A ARMADURAS PARA CONCRETO ARMADO – ESPECIFICAÇÃO

C. GEOMETRIA

OS ELEMENTOS DE CONFORMIDADE DO PROJETO ESTRUTURAL FACE AOS PROJETOS DE ARQUITETURA, INSTALAÇÕES E DEMAIS DISCIPLINAS TAIS COMO DATAS, NÍVEIS, DIMENSÕES DAS PEÇAS ESTRUTURAIS, POÇOS DE ELEVADORES, ESCADAS, ETC. DEVEM SER VALIDADOS PELOS ARQUITETOS RESPONSÁVEIS PELO DESENVOLVIMENTO DO PROJETO EXECUTIVO.

D. MATERIAIS

01. CONCRETO

VER EM NOTAS GERAIS

02.AÇO EM ARMADURA PASSIVA

02.1. AÇO CA-50A / CA-60B

03.FORMAS E ESCORAMENTOS.

O PROJETO E DIMENSIONAMENTO DAS FORMAS E ESCORAMENTOS NÃO FAZ PARTE DO ESCOPO DE NOSSOS SERVIÇOS.

E. EXECUÇÃO DA ESTRUTURA.

A EXECUÇÃO DA ESTRUTURA É DE RESPONSABILIDADE DA EMPRESA CONSTRUTORA E DEVERÁ CONTAR COM A CONSULTORIA DE UM TECNOLOGISTA DE MATERIAIS. O ENGENHEIRO RESPONSÁVEL PELA EXECUÇÃO DEVERÁ OBEDECER AS RECOMENDAÇÕES DA NBR14931-EXECUÇÃO DE ESTRUTURAS DE CONCRETO-PROCEDIMENTOS.

F. CARGAS ADOTADAS PARA ESTE PROJETO

01. FORÇAS DEVIDO AO VENTO - CONFORME NBR 6123

02. CARGAS ACIDENTAIS NÃO PARTICULARES : CONFORME NBR 6120 DE ACORDO COM PROJETO ARQUITETONICO APROVADO EM PREFEITURA.

03. PESO PRÓPRIO DO CONCRETO : 2500 kgf / m3

04. ALVENARIAS (COM REVESTIMENTOS) :1300 kgf / m3
- ESPESSURA DA ALVENARIA ACABADA CONFORME PROJ. ARQUITETÔNICO

05. LAJES (CONTRAPISO + REVESTIMENTOS) :100 kgf / m2
OBS : AS CARGAS EVENTUALMENTE INFORMADAS NAS PRANCHAS DE FORMAS PREVALECEM SOBRE AS CARGAS AQUI INDICADAS.

G.COBRIMENTOS

	PAV. REVESTIDOS	
	COBERTOS	DEMAIS PAV.
01. LAJES: POSITIVA/NEGATIVA	2,0/1,5 cm	2,0/2,0 cm
02. VIGAS:	2,5 cm	2,5 cm
03. PILARES:	3,0 cm	3,0 cm
04. BLOCOS SOBRE ESTACAS / SAPATAS: 3,0 cm		
05. CINTAS / LAJES DE SUBPRESSÃO: 3,0 cm		
06. PAREDES DE SUBSOLO: 3,0 cm		
07. RESERVATÓRIOS: 3,0 cm		

OBS: 1) DEVERÁ HAVER CONTROLE RIGOROSO DE QUALIDADE E RÍGIDOS LIMITES DE TOLERÂNCIA DAS MEDIDAS DURANTE A EXECUÇÃO.
2) COBRIMENTOS INFORMADOS NOS DESENHOS DE ARMAÇÃO PREVALECEM EM RELAÇÃO À TABELA ACIMA.

H. MEMORIAL DESCRITIVO PARA DESCIMBRAMENTO DA ESTRUTURA
(PARA DESENVOLVIMENTO DA RESISTÊNCIA DO CONCRETO ATENDENDO AS EXPECTATIVAS DE VALORES A 7,14,21 E 28 DIAS)

TEMPO DECORRIDO APÓS A CONCRETAGEM (DIAS)	% ESCORAMENTO A SER MANTIDO
0	
7	>100%
14	100%
21	50%
28	25%
	SEM ESCORAMENTO

I. FUNDAÇÕES

01.O PROJETO DE FUNDAÇÕES, DETERMINAÇÃO DA TAXA ADMISSIVEL NO TERRENO, DISPOSIÇÃO E DIMENSIONAMENTO DE ESTACAS, COTA DE IMPLANTAÇÃO, METODOLOGIA DE ESCAVAÇÃO, INTERAÇÃO COM VIZINHOS, ETC... É DE RESPONSABILIDADE DA EMPRESA DE CONSULTORIA DE FUNDAÇÕES DEVENDO SEGUIR AS RECOMENDAÇÕES DA NBR-6122 - PROJETO E EXECUÇÃO DE FUNDAÇÕES

J. FURAÇÕES

01. FUROS EM LAJES E VIGAS DEVERÃO RECEBER ARMADURA DE REFORÇO PADRÃO.
02.FUROS NÃO INDICADOS SÓ PODERÃO SER EXECUTADOS COM NOSSA APROVAÇÃO.

NOTAS GERAIS

1- DIMENSÕES EM CENTÍMETRO, NÍVEIS EM METRO

2- PROPRIEDADES DO CONCRETO:
- Fck > 40 MPa (400kg/cm²)
- MODULO DE DEFORMAÇÃO TANGENTE INICIAL > 32 GPa
- CONSUMO MINIMO DE CIMENTO: 350kg/m³
- FATOR ÁGUA/CIMENTO MÁXIMO: 0,55

3- UTILIZAR OBRIGATORIAMENTE EM CONJUNTO COM O DESENHO DE FURAÇÃO

ATENÇÃO/PLOTAGEM

-OS ARQUIVOS DXF SERVEM APENAS COMO BASE PARA A ARQUITETURA E DEMAIS COMPLEMENTARES.
-PLOTAR APENAS O ARQUIVO PDF-**COLORIDO** CASO CONTRÁRIO PODERÁ HAVER PERDA DE INFORMAÇÕES

REV.	DATA	DESCRIÇÃO
05		
04		
03	24/08/2026	AJUSTADOS FUROS NAS VIGAS V22, V23 E V6
02	22/05/2026	ATUALIZADO CONFORME FURAÇÃO E MARK-UP
01	16/04/2025	CONFORME COMENTÁRIOS DA ARQUITETURA
00	06/01/2025	EMISSÃO INICIAL

CONVENÇÃO DE PILARES

NASCE | CONTINUA | MORRE

SIGMA1 CONSULTORIA & PROJETOS
RUA URUGUAIANA, 10-SALA 2307- CENTRO- RIO DE JANEIRO-RJ
TEL/FAX: (55-21)2508-8541 E-MAIL:administracao@sigma1.eng.br
www.sigma1.eng.br
ENG. EDUARDO VIDAL CABRAL CREA: 1982077/D
ENG. MAURICIO DOS SANTOS SGARBI GOULART CREA: 2005119508
CONSULTORIA & PROJETOS

NÚMERO DA OBRA: 578
RESPONSÁVEL: MAURICIO SGARBI
COORDENAÇÃO: VINÍCIUS CORDEIRO
PROJETISTA: VINÍCIUS CORDEIRO
DESENHO Nº: ST 008

EMPREENDIMENTO E LOCAL:
PDM 1050
RUA PRUDENTE DE MORAIS, 1050 - IPANEMA, RIO DE JANEIRO - RJ

PROJETO: ESTRUTURA
FASE: EXECUTIVO

TÍTULO DO DESENHO:
FORMA
PISO DO 1°PAVIMENTO
(TETO DO EMBASAMENTO 5)

ESCALA: 1:50
DATA: 24/08/2026
ARQUIVO: PDM-EST-EX-008-PD-1PV-FORM_R05

DIMENSÃO DA FOLHA: 121lx594mm (A1L)

SIGMA 1 - CONSULTORIA & PROJETOS PL. PDM-EST-EX-008-PD-1PV-FORM_R03.DXF 24/08/2026 16:58:39