
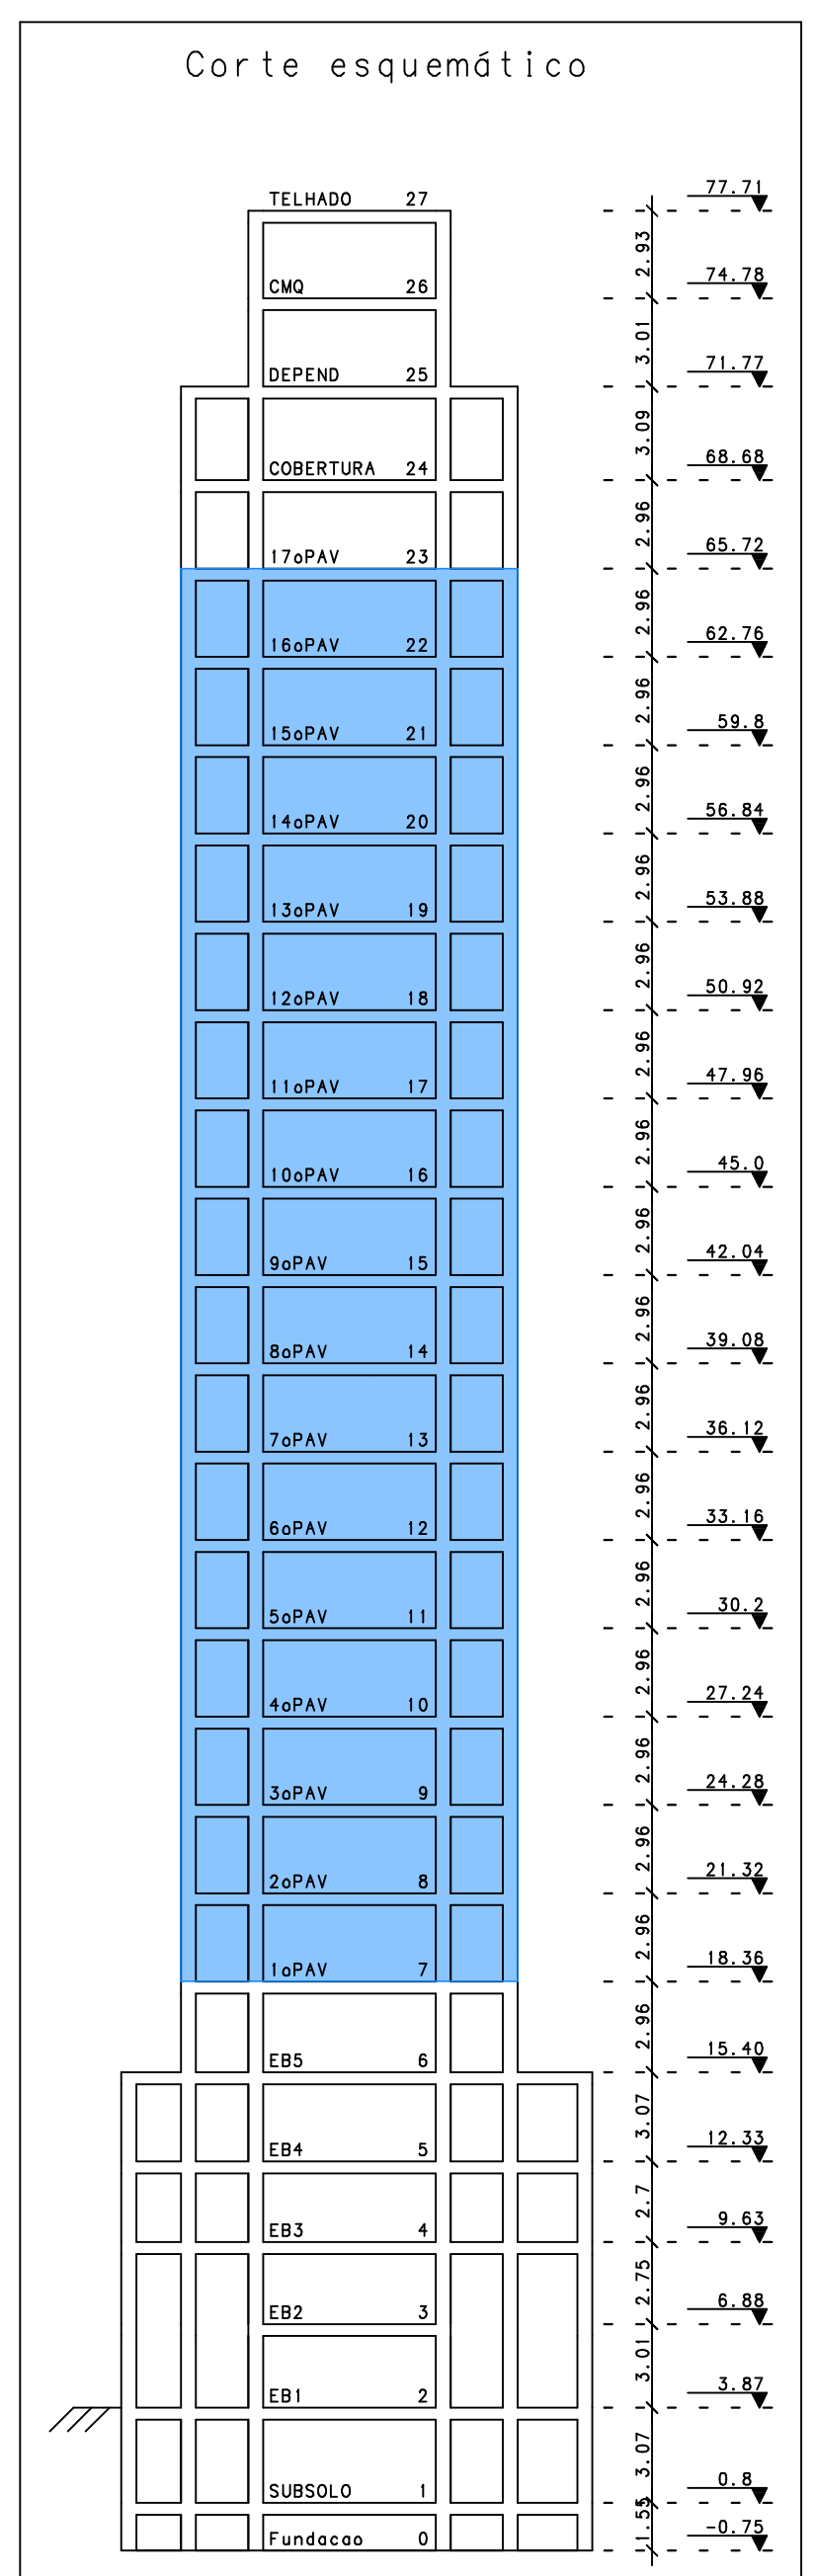


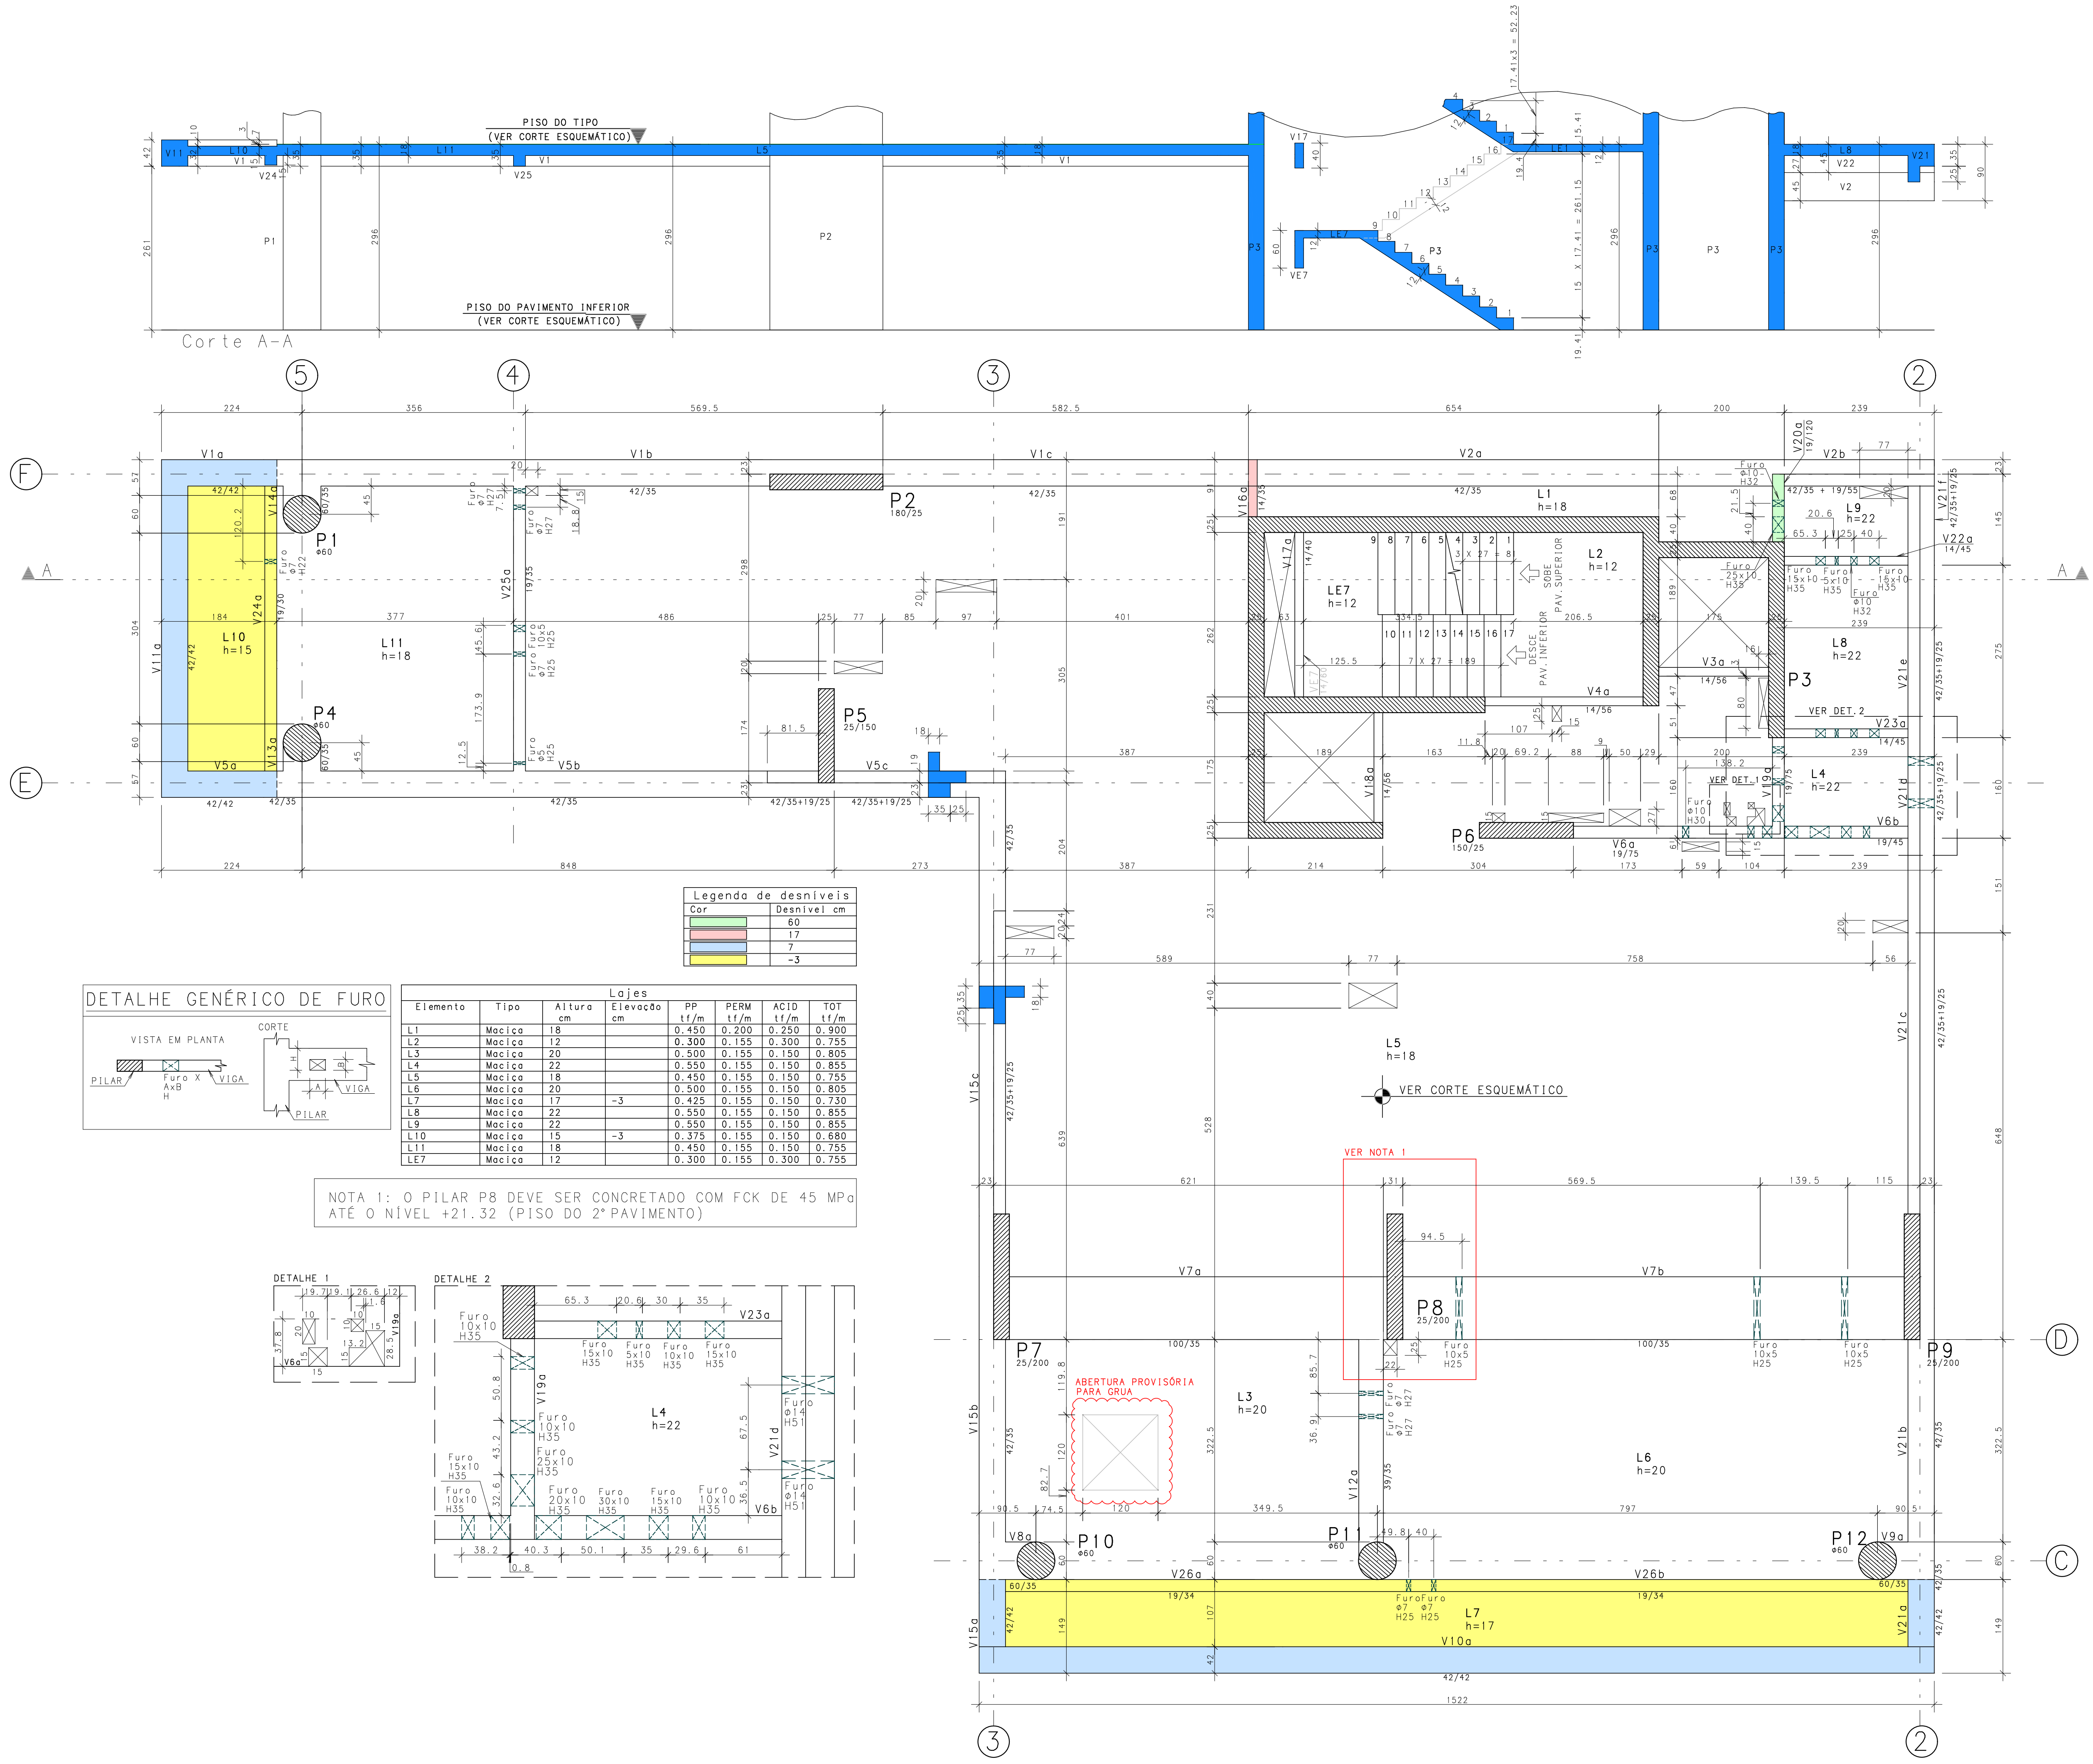

CONVENÇÃO DE PILARES	
	NASCE
	CONTINUA
	MORRE

NOTAS GERAIS PARA O USO DESTA PROJETO :

A. DIREITOS AUTORAIS

ESTE PROJETO É PROPRIEDADE DE SIGMA CONSULTORIA & PROJETOS FILIADO A ASSOCIAÇÃO BRASILEIRA DE ENGENHARIA E CONSULTORIA ESTRUTURAL - ABCE, SOB Nº. 0786, NÃO SENDO PERMITIDA SUA UTILIZAÇÃO PARA QUALQUER FINALIDADE QUE NÃO SE RELACIONE COM A EXECUÇÃO ESPECÍFICA DESTA OBRA, SENDO TERMINANTEMENTE VEDADA SUA COLOCAÇÃO À DISPOSIÇÃO DE TERCEIROS.

B. NORMAS TÉCNICAS DE REFERÊNCIA

NBR 6118

PROJETO DE ESTRUTURAS DE CONCRETO

NBR 6120

CARGAS PARA O CÁLCULO DE ESTRUTURAS DE EDIFICAÇÕES

NBR 6123

FORÇAS DEVIDAS AO VENTO EM EDIFICAÇÕES

NBR 5671

PARTICIPAÇÃO DOS INTERVENIENTES EM SERVIÇOS E OBRAS DE ENGENHARIA E ARQUITETURA

NBR 12654

CONTROLE TECNOLÓGICO DE MATERIAIS COMPONENTES DO CONCRETO

NBR 12655

CONCRETO - PREPARO, CONTROLE E RECEBIMENTO

NBR 5738

MOLDEAGEM E CURA DE CORPOS CILÍNDRICOS OU PRISMA MÁTICOS DE CONCRETO - MÉTODO DE ENSAIO

NBR 5739

CONCRETO - ENSAIO DE COMPRESSÃO DE CORPOS-DE-PROVA CILÍNDRICOS - MÉTODO DE ENSAIO

NBR 8522

CONCRETO - DETERMINAÇÃO DO MÓDULO DE DEFORMAÇÃO ELÁSTICA E DIAGRAMA TENSÃO x DEFORMAÇÃO - MÉTODO DE ENSAIO

NBR 6152

MATERIAIS METÁLICOS-DETERMINAÇÃO DAS PROPRIEDADES MECÂNICAS A TRAÇÃO-MÉTODO DE ENSAIO

NBR 6153

PRODUTO METÁLICO - ENSAIO DE DOBRAMENTO SEMI-GUIADO

NBR 7477

DETERMINAÇÃO DO COEFICIENTE DE CONFORMAÇÃO SUPERFICIAL DE BARRAS E FIOS DE AÇO DESTINADOS A ARMADURA DE CONCRETO ARMADO MÉTODO DE ENSAIO

NBR 7480

BARRAS E FIOS DE AÇO DESTINADOS A ARMADURAS PARA CONCRETO ARMADO - ESPECIFICAÇÃO

C. GEOMETRIA

OS ELEMENTOS DE CONFORMIDADE DO PROJETO ESTRUTURAL FACE AOS PROJETOS DE ARQUITETURA, INSTALAÇÕES E DEMAIS DISCIPLINAS, TAIS COMO COTAS, NÍVEIS, DIMENSÕES DAS PEÇAS ESTRUTURAIS, POÇOS DE ELEVADORES, ESCADAS, ETC. DEVEM SER VALIDADOS PELOS ARQUITETOS RESPONSÁVEIS PELO DESENVOLVIMENTO DO PROJETO EXECUTIVO.

D. MATERIAIS

01. CONCRETO

VER EM NOTAS GERAIS

02. AÇO EM ARMADURA PASSIVA

02.1. AÇO CA-50A / CA-60B

03. FORMAS E ESCORAMENTOS

O PROJETO E DIMENSIONAMENTO DAS FORMAS E ESCORAMENTOS NÃO FAZ PARTE DO ESCOPO DE NOSSOS SERVIÇOS.

E. EXECUÇÃO DA ESTRUTURA

A EXECUÇÃO DA ESTRUTURA E DE RESPONSABILIDADE DA EMPRESA CONSTRUTORA E DEVERÁ CONTAR COM A CONSULTORIA DE UM TECNOLÓGISTA DE MATERIAIS. O ENGENHEIRO RESPONSÁVEL PELA EXECUÇÃO DEVERÁ OBEDECER AS RECOMENDAÇÕES DA NBR-6118-EXECUÇÃO DE ESTRUTURAS DE CONCRETO-PROCEDIMENTOS.

F. CARGAS ADOPTADAS PARA ESTE PROJETO

01. FORÇAS DEVIDO AO VENTO - CONFORME NBR 6123

02. CARGAS ACIDENTAIS NÃO PARTICULARES - CONFORME NBR 6120 DE ACORDO COM PROJETO ARQUITETÔNICO APROVADO EM PREFEITURA

03. PESO PRÓPRIO DO CONCRETO - 2500 kgf / m³

04. ALVENARIAS (COM REVESTIMENTOS) - 1500 kgf / m³

+ ESPESSURA DA ALVENARIA ACABADA CONFORME PROJ. ARQUITETÔNICO

05. LAJES (CONTRAPISO + REVESTIMENTOS) - 100 kgf / m²

06. PAREDES DE SUBSOLO - 5,0 cm

07. RESERVATÓRIOS - 5,0 cm

G. COBERTIMENTOS

01. LAJES: POSITIVA/NEGATIVA 2,0/1,5 cm 2,0/2,0 cm

02. VIGAS: 2,5 cm 2,5 cm

03. PILARES: 3,0 cm 3,0 cm

04. BLOCOS SOBRE ESTACAS / SAPATAS: 3,0 cm

05. CINTAS / LAJES DE SUPRESSÃO: 3,0 cm

06. PAREDES DE SUBSOLO: 5,0 cm

07. RESERVATÓRIOS: 5,0 cm

OBS: 1) DEVERÁ HAVER CONTROLE RIGOROSO DE QUALIDADE E RÍGIDOS LIMITES DE TOLERÂNCIA DAS MEDIDAS DURANTE A EXECUÇÃO.

2) COBERTIMENTOS INFORMADOS NOS DESENHOS DE ARMADURA PREVALECEM EM RELAÇÃO À TABELA ACIMA.

H. MEMORIAL DESCRITIVO PARA DESCRIMBRAMENTO DA ESTRUTURA

(PARA DESENVOLVIMENTO DA RESISTÊNCIA DO CONCRETO ATENDENDO AS EXPECTATIVAS DE VALORES A 7, 14, 21 E 28 DIAS)

TEMPO DECORRIDO APÓS A CONCRETAGEM (DIAS)

7

14

21

28

>100%

100%

50%

25%

SEM ESCORAMENTO

1. FUNDAMENTOS

01. O PROJETO DE FUNDAMENTOS, DETERMINAÇÃO DA TAXA ADMISSÍVEL NO TERRENO, DISPOSIÇÃO E DIMENSIONAMENTO DE ESTACAS, COTA DE IMPLANTAÇÃO, METODOLOGIA DE ESCAVAÇÃO, INTERAÇÃO COM VIZINHOS, ETC., É DE RESPONSABILIDADE DA EMPRESA DE CONSULTORIA DE FUNDAMENTOS DEVENDO SEGUIR AS RECOMENDAÇÕES DA NBR-6122 - PROJETO E EXECUÇÃO DE FUNDAMENTOS

2. FURAÇÕES

01. FUROS EM LAJES E VIGAS DEVERÃO RECEBER ARMADURA DE REFORÇO PADRÃO.

02. FUROS NÃO INDICADOS SÓ PODERÃO SER EXECUTADOS COM NOSSA APROVAÇÃO.

NOTAS GERAIS

1- DIMENSÕES EM CENTÍMETRO. NÍVEIS EM METRO

2- PROPRIEDADES DO CONCRETO

- Fck > 40 MPa (400 kg/cm²)

- MÓDULO DE DEFORMAÇÃO TANGENTE INICIAL > 32 GPa

- CONSUMO MÍNIMO DE CIMENTO: 350 kg/m³

- FATOR ÁGUA/CEMENTO MÁXIMO: 0,55

3- UTILIZAR OBRIGATORIAMENTE EM CONJUNTO COM O DESENHO DE FURAÇÃO

ATENÇÃO/PLOTAGEM

- OS ARQUIVOS DXF SERVEM APENAS COMO BASE PARA A ARQUITETURA E DEMAIS COMPLEMENTARES.

- PLOTAR APENAS O ARQUIVO PDF-COLORIDO CASO CONTRÁRIO PODERÁ HAVER PERDA DE INFORMAÇÕES

05

04

03

02

01

00

REV.

DATA

DESCRIÇÃO

SIGMA

CONSULTORIA & PROJETOS

SIGMA I CONSULTORIA & PROJETOS

RUA URUGUAIANA, 10-SALA 2307- CENTRO- RIO DE JANEIRO-RJ

TEL/FAX: (55-21)2508-8541 E-MAIL: admin@sigmaeng.com.br

www.sigmaeng.com.br

ENG. EDUARDO VIDAL CABRAL CREA: 18807/0

ENG. MAURÍCIO DOS SANTOS SGARBI CREA: 20051/008

NÚMERO DA OBRA

578

RESPONSÁVEL

MAURÍCIO SGARBI

COORDENADOR

VINÍCIUS CORDEIRO

PROJETISTA

VINÍCIUS CORDEIRO

DESENHO Nº

ST 009

PROJETO

ESTRUTURA

FASE

EXECUTIVO

ESCALA

1:50

DATA

22/05/2026

ARQUIVO

PDM-EST-EX-009-PB-TIP-FORM_R

EMPRESAMENTO E LOCAL

PDM 1050

RUA PRUDENTE DE MORAIS, 1050 - IPANEMA, RIO DE JANEIRO - RJ

TÍTULO DO DESENHO

FORMA

PISO DO TIPO

(TETO DO 17º PAVIMENTO)

DIMENSÃO DA FOLHA: 1211x594mm (A1/L)