

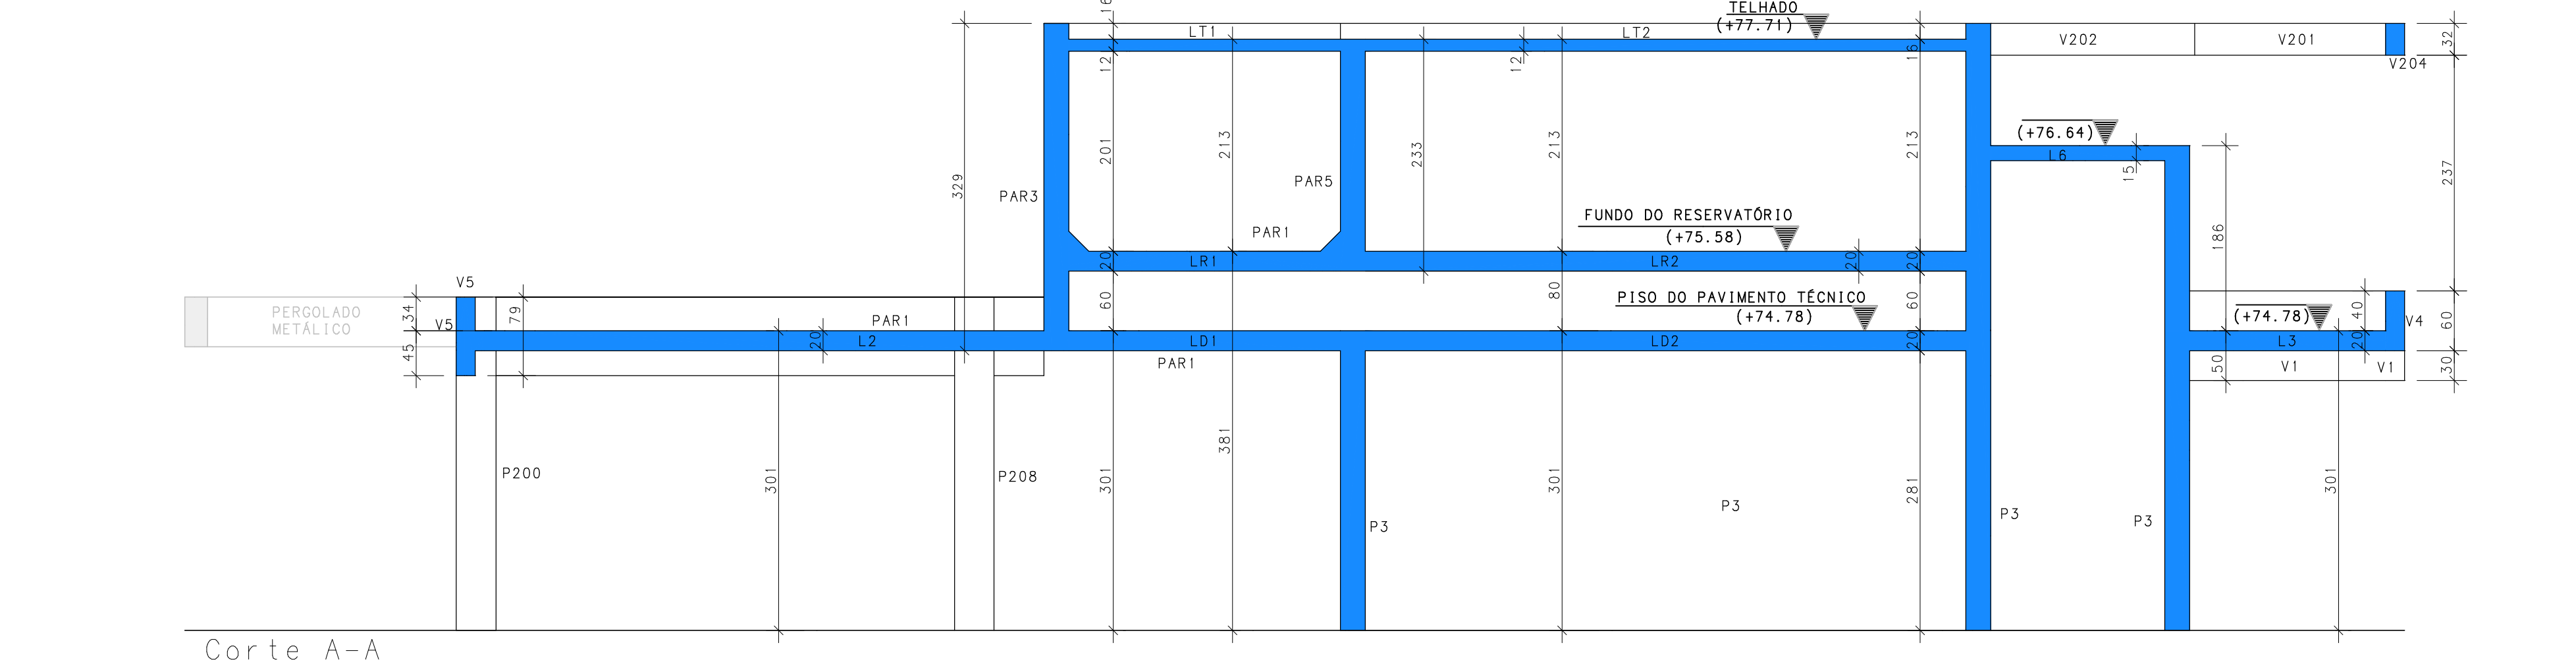
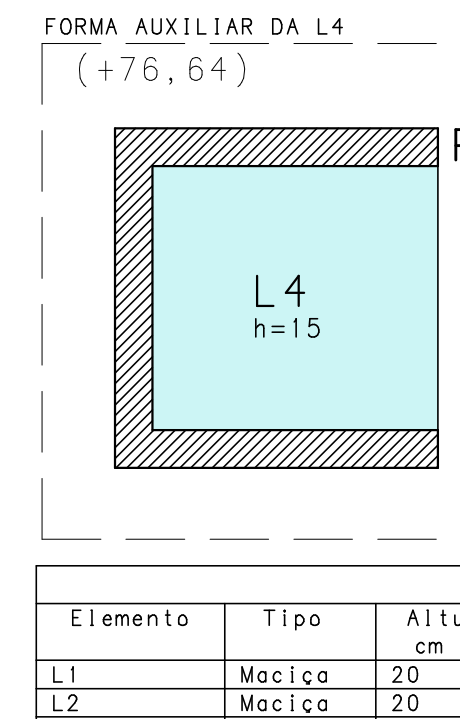


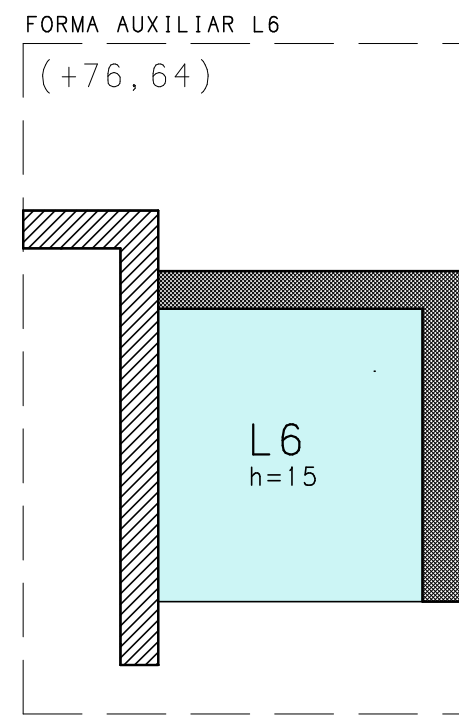

FORMA DO PAVIMENTO TÉCNICO
(+74,78)


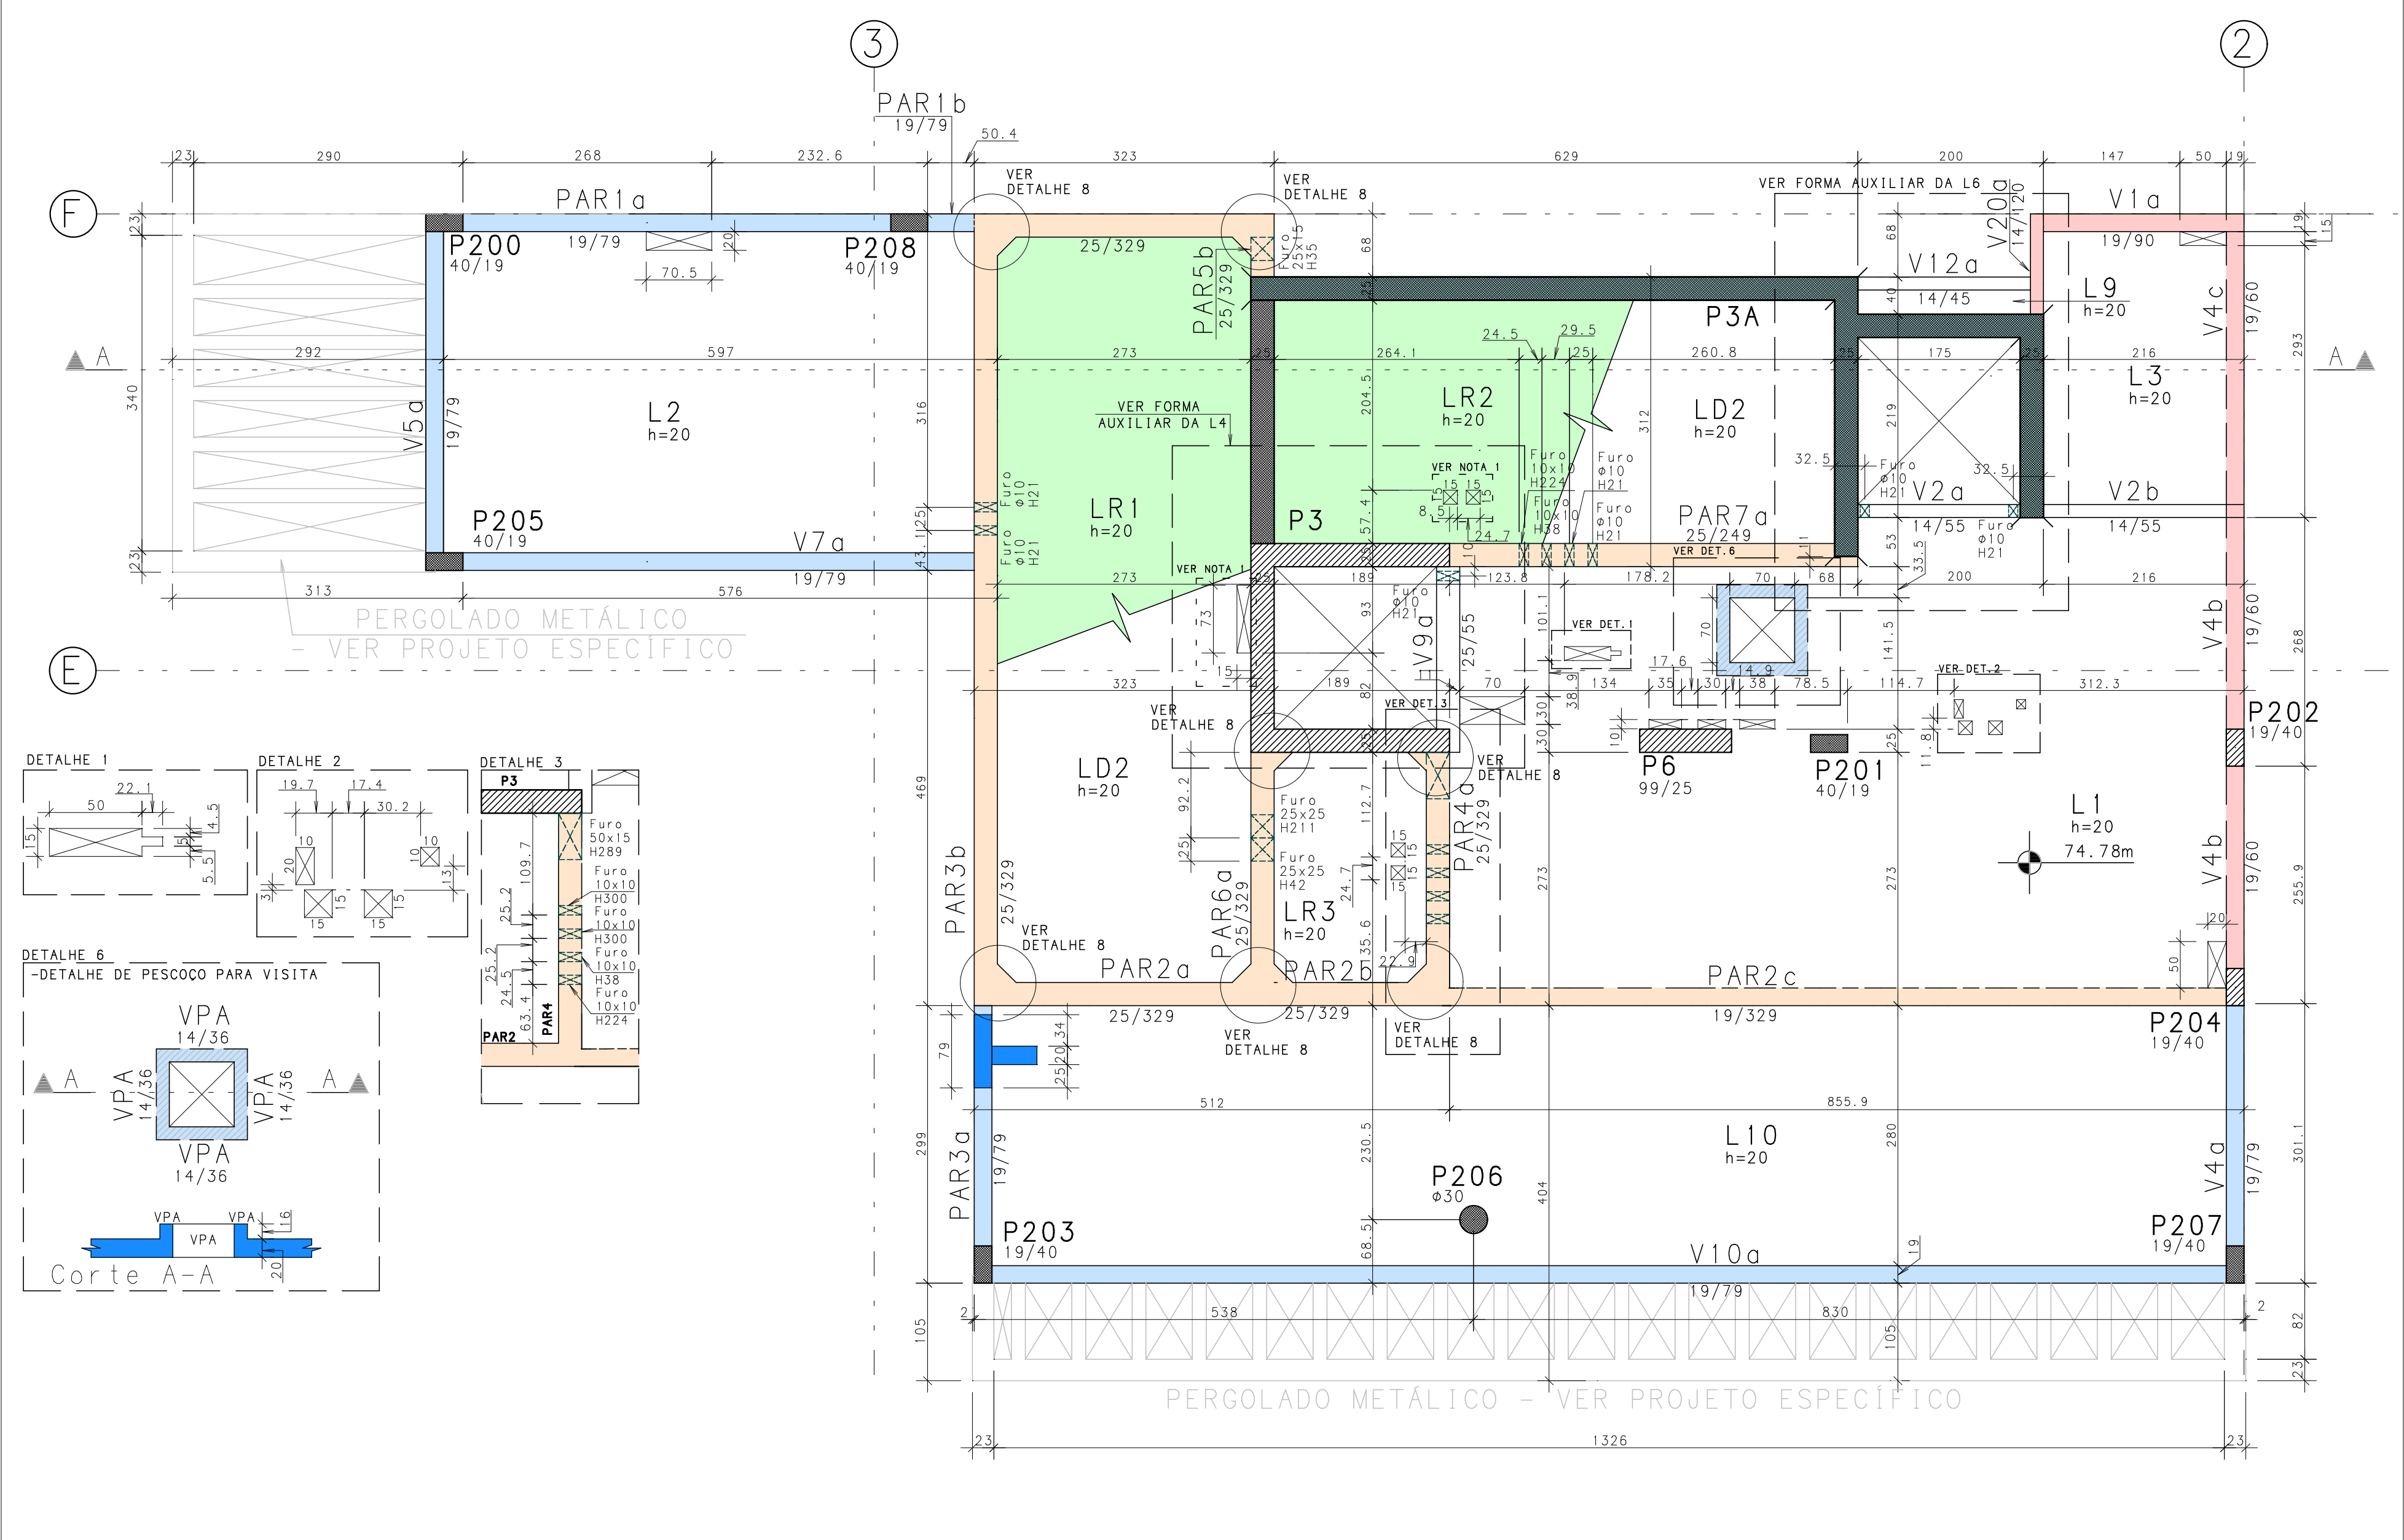


Elemento	Tipo	Altura cm	Elevação cm	PP tf/m	PERM tf/m	ACID tf/m	TOT tf/m
L1	Moldado	20	0.500	0.100	0.300	0.900	
L2	Moldado	20	0.500	0.200	0.100	0.800	
L3	Moldado	20	0.500	0.200	0.300	1.000	
L4	Moldado	20	0.500	0.200	0.300	1.000	
L5	Moldado	20	0.500	0.200	0.300	1.000	
L6	Moldado	20	0.500	0.200	0.300	1.000	
L7	Moldado	20	0.500	0.200	0.300	1.000	
L8	Moldado	20	0.500	0.200	0.300	1.000	
L9	Moldado	20	0.500	0.200	0.300	1.000	
L10	Moldado	20	0.500	0.200	0.300	1.000	
L11	Moldado	20	0.500	0.200	0.300	1.000	
L12	Moldado	20	0.500	0.200	0.300	1.000	
L13	Moldado	12	0.300	0.150	0.100	0.550	
L14	Moldado	12	0.300	0.150	0.100	0.550	

Legenda de níveis	
Cor	nível m
Ver	+74.94
Ver	+75.12
Ver	+75.18
Ver	+75.58
Ver	+76.64
Ver	+77.71
Ver	+77.87

NOTA 1: OS FURROS INDICADOS DEVEM SER EXECUTADOS SOMENTE NAS LAJES DO FUNDO DO RESERVATÓRIO.

FORMA DO TELHADO
(+77,71)

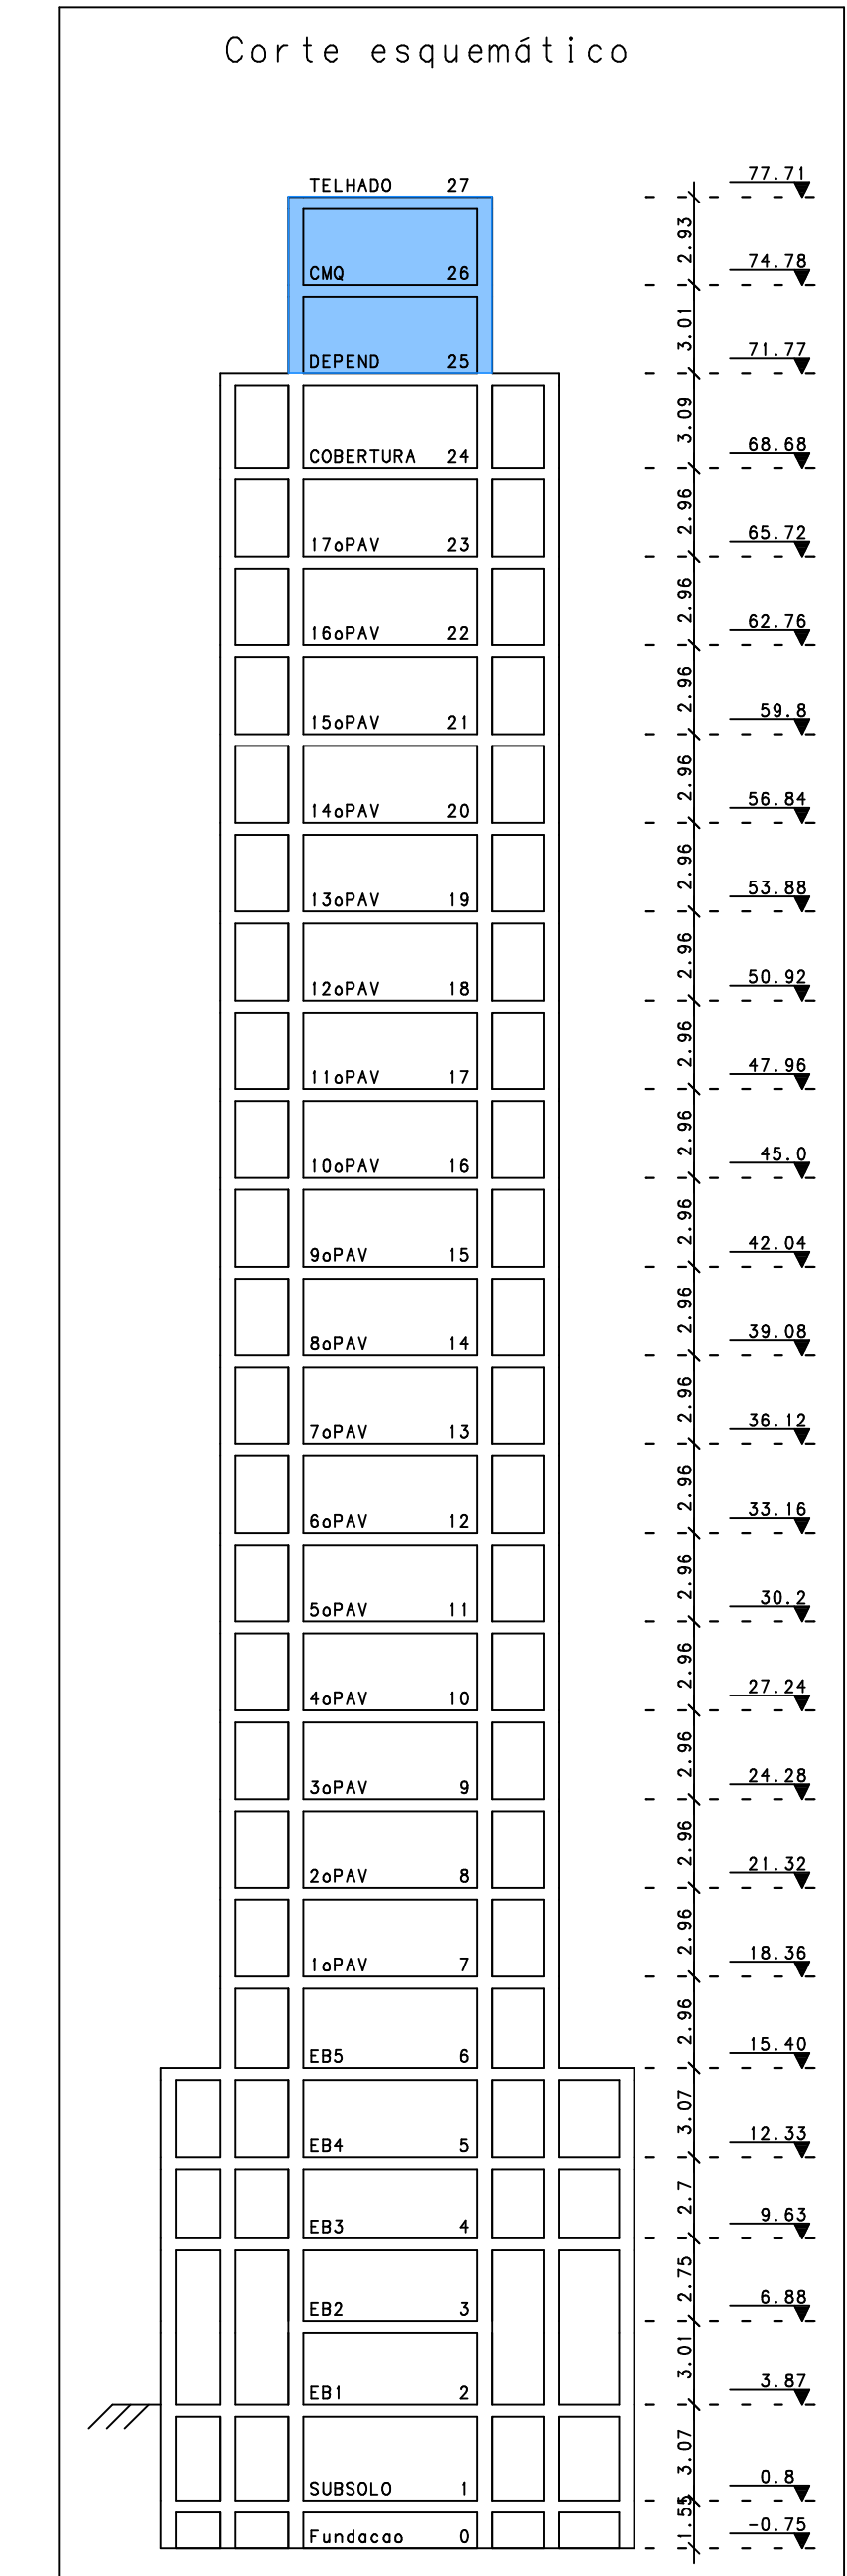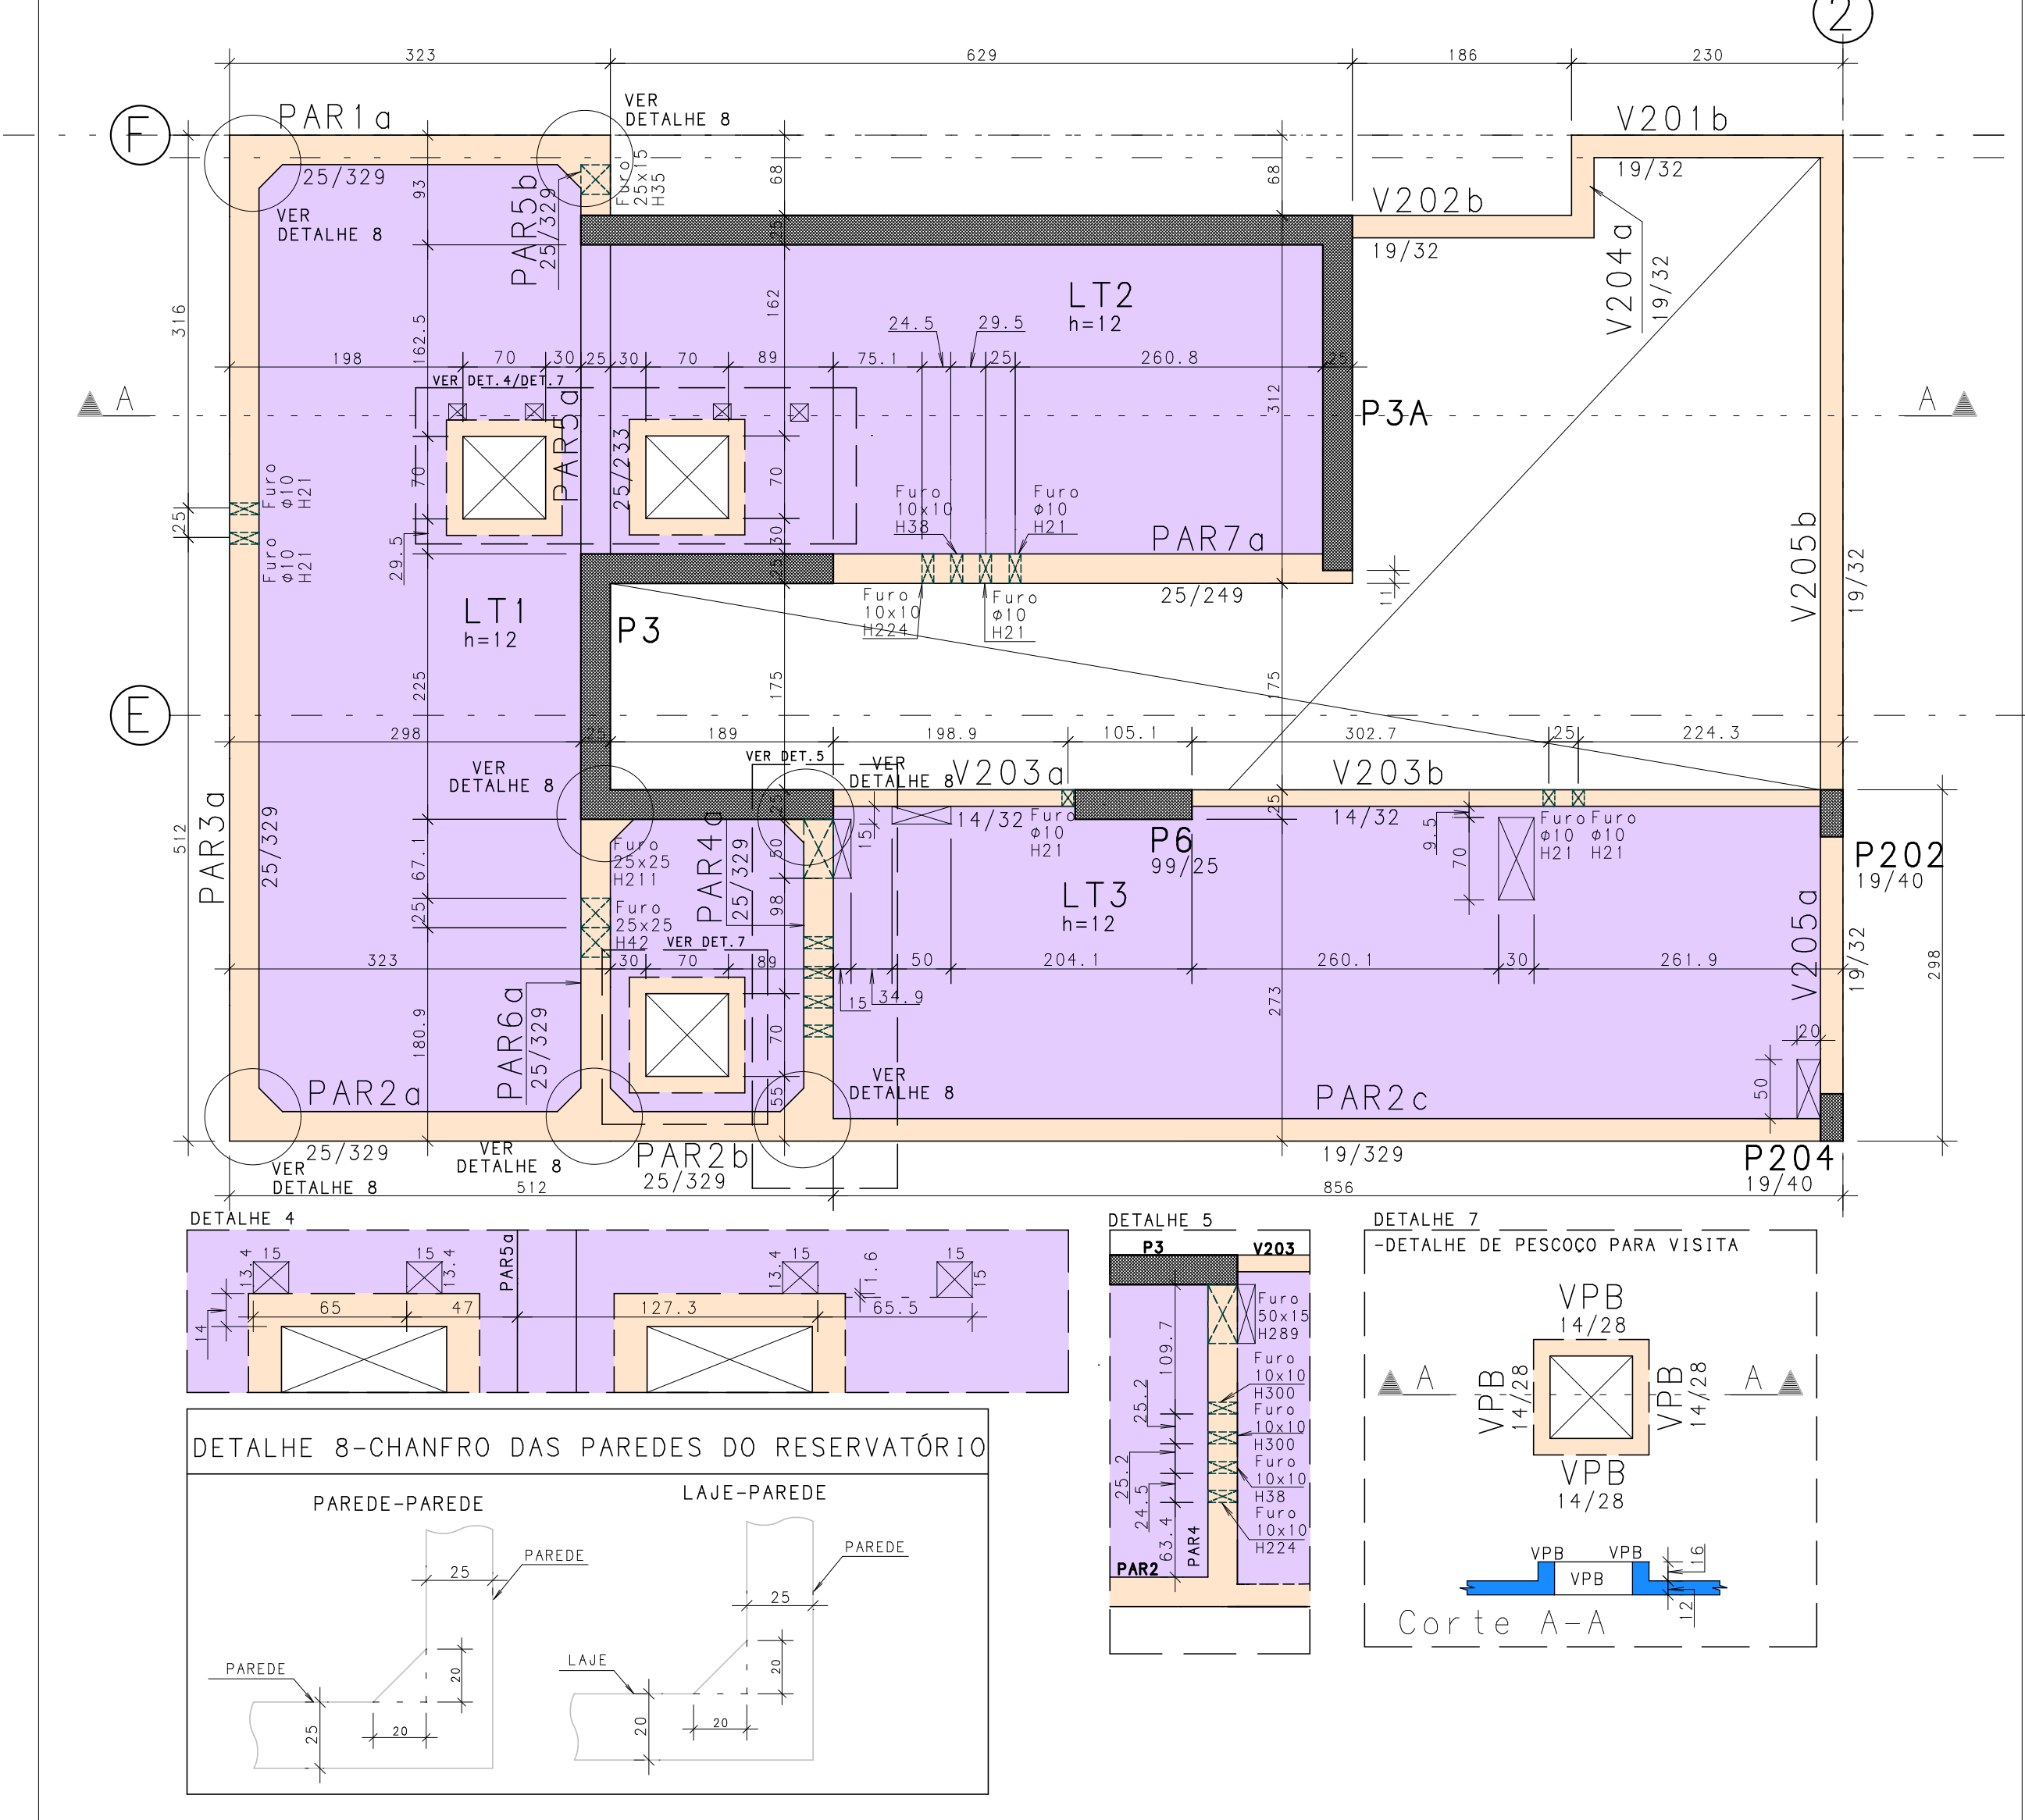

CONVENÇÃO DE PILARES			
NASCE	CONTINUA	MORRE	

NOTAS GERAIS PARA O USO DESTA PLANILHA :

A. DIREITOS AUTORAIS

ESTE PROJETO É PROPRIEDADE DE SIGMA CONSULTORIA & PROJETOS FILIADO A ASSOCIAÇÃO BRASILEIRA DE ENGENHARIA E CONSULTORIA ESTRUTURAL - ABCE, SOB O Nº. 0788, NÃO SENDO PERMITIDA SUA UTILIZAÇÃO PARA QUALQUER FINALIDADE QUE NÃO SE RELACIONE COM A EXECUÇÃO ESPECÍFICA DESTA OBRA, SENDO TERMINANTEMENTE VEDADA SUA COLOCAÇÃO À DISPOSIÇÃO DE TERCEIROS.

B. NORMAS TÉCNICAS DE REFERÊNCIA

NBR 6118 PROJETO DE ESTRUTURAS DE CONCRETO

NBR 6120 CARGAS PARA O CÁLCULO DE ESTRUTURAS DE EDIFICAÇÕES

NBR 6123 FORÇAS DEVIDAS AO VENTO EM EDIFICAÇÕES

NBR 5671 PARTICIPAÇÃO DOS INTERVENIENTES EM SERVIÇOS E OBRAS DE ENGENHARIA E ARQUITETURA

NBR 12654 CONTROLE TECNOLÓGICO DE MATERIAIS COMPONENTES DO CONCRETO

NBR 12655 CONCRETO - PREPARO, CONTROLE E RECEBIMENTO

NBR 5738 MOLDAGEM E CURA DE CORPOS CILÍNDRICOS OU PRIS MATICOS DE CONCRETO - MÉTODO DE ENSAIO

NBR 5739 CONCRETO - ENSAIO DE COMPRESSÃO DE CORPOS-DE-PROVA CILÍNDRICOS - MÉTODO DE ENSAIO

NBR 8522 CONCRETO - DETERMINAÇÃO DO MÓDULO DE DEFORMAÇÃO ELÁSTICA E DIAGRAMA TENSÃO x DEFORMAÇÃO - MÉTODO DE ENSAIO

NBR 6152 MATERIAIS METÁLICOS-DETERMINAÇÃO DAS PROPRIEDADES MECÂNICAS A TRAÇÃO-MÉTODO DE ENSAIO

NBR 6153 PRODUTO METÁLICO - ENSAIO DE DOBRAMENTO SEMI-GUIDADO

NBR 7477 DETERMINAÇÃO DO DEFICIÊNCIA DE CONFORMAÇÃO SUPERFICIAL DE BARRAS E FIOS DE AÇO DESTINADOS A ARMADURA DE CONCRETO ARMADO MÉTODO DE ENSAIO

NBR 7480 BARRAS E FIOS DE AÇO DESTINADOS A ARMADURAS PARA CONCRETO ARMADO - ESPECIFICAÇÃO

C. GEOMETRIA

OS ELEMENTOS DE CONFORMIDADE DO PROJETO ESTRUTURAL FACE AOS PROJETOS DE ARQUITETURA, INSTALAÇÕES E DEMAIS DISCIPLINAS TAIS COMO COTAS, NÍVEIS, DIMENSÕES DAS PEÇAS ESTRUTURAIS, POÇOS DE ELEVADORES, ESCADAS, ETC. DEVEM SER VALIDADOS PELOS ARQUITETOS RESPONSÁVEIS PELO DESENVOLVIMENTO DO PROJETO EXECUTIVO.

D. MATERIAIS

01. CONCRETO

VER EM NOTAS GERAIS

02. AÇO EM ARMADURA PASSIVA

02.1. AÇO CA-50A / CA-60B

03. FORMAS E ESCORAMENTOS

O PROJETO E DIMENSIONAMENTO DAS FORMAS E ESCORAMENTOS NÃO FAZ PARTE DO ESCOPO DE Nossos SERVIÇOS.

E. EXECUÇÃO DA ESTRUTURA

A EXECUÇÃO DA ESTRUTURA E DE RESPONSABILIDADE DA EMPRESA CONSTRUTORA E DEVERÁ CONTAR COM A CONSULTORIA DE UM TECNOLÓGICO DE MATERIAIS. O ENGENHEIRO RESPONSÁVEL PELA EXECUÇÃO DEVERÁ OBEDECER AS RECOMENDAÇÕES DA NBR 6118-EXECUÇÃO DE ESTRUTURAS DE CONCRETO-PROCEDIMENTOS.

F. CARGAS ADOPTADAS PARA ESTE PROJETO

01. FORÇAS DEVIDAS AO VENTO : CONFORME NBR 6123

02. CARGAS ACIDENTAIS NÃO PARTICULARES : CONFORME NBR 6120 DE ACORDO COM PROJETO ARQUITETÔNICO

APROVADO EM PREFEITURA

03. PESO PRÓPRIO DO CONCRETO : 2500 kgf / m³

04. ALVENARIAS (COM REVESTIMENTOS) : 1500 kgf / m³

+ ESPESURA DA ALVENARIA ACABADA CONFORME PROJ. ARQUITETÔNICO

05. LAJES (CONTRAPISO + REVESTIMENTOS) : 100 kgf / m²

06. AS CARGAS EVENTUALMENTE INFORMADAS NAS PRANCHAS DE FORMAS PREVALECEM SOBRE AS CARGAS AQUI INDICADAS.

G. COBERTIMENTOS

01. LAJES: POSITIVA/NEGATIVA 2.0/1.5 cm 2.0/2.0 cm

02. VIGAS: 2.5 cm 2.5 cm

03. PILARES: 3.0 cm 3.0 cm

04. BLOCOS SOBRE ESTACAS / SAPATAS: 3.0 cm

05. CINTAS / LAJES DE SUPRESSÃO: 3.0 cm

06. PAREDES DE SUBSOLO: 3.0 cm

07. RESERVATÓRIOS: 3.0 cm

OBS: 1) DEVERÁ HAVER CONTROLE RIGOROSO DE QUALIDADE E RÍGIDOS LIMITES DE TOLERÂNCIA DAS MEDIDAS DURANTE A EXECUÇÃO.

2) COBERTIMENTOS INFORMADOS NOS DESENHOS DE ARMADURA PREVALECEM EM RELAÇÃO À TABELA ACIMA.

H. MEMORIAL DESCRITIVO PARA DESCRIMBAMENTO DA ESTRUTURA

(PAR DESENVOLVIMENTO DA RESISTÊNCIA DO CONCRETO)

ATENDENDO AS EXPECTATIVAS DE VALORES A 7, 14, 21 E 28 DIAS)

TEMPO DECORRIDO APÓS A CONCRETAGEM (DIAS)

1. FUNDAMENTOS

01. O PROJETO DE FUNDAMENTOS, DETERMINAÇÃO DA TAXA ADMISSÍVEL NO TERRENO, DISPOSIÇÃO E DIMENSIONAMENTO DE ESTACAS, COTA DE IMPLANTAÇÃO, METODOLOGIA DE ESCAVAÇÃO, INTERAÇÃO COM VIZINHOS, ETC., É DE RESPONSABILIDADE DA EMPRESA DE CONSULTORIA DE FUNDAMENTOS DEVENDO SEGUIR AS RECOMENDAÇÕES DA NBR 6122 - PROJETO E EXECUÇÃO DE FUNDAMENTOS

J. FURAÇÕES

01. FURROS EM LAJES E VIGAS DEVERÃO RECEBER ARMADURA DE REFORÇO PADRÃO.

02. FURROS NÃO INDICADOS SÃO PODERÃO SER EXECUTADOS COM NOSSA APROVAÇÃO.

NOTAS GERAIS

1- DIMENSÕES EM CENTÍMETRO. NÍVEIS EM METRO

2- PROPRIEDADES DO CONCRETO

-Fck > 40 MPa (400kg/cm²)

-MÓDULO DE DEFORMAÇÃO TANGENTE INICIAL > 32 GPa

-CONSUMO MÍNIMO DE CIMENTO: 350kg/m³

-FATOR ÁGUA/CEMENTO MÁXIMO: 0,55

3- UTILIZAR OBRIGATORIAMENTE EM CONJUNTO COM O DESENHO DE FURAÇÃO

ATENÇÃO/PLOTAGEM

OS ARQUIVOS DXF SERVEM APENAS COMO BASE PARA A ARQUITETURA E DEMAIS COMPLEMENTARES.

PLOTAR APENAS O ARQUIVO PDF-COLORIDO CASO CONTRÁRIO PODERÁ HAVER PERDA DE INFORMAÇÕES

10			
09			
08			
07			
06	17/08/2026	CONFORME COMENTÁRIOS DA ARQUITETURA	
05	06/01/2025	EMIÇÃO INICIAL	
REV.	DATA	DESCRIÇÃO	

	SIGMA CONSULTORIA & PROJETOS RUA URUGUAIANA, 10-SALA 2307- CENTRO- RIO DE JANEIRO-RJ TEL/FAX: (55-21)2508-8541 E-MAIL: admin@sigmaengbr www.sigmaengbr	NÚMERO DA OBRA 578
CONSTRUTOR VINÍCIUS CORDEIRO	RESPONSÁVEL MAURÍCIO SGARBI	
PROJETISTA VINÍCIUS CORDEIRO		
DESENHO Nº ST 012		
EMPREENHIMENTO E LOCAL PDM 1050 RUA PRUDENTE DE MORAIS, 1050 - IPANEMA, RIO DE JANEIRO - RJ	TÍTULO DO DESENHO FORMA PISO DO PAV. TÉCNICO E TELHADO (TETO DO EMBASAMENTO 2)	PROJETO ESTRUTURA FASE EXECUTIVO ESCALA 1:50 DATA 17/08/2026 ARQUIVO PDM-EST-EX-012-PB-TEL-FORM-R6

DIMENSÃO DA FOLHA: 1211x594mm (A1/L)