


33004 - 1 - CONSULTORIA & PROJETOS DE 22/05/2026 13:41:39

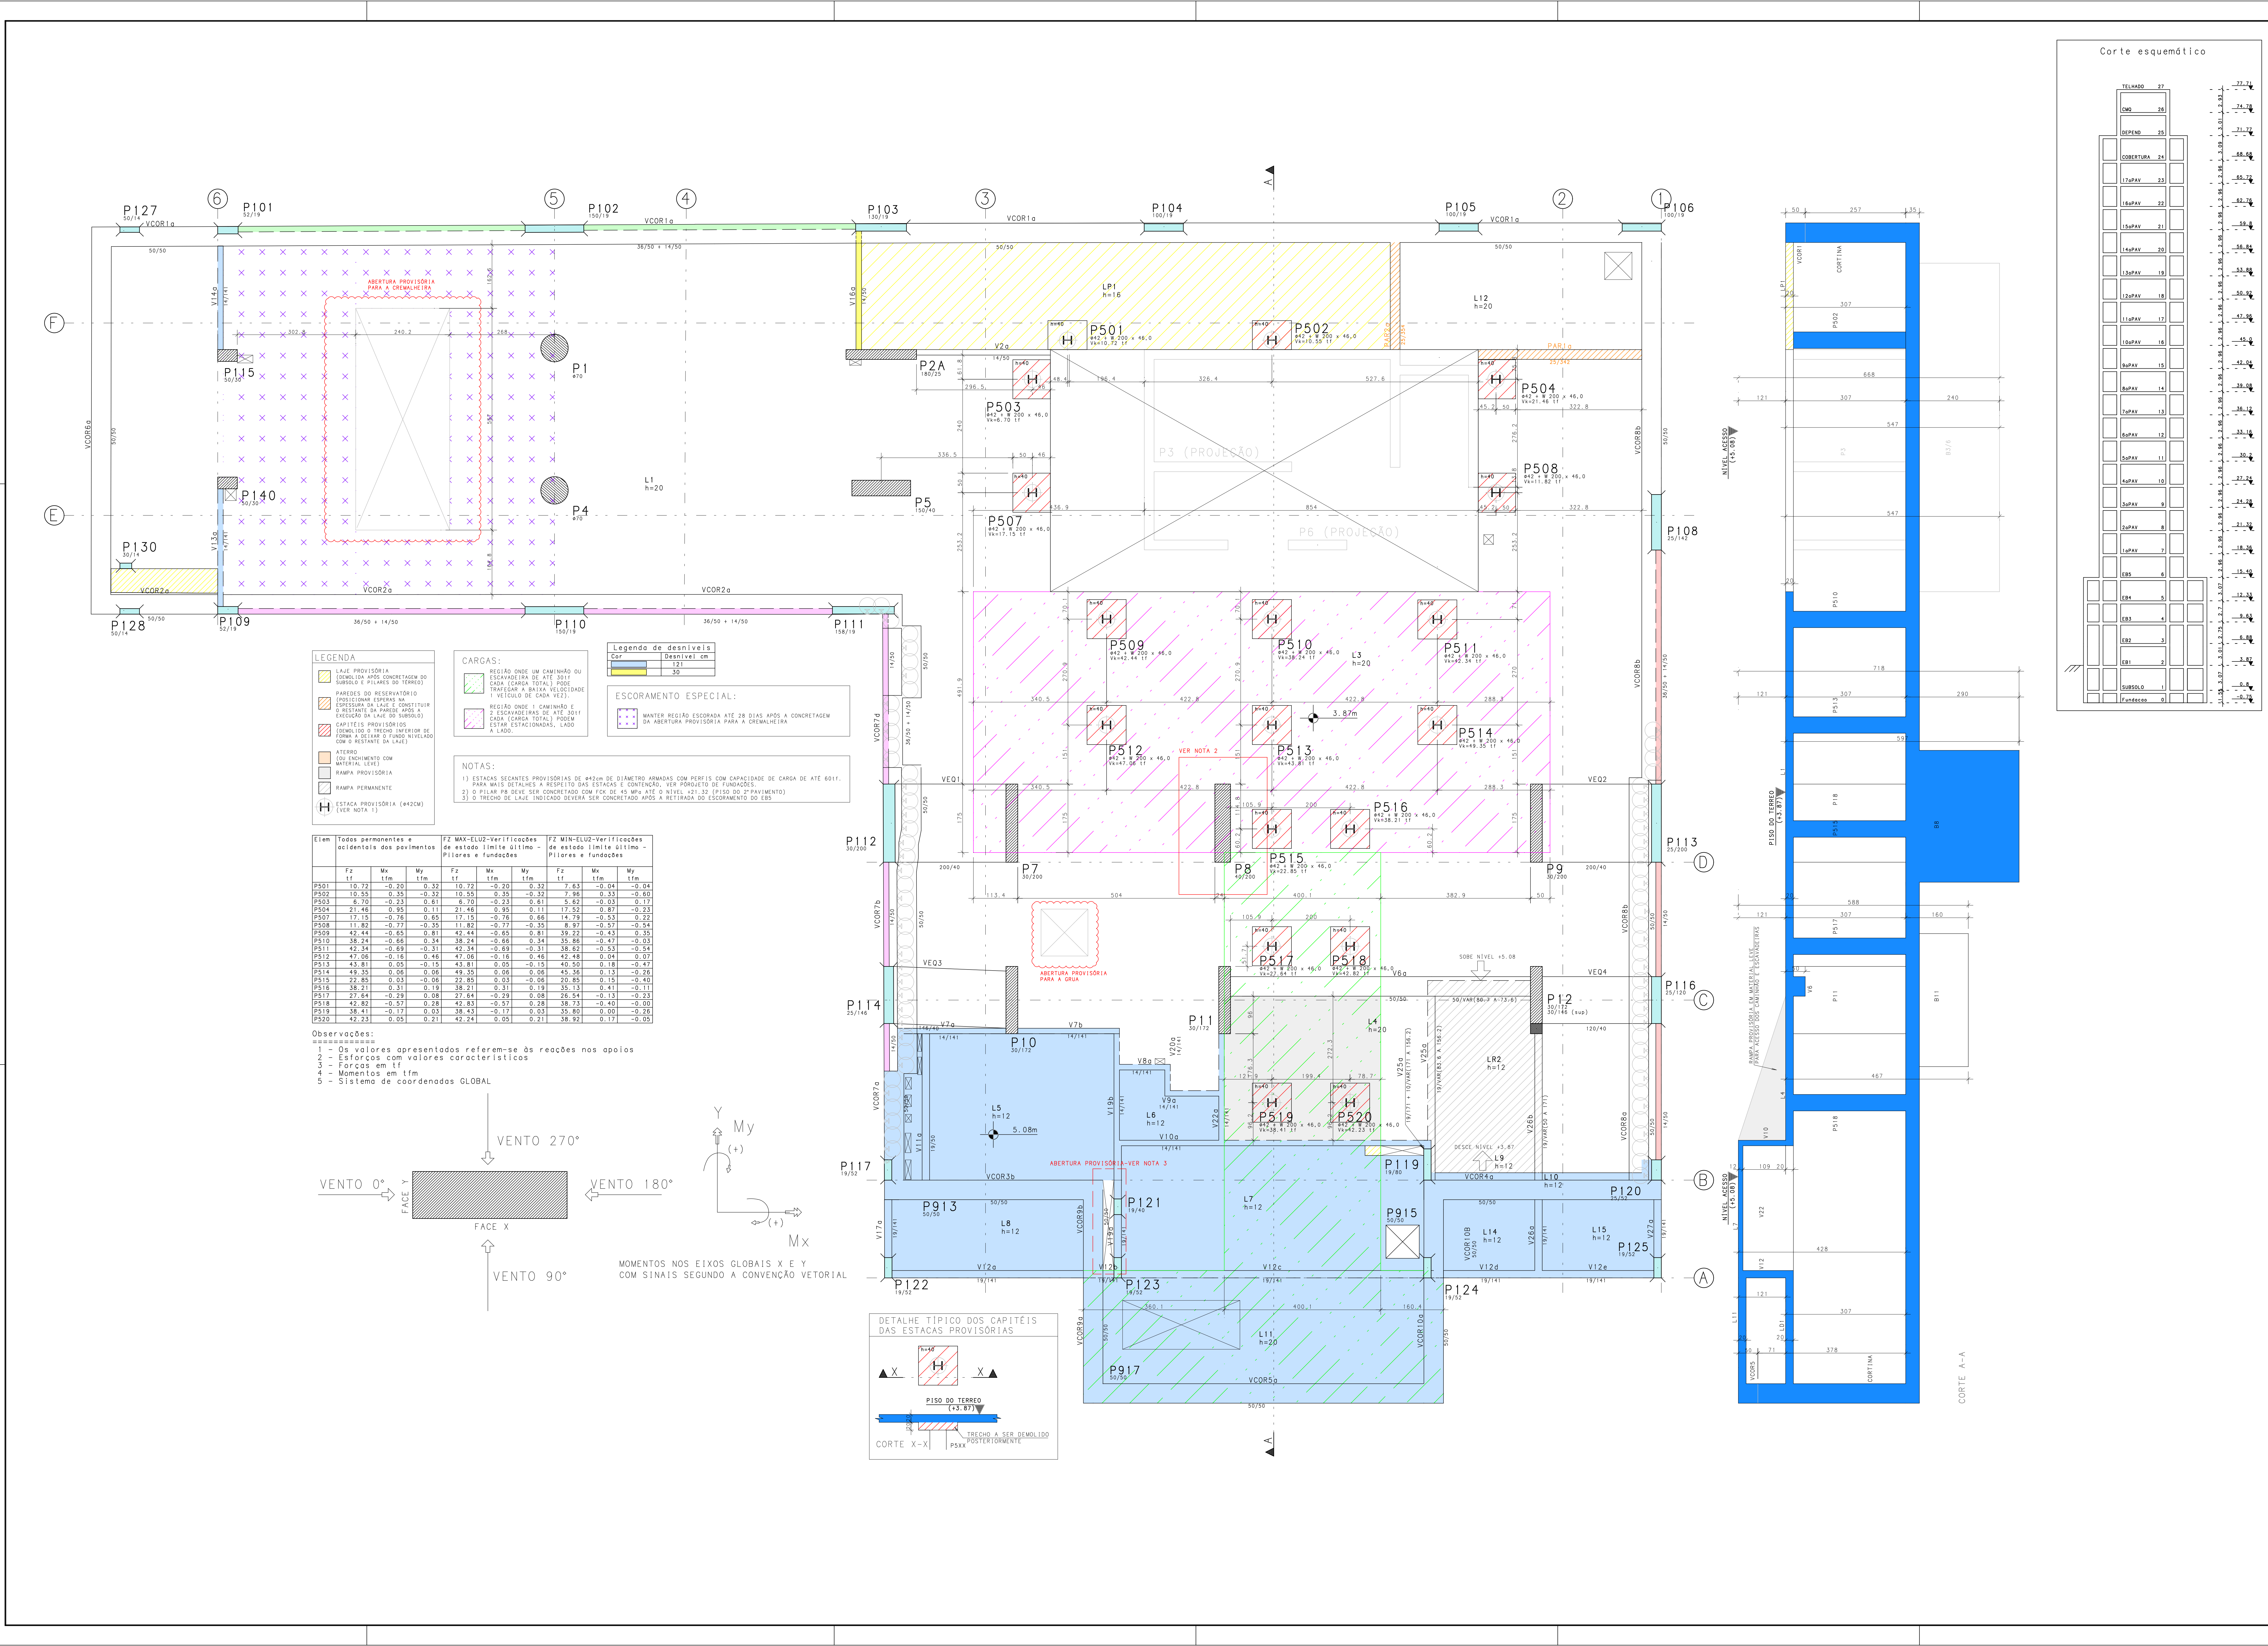

NOTAS GERAIS PARA O USO DESTA PROJETO:

A. DIREITOS AUTORAIS

ESTE PROJETO É PROPRIEDADE DE SIGMA1 CONSULTORIA & PROJETOS. FICANDO A ASSOCIAÇÃO BRASILEIRA DE ENGENHARIA E CONSULTORIA ESTRUTURAL - ABRECE, E O SEU CORPO TÉCNICO, DESLIGADOS DE QUALQUER RESPONSABILIDADE QUE NÃO SE RELACIONE COM A EXECUÇÃO ESPECÍFICA DESTA OBRA, SENDO TERMINANTEMENTE VÁLIDA SUA COLUOÇÃO A DISPOSIÇÃO DO TERCEIROS.

B. NORMAS TÉCNICAS DE REFERÊNCIA

NBR 6118

PROJETO DE ESTRUTURAS DE CONCRETO

NBR 6120

CARGAS PARA O CÁLCULO DE ESTRUTURAS DE EDIFICAÇÕES

NBR 6123

FORÇAS DEVIDAS AO VENTO EM EDIFICAÇÕES

NBR 6471

PARTICIPAÇÃO DOS INTERVENIENTES DE SERVIÇOS E OBRAS DE ENGENHARIA E ARQUITETURA

NBR 7264

CONTROLE TECNOLÓGICO DE MATERIAIS COMPONENTES DO CONCRETO

NBR 7265

CONCRETO - PREPARO, CONTROLE E RECEBIMENTO

NBR 7338

MOLDEADO E CURA DE CORPOS CULTURADOS DE MATERIAIS DE CONCRETO - MÉTODO DE ENSAIO

NBR 7339

CONCRETO - ENSAIO DE COMPRESSÃO DE CORPOS-DE-PROVA CILINDRICOS - MÉTODO DE ENSAIO

NBR 8522

CONCRETO - DETERMINAÇÃO DO MÓDULO DE DEFORMAÇÃO ELÁSTICA E DILATAMEN TO ENFRA - MÉTODO DE ENSAIO

NBR 6152

MATERIAIS METÁLICOS - DETERMINAÇÃO DAS PROPRIEDADES MECÂNICAS À TRACÇÃO - MÉTODO DE ENSAIO

NBR 6153

PRODUTO METÁLICO - ENSAIO DE DOBRAMENTO SEMI-GUIADO

NBR 7477

DETERMINAÇÃO DO COEFICIENTE DE CONFORMAÇÃO SUPERFICIAL DE BARRAS E FIOS DE AÇO DESTINADOS A ARMADURA DE CONCRETO ARMADO - MÉTODO DE ENSAIO

NBR 7480

BARRAS E FIOS DE AÇO DESTINADOS A ARMADURAS PARA CONCRETO ARMADO - ESPECIFICAÇÃO

C. GEOMETRIA

OS ELEMENTOS DE CONFORMIDADE DO PROJETO ESTRUTURAL, FACE OS PROJETOS DE ARQUITETURA, INSTALAÇÕES E DEMAIS DISCIPLINAS, TAIS COMO COTAS, NÍVEIS, DIMENSÕES DAS PEÇAS ESTRUTURAIS, POSIÇÃO DE ELEVADORES, ESCADAS, ETC., DEVEM SER VALIDADOS PELOS ARQUITETOS RESPONSÁVEIS PELO DESENVOLVIMENTO DO PROJETO EXECUTIVO.

D. MATERIAIS

01. CONCRETO

VER EM NOTAS GERAIS

02. AÇO EM ARMADURA PASSIVA

02.1. AÇO CA-50A / CA-60B

03. FORMAS E ESCORAMENTOS

03.1. O PROJETO E DIMENSIONAMENTO DAS FORMAS E ESCORAMENTOS NÃO FAZ PARTE DO ESCOPO DE Nossos SERVIÇOS.

E. EXECUÇÃO DA ESTRUTURA

A EXECUÇÃO DA ESTRUTURA E DE RESPONSABILIDADE DA EMPRESA CONSTRUTORA E DEVERÁ CONTAR COM A CONSULTORIA DE UM ESPECIALISTA DE MATERIAIS E O ENGENHEIRO RESPONSÁVEL PELA EXECUÇÃO DEVERÁ OBEDECER AS RECOMENDAÇÕES DA NBR-6118-EXECUÇÃO DE ESTRUTURAS DE CONCRETO-PROCEDIMENTOS

F. CARGAS APLICADAS PARA ESTE PROJETO

01. CARGAS RESIDUAIS NÃO PARTICULARES - CONFORME NBR 6120

02. CARGAS RESIDUAIS PARTICULARES - CONFORME NBR 6120

03. CARGAS DE ACORDO COM PROJETO ARQUITETÔNICO APROVADA EM PREFEITURA

04. ALVENARIAS (COM REVESTIMENTOS) : 1,500 kgf / m²

05. LAJES (CONTRAPISO + REVESTIMENTOS) : 1,100 kgf / m²

06. AS CARGAS EVENTUALMENTE INFORMADAS NAS PRANCHAS DE FORMAS PREVALECEM SOBRE AS CARGAS AQUI INDICADAS.

G. COBRIMENTOS

01. LAJES: POSITIVANEGATIVA

02. VIGAS:

03. PILARES:

04. BLOCOS SOBRE ESCADAS / SAPATAS:

05. CINTAS / LAJES DE SUPRESSÃO:

06. PARQUES DE SUBSÓLO:

07. RESERVAÇÕES:

08.1) DEVERÁ HAVER CONTROLE RIGOROSO DE QUALIDADE E RÍGIDOS LIMITES DE TOLERÂNCIA DAS MEDIDAS DURANTE A EXECUÇÃO.

08.2) COBRIMENTOS INFORMADOS NOS DESENHOS DE ARMADURA PREVALECEM EM RELAÇÃO À TABELA ABAIXA.

H. MEMORIAL DESCRITIVO PARA DESCRIMENAMENTO DA ESTRUTURA

ATENÇÃO AS EXPECTATIVAS DE VALORES A 7, 14, 21 E 28 DIAS

TEMPO DECORRIDO APÓS A CONCRETAGEM (DIAS)

1. FUNDAMENTOS

01. O PROJETO DE FUNDAMENTOS, DETERMINAÇÃO DA TAXA ADMISSÍVEL NO TERRENO, DISPOSIÇÃO E DIMENSIONAMENTO DE ESTACAS, COTA DE IMPLANTADO, METODOLOGIA DE ESCAVACAO, INTERAÇÃO COM VIZINHOS, ETC., É DE RESPONSABILIDADE DA EMPRESA DE CONSULTORIA DE FUNDAMENTOS, DEVENDO SEGUIR AS RECOMENDAÇÕES DA NBR-6122 - PROJETO E EXECUÇÃO DE FUNDAMENTOS

2. FUNDAMENTOS

01. FUNDOS EM LAJES E VIGAS DEVERÃO RECEBER ARMADURA DE REFORÇO PADRÃO.

02. FUNDOS NÃO INDICADOS SÓ PODERÃO SER EXECUTADOS COM NOSSA APROVAÇÃO.

CONVENÇÃO DE PILARES

NASCE

CONTINUA

MORRE

NOTAS GERAIS

1- DIMENSÕES EM CENTÍMETRO, NÍVEIS EM METRO

2- PROPRIEDADES DO CONCRETO:

- $f_{ck} > 40$ MPa (400 kg / cm²)

- MÓDULO DE DEFORMAÇÃO TANGENTE INICIAL > 26 GPa

- CONSUMO MÍNIMO DE CIMENTO: 310 kg / m³

- FATOR AGUA/CIMENTO MÁXIMO: 0,55

3- UTILIZAR OBRIGATORIAMENTE EM CONJUNTO COM O DESENHO DE FURAÇÃO

ATENÇÃO/PLOTAGEM

OS ARQUIVOS DXF SERVEEM APENAS COMO BASE PARA A ARQUITETURA E DEMAIS COMPLEMENTARES. PLOTAR APENAS O ARQUIVO PDF - COLORIDO CASO CONTRÁRIO PODERÁ HAVER PERDA DE INFORMAÇÕES

05

04 22/05/2026 AJUSTADA POSIÇÃO DE ABERTURA DA GRUA

03 13/02/2026 INCLUIDOS CAPITEIS, ABERTURAS, DETALHES E NOTAS

02 07/10/2025 RETIRADOS P505 E P506

01 18/06/2025 REVISÃO GERAL

00 13/01/2025 EMISSÃO INICIAL

REV. | DATA | DESCRIÇÃO

SIGMA1

CONSULTORIA & PROJETOS

RUA JOAQUIM FAGUNDA, 72 - SALAS 1108/1107 - JARDIM NITERÓI/RJ
TEL/FAX: (51) 212208-5041 E-MAIL: contato@sigma1projeto.com.br

ENG. RAFAEL RODRIGUES LOPES CREA: 2013107841
ENG. MAURICIO DOS SANTOS SCARBI CREA: 200810608

578
SUFIXO: MAURICIO SCARBI
CORPORE: VENTÍCIUS CORDEIRO
PROFESSOR: VENTÍCIUS C.

SIG

EPHILUM

DESENHO DE: ST
ESTRUTURA: 013

PROJETO: PDM 1050
RUA PRUDENTE DE MORAIS, 1050 - IPANEMA, RIO DE JANEIRO - RJ

TIPO DE OBRA: FORMAS E PLANTA DE CARGAS
ETAPA CONSTRUTIVA: PISO DO TERREO (EB1)

1/50
DATA: 22/05/2026
ARQUIVO: PDM-EST-02-02-78-EB1-2026.dwg

DIMENSÃO DA FOLHA: 137x841mm (A0)