


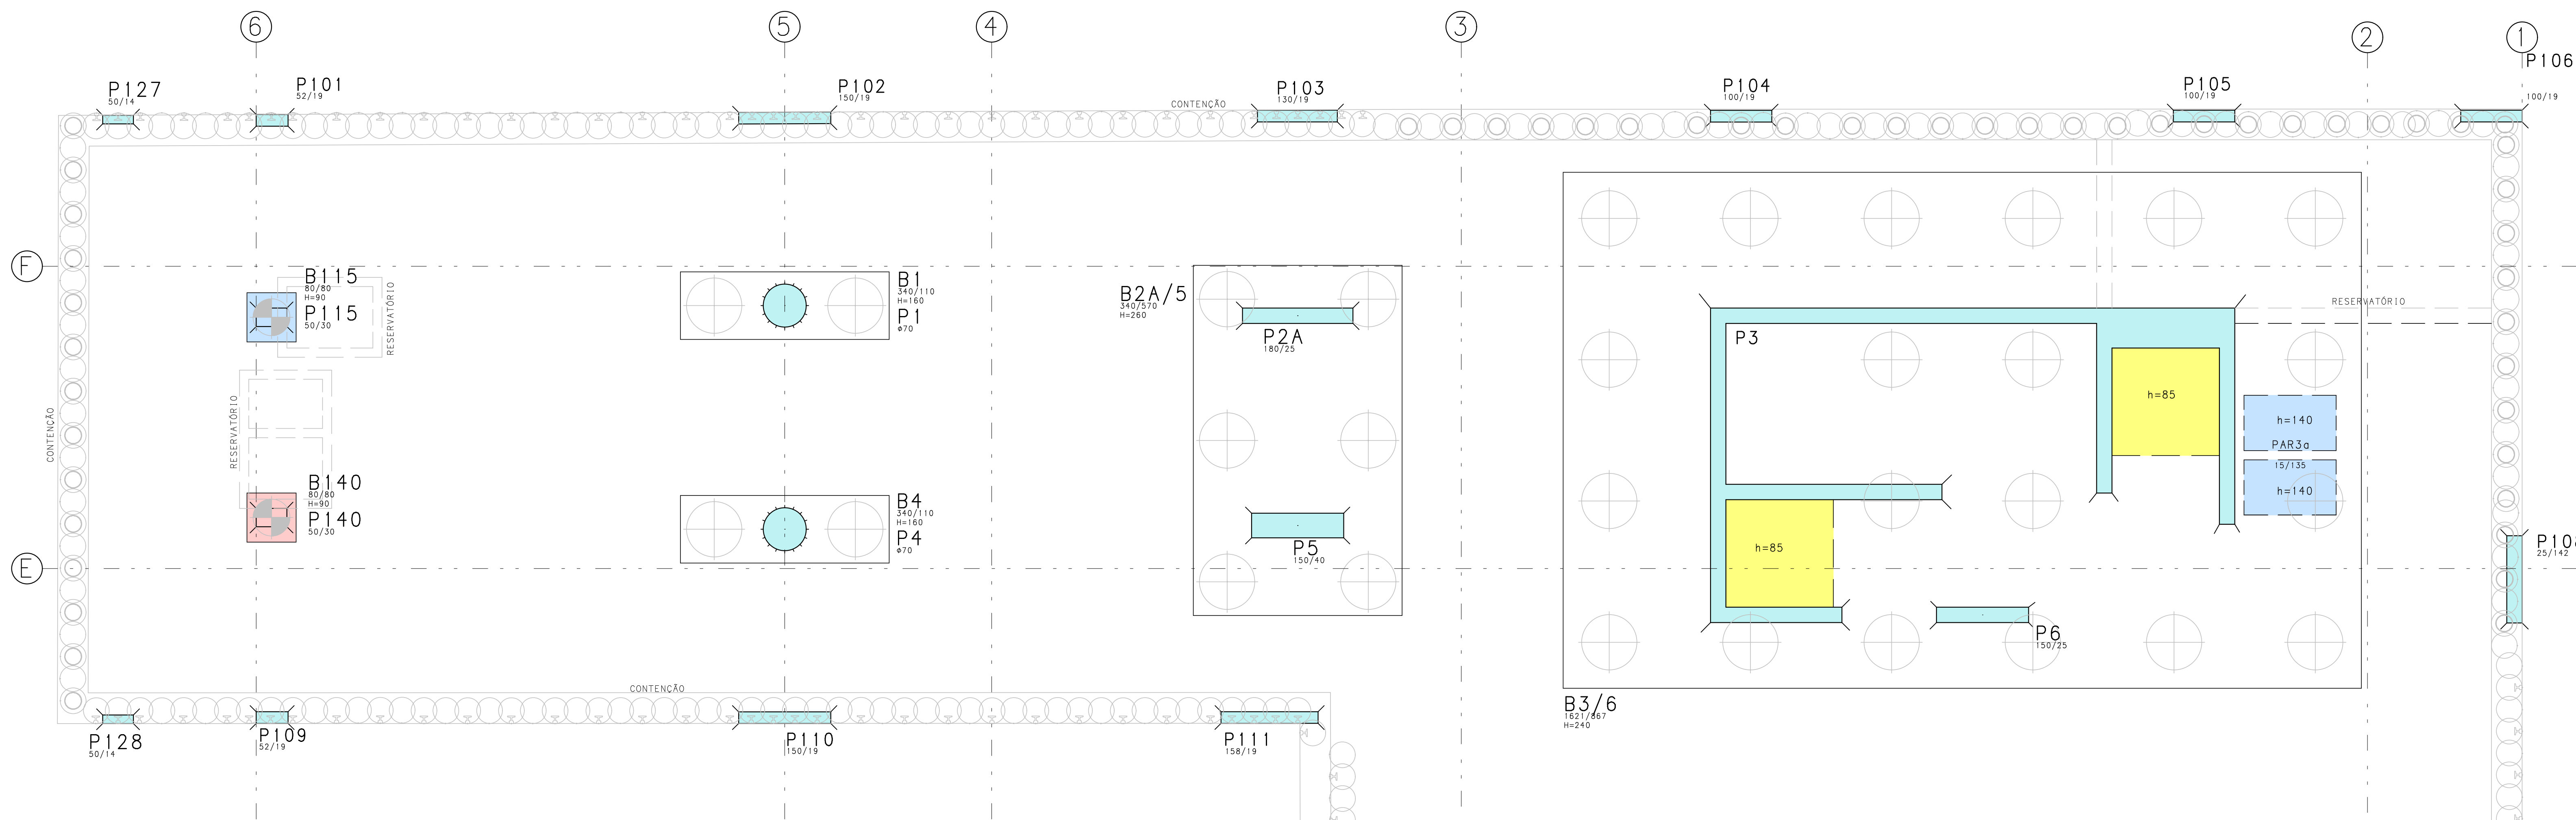










NOTAS:
1) O PILAR P8 DEVE SER CONCRETADO COM FCK DE 45 MPa ATÉ O NÍVEL +21.32 (PISO DO 2º PAVIMENTO)
2) PILARES P101 A P106, P108 A P114, P116, P117, P120, P127 E P128 NASCEM NO TOPO DA VIGA DE COROAMENTO. PARA SEÇÃO E NÍVEL DA VIGA DE COROAMENTO, VER FORMA DO TERREO (EB1)

LEGENDA DE DESNÍVEIS

1) PARA BLOCOS NÃO HACHURADOS:
□ COTA SUPERIOR (TOPO): +0.80 (NO NÍVEL DO PISO DO SUBSOLO)

2) PARA BLOCOS HACHURADOS:
■ COTA SUPERIOR (TOPO): -0.75 (155cm ABAIXO DO NÍVEL DO PISO DO SUBSOLO)
■ COTA SUPERIOR (TOPO): -0.35 (115cm ABAIXO DO NÍVEL DO PISO DO SUBSOLO)
■ COTA SUPERIOR (TOPO): -0.20 (100cm ABAIXO DO NÍVEL DO PISO DO SUBSOLO)

3) PARA SAPATAS HACHURADAS:
■ COTA SUPERIOR (TOPO): +5.08 (NO NÍVEL DO ACESSO DO PISO DO TERREO)

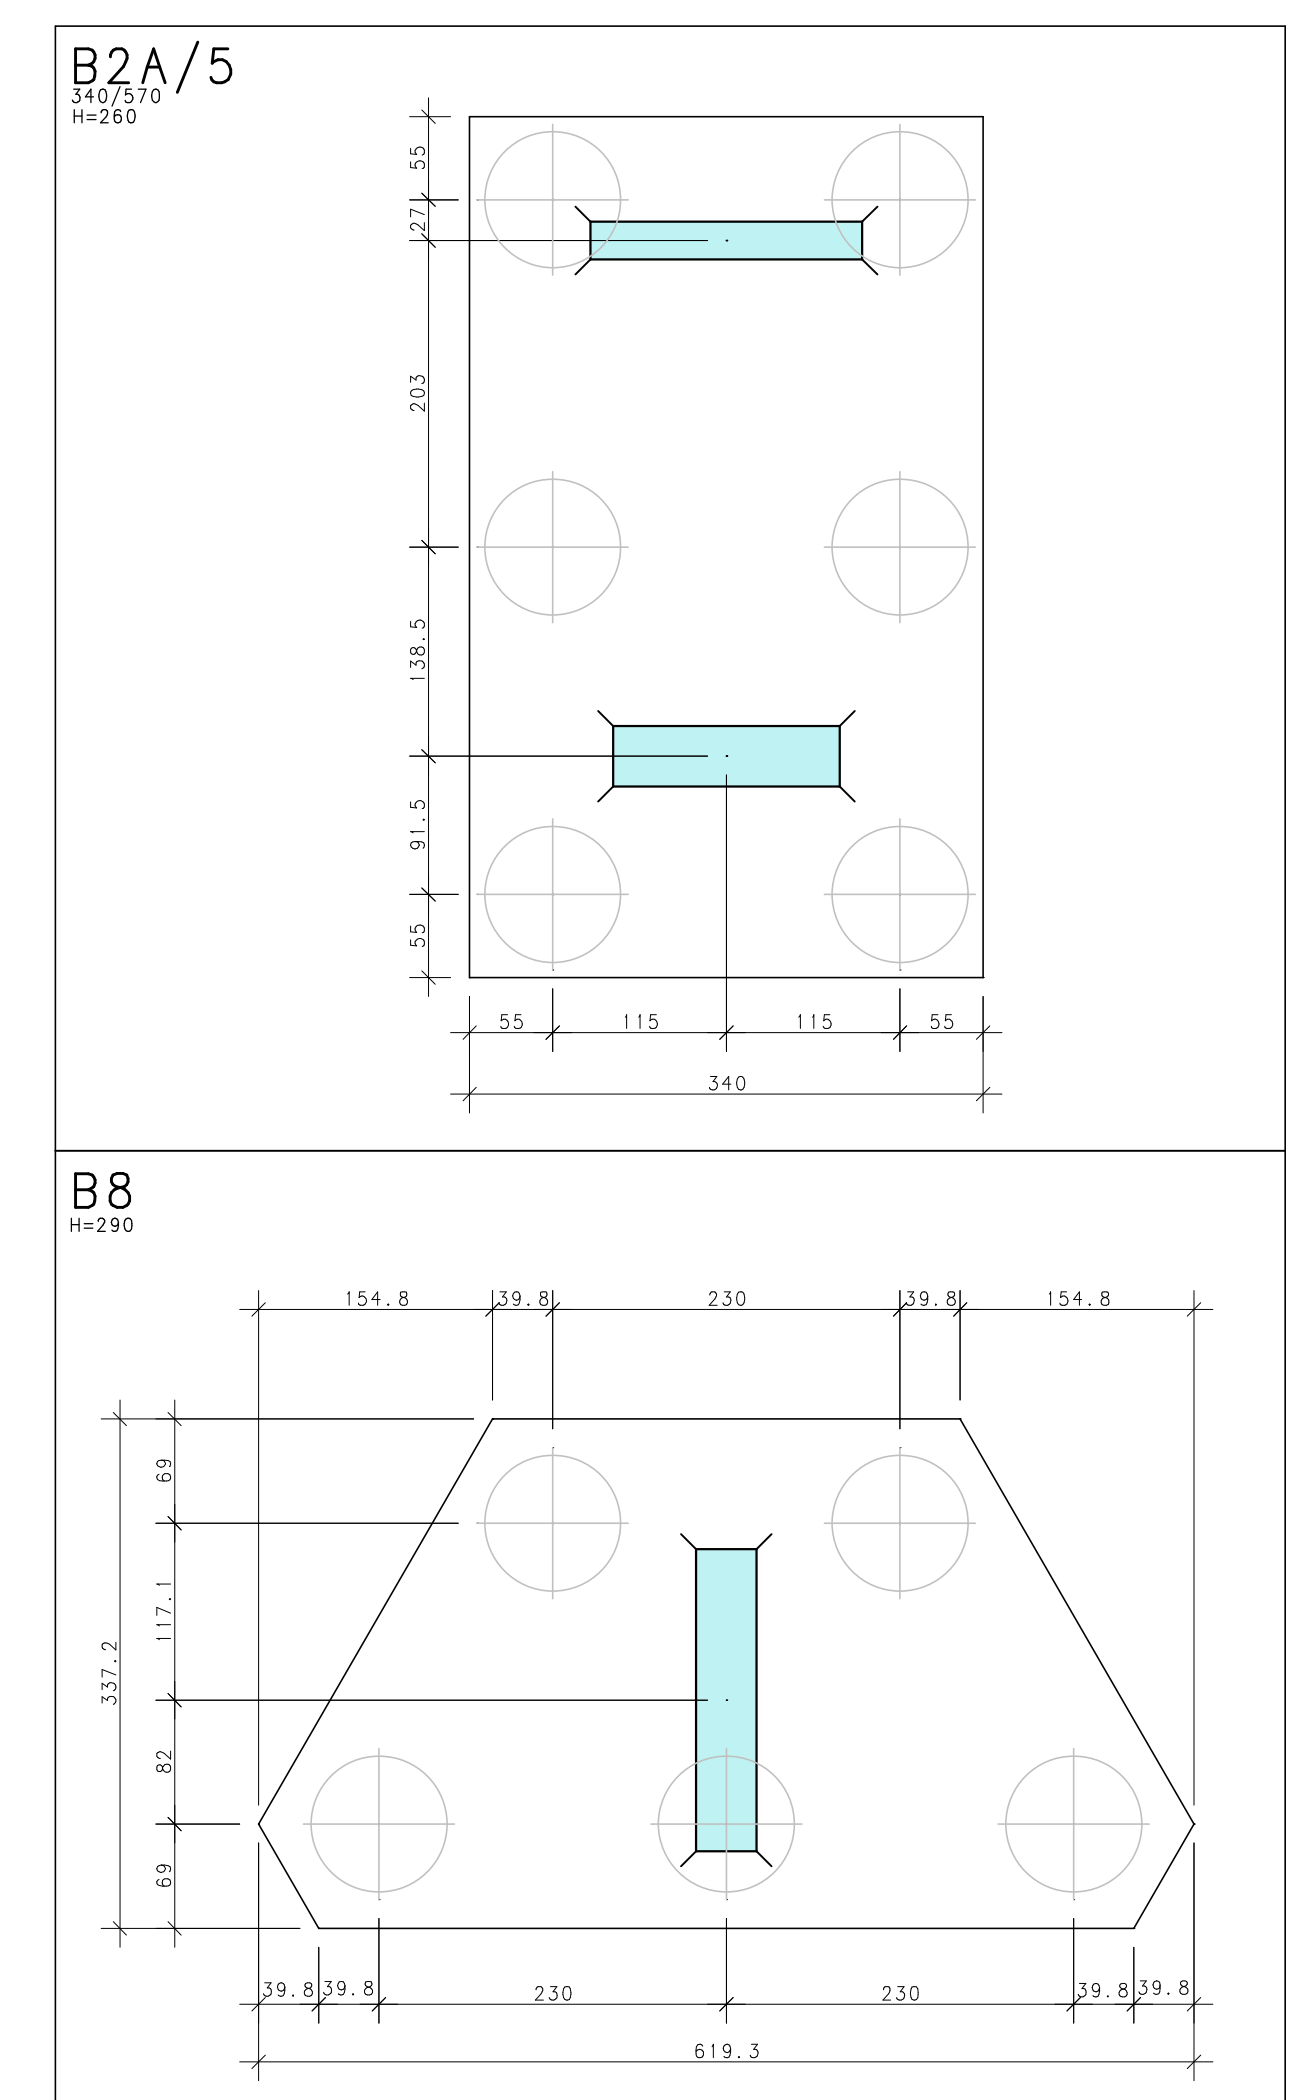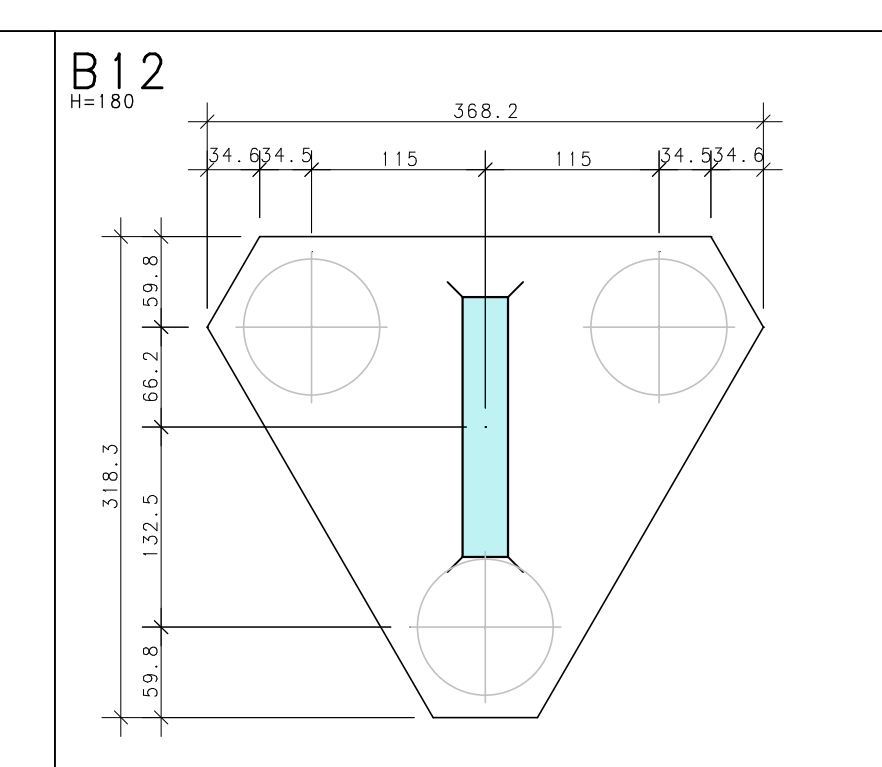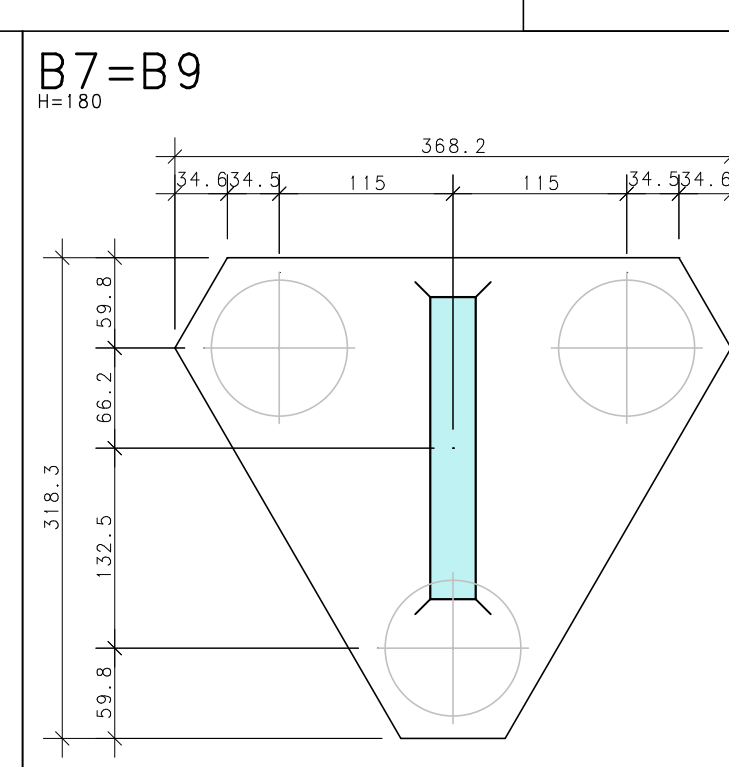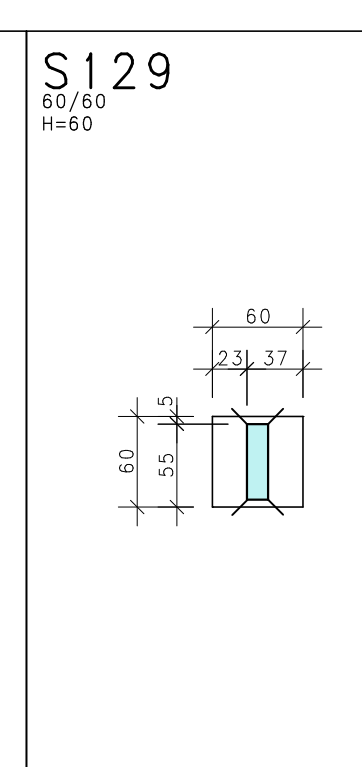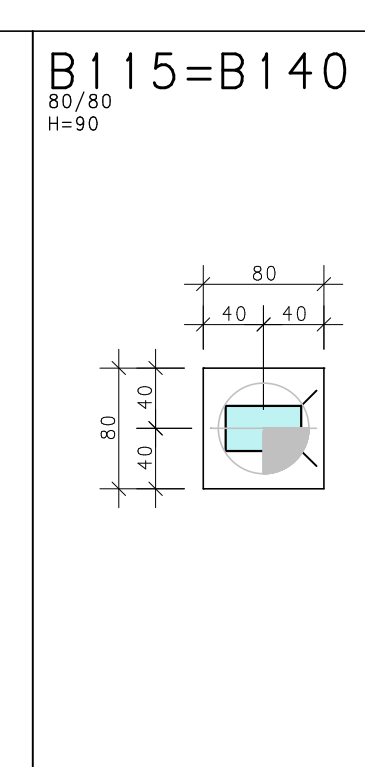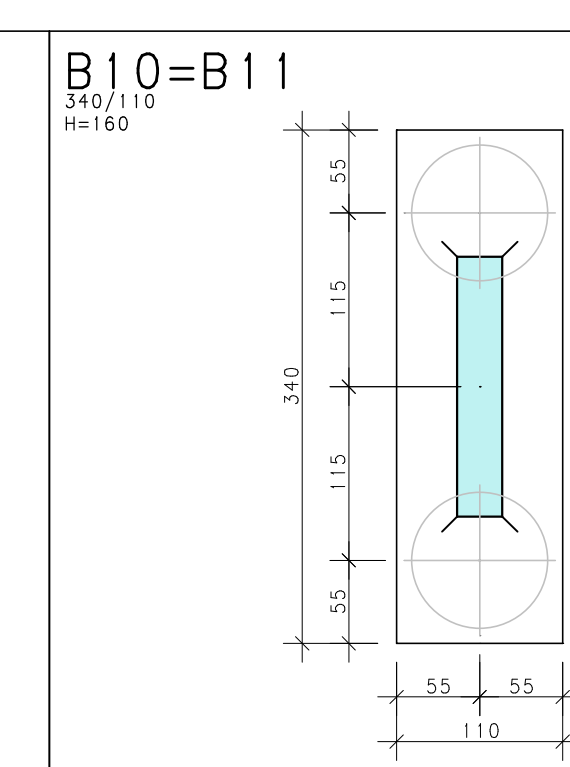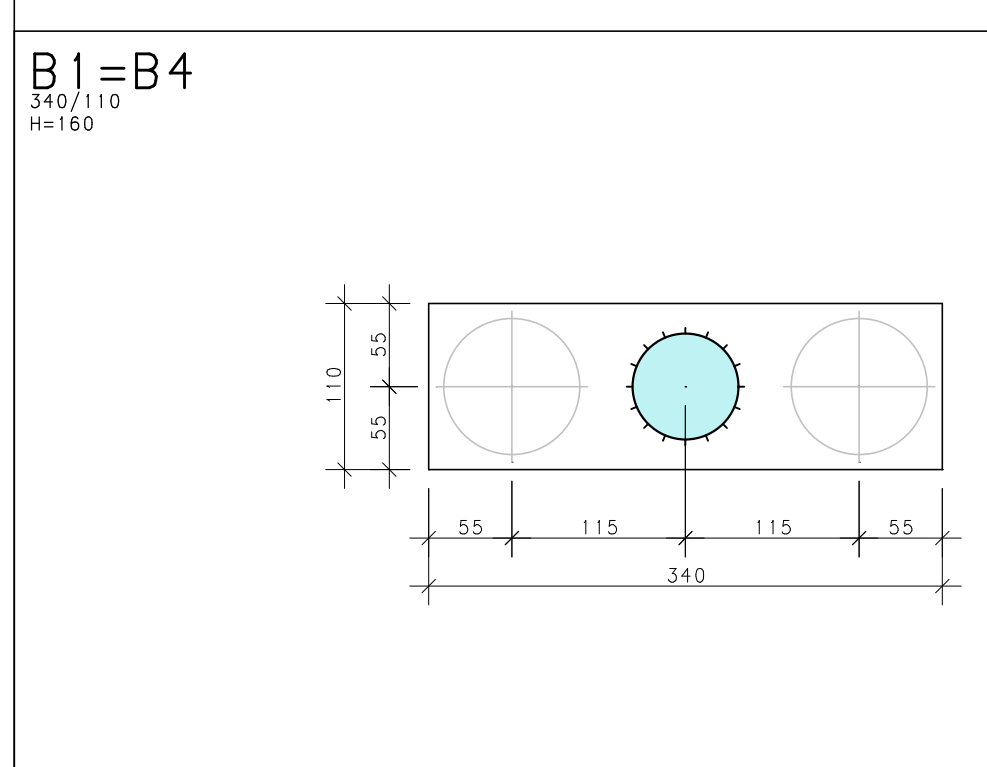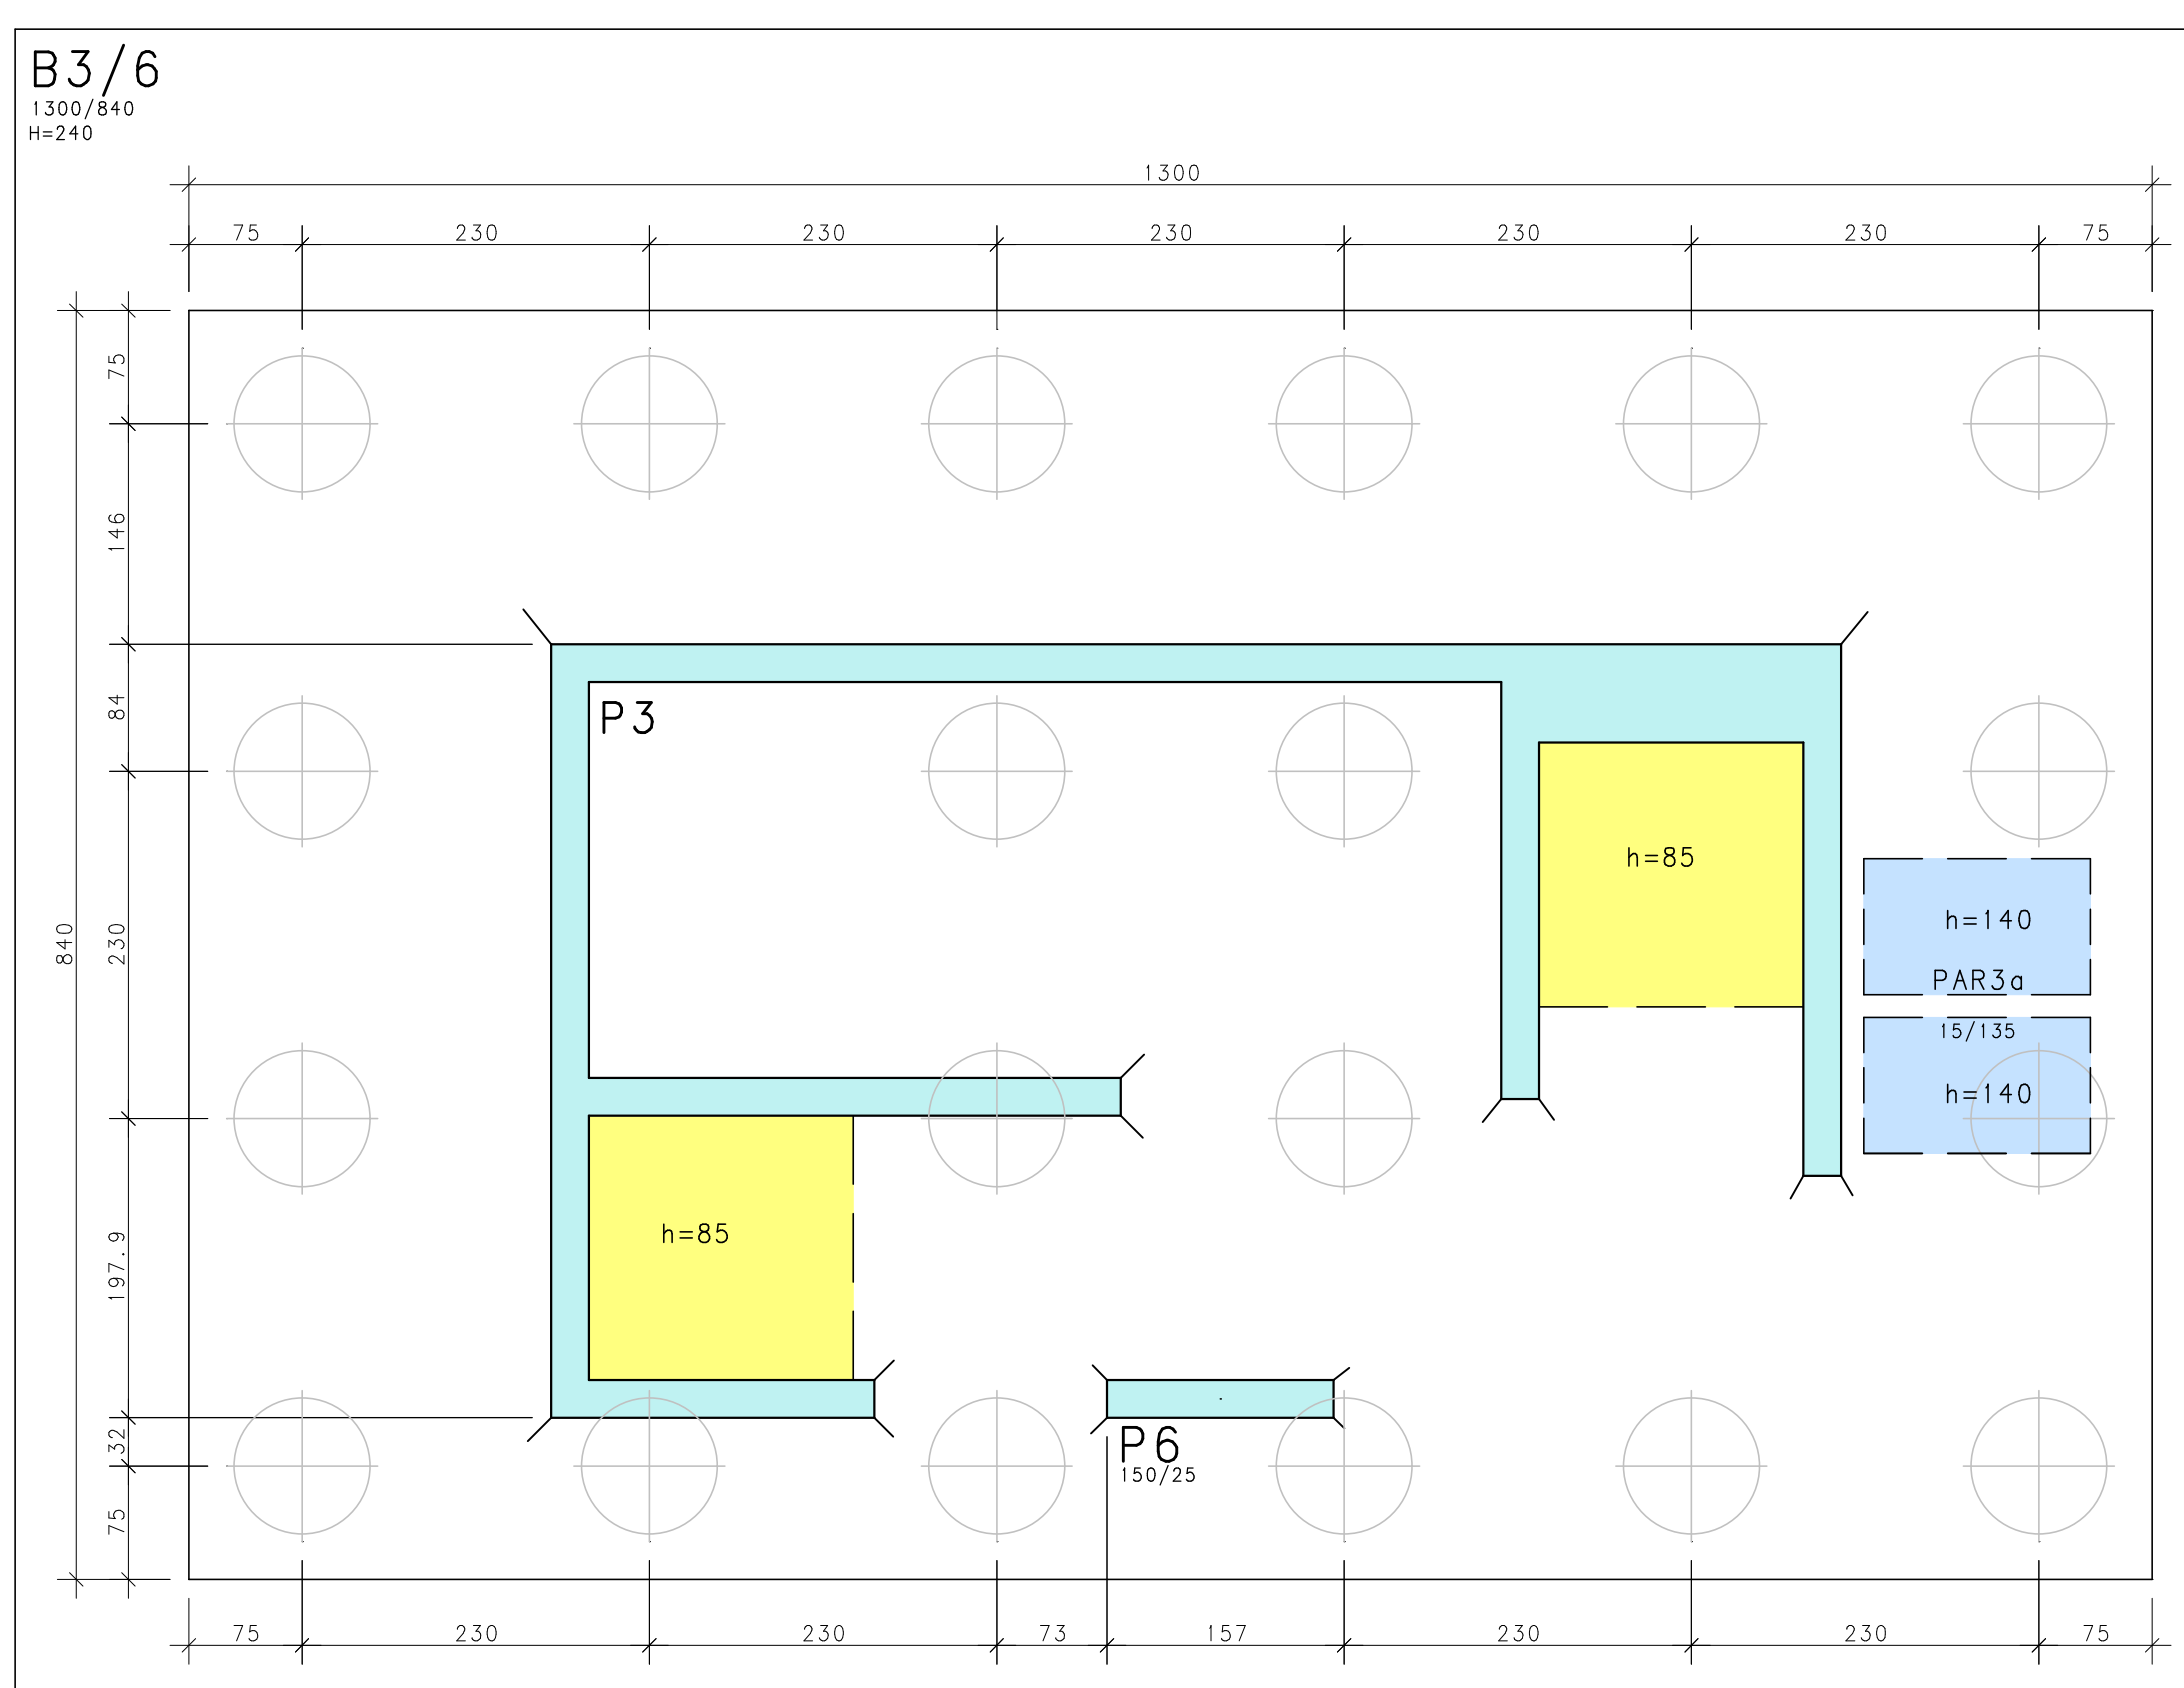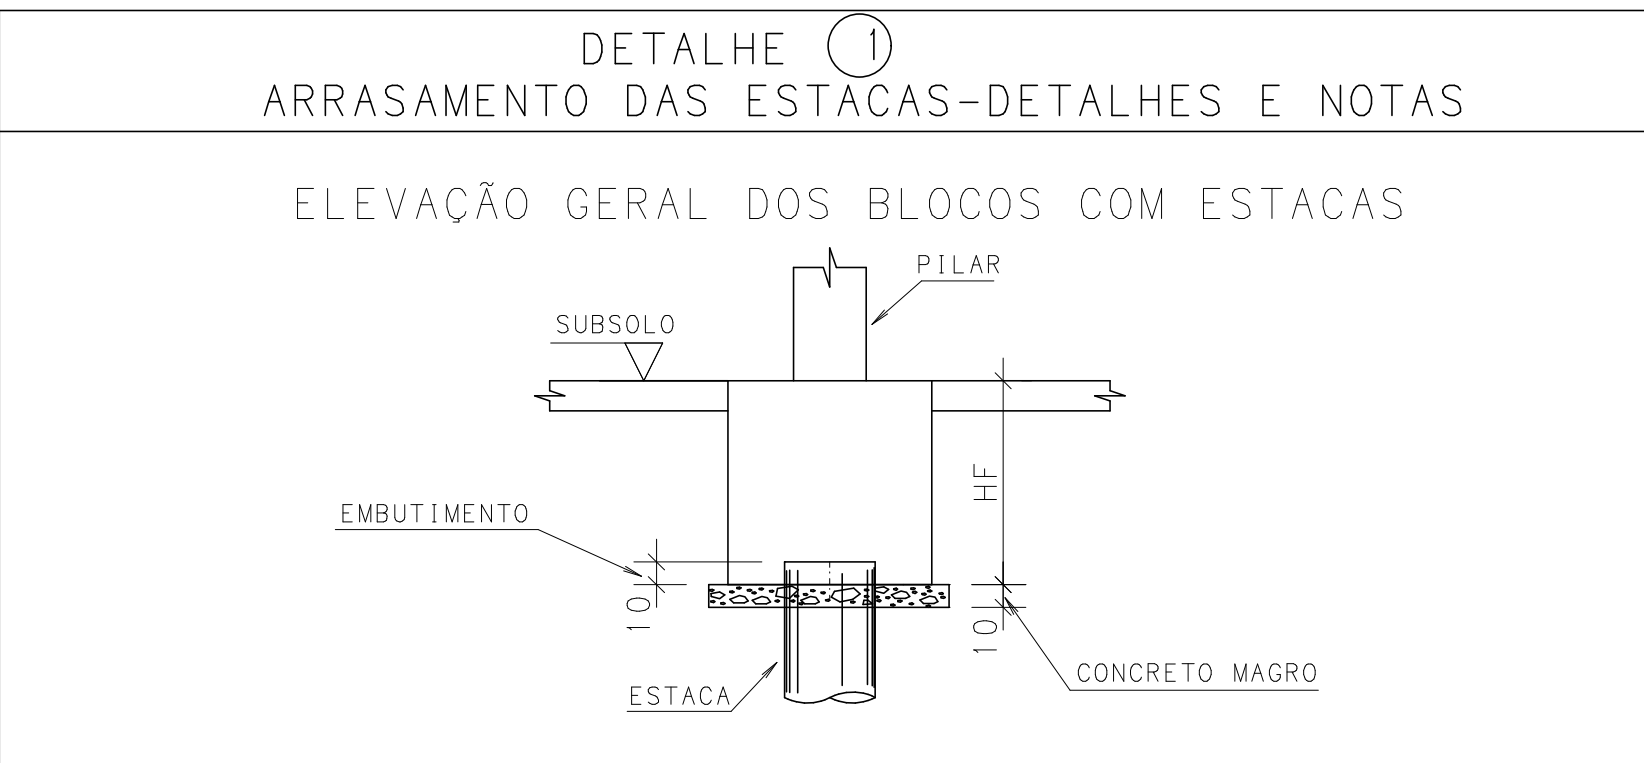

Corte esquemático

TELHADO	27	-77.74
CMS	26	-74.78
DEPMO	25	-71.72
COBERTURA	24	-68.66
1ºPAV	23	-65.60
16ºPAV	22	-62.54
15ºPAV	21	-59.48
14ºPAV	20	-56.42
13ºPAV	19	-53.36
12ºPAV	18	-50.30
11ºPAV	17	-47.24
10ºPAV	16	-44.18
9ºPAV	15	-41.12
8ºPAV	14	-38.06
7ºPAV	13	-35.00
6ºPAV	12	-31.94
5ºPAV	11	-28.88
4ºPAV	10	-25.82
3ºPAV	9	-22.76
2ºPAV	8	-19.70
1ºPAV	7	-16.64
EB5	6	-13.58
EB4	5	-10.52
EB3	4	-7.46
EB2	3	-4.40
EB1	2	-1.34
SUBSÓLO	1	1.72
Fundação	0	4.78