
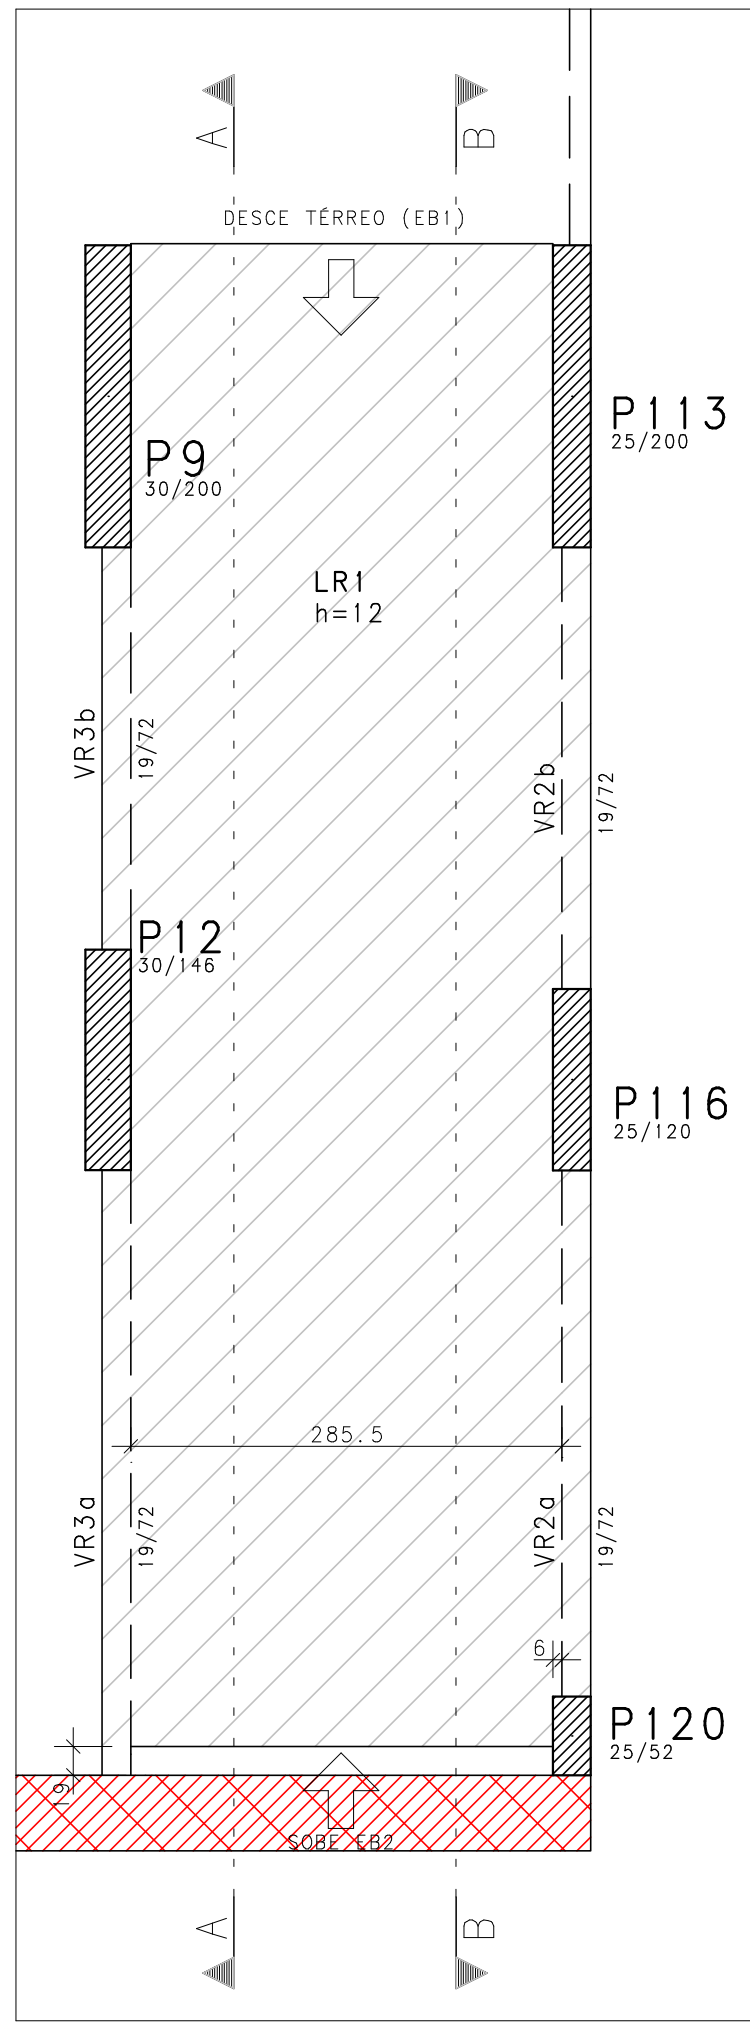
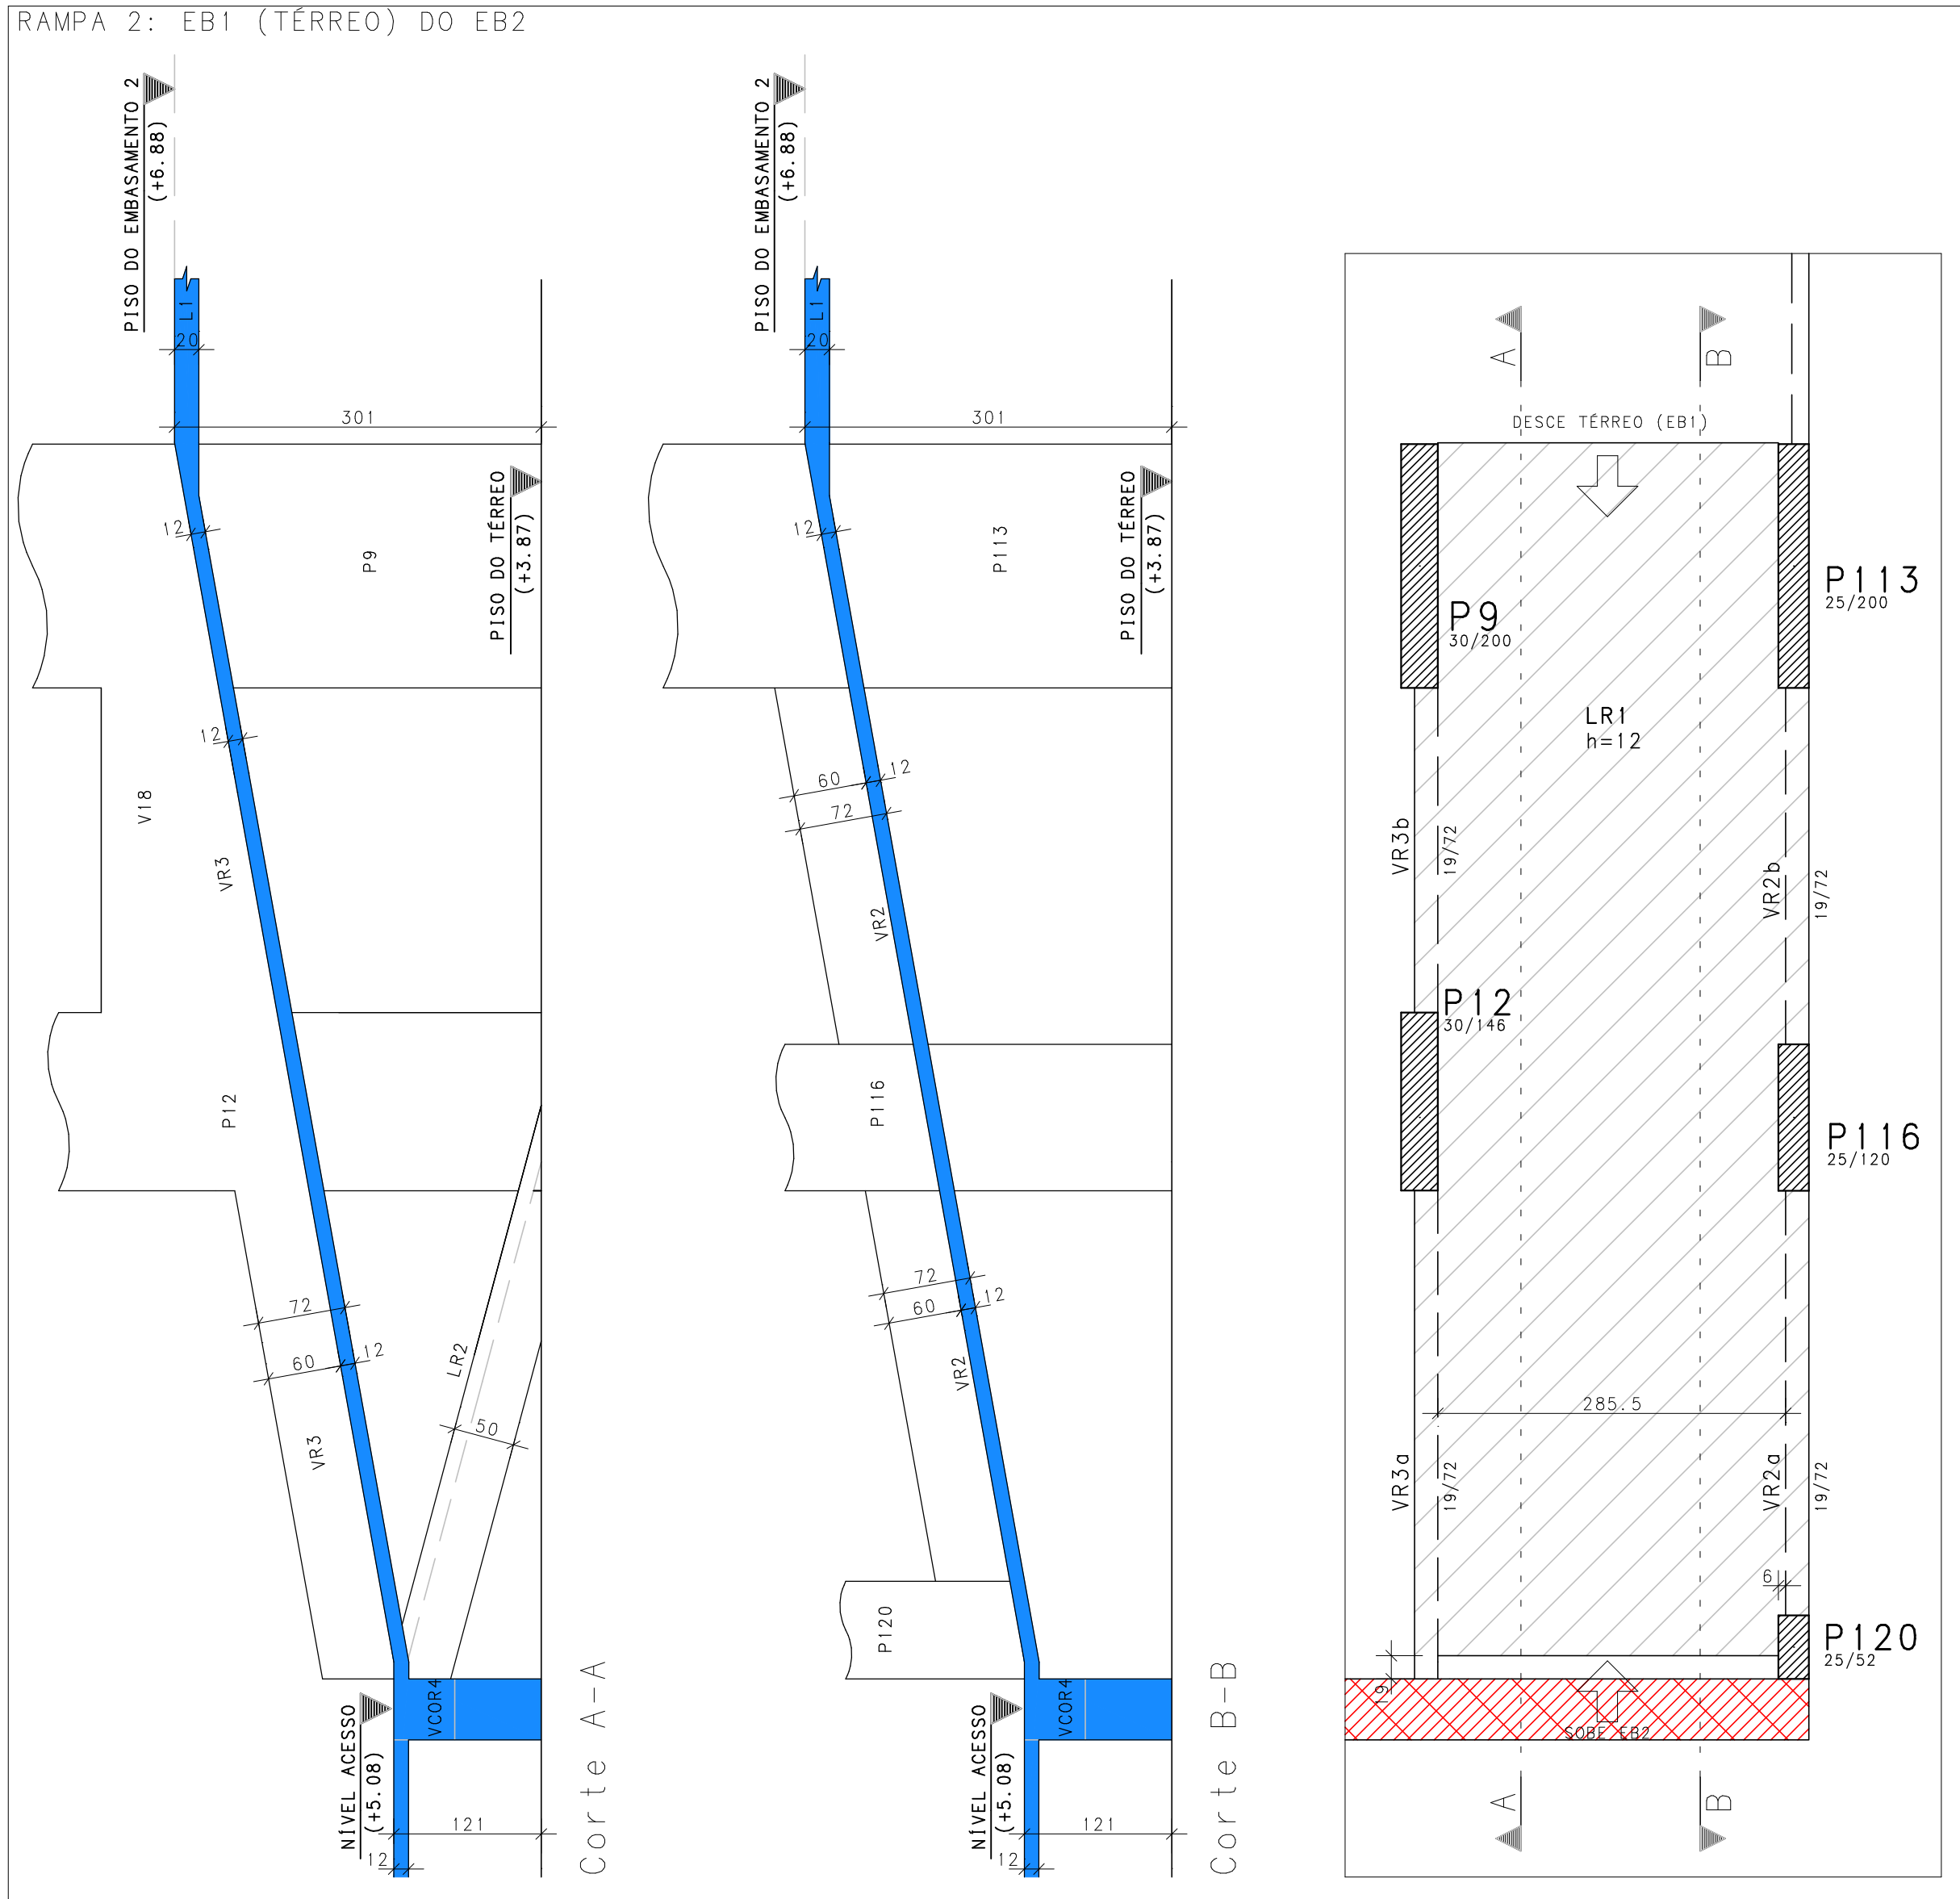
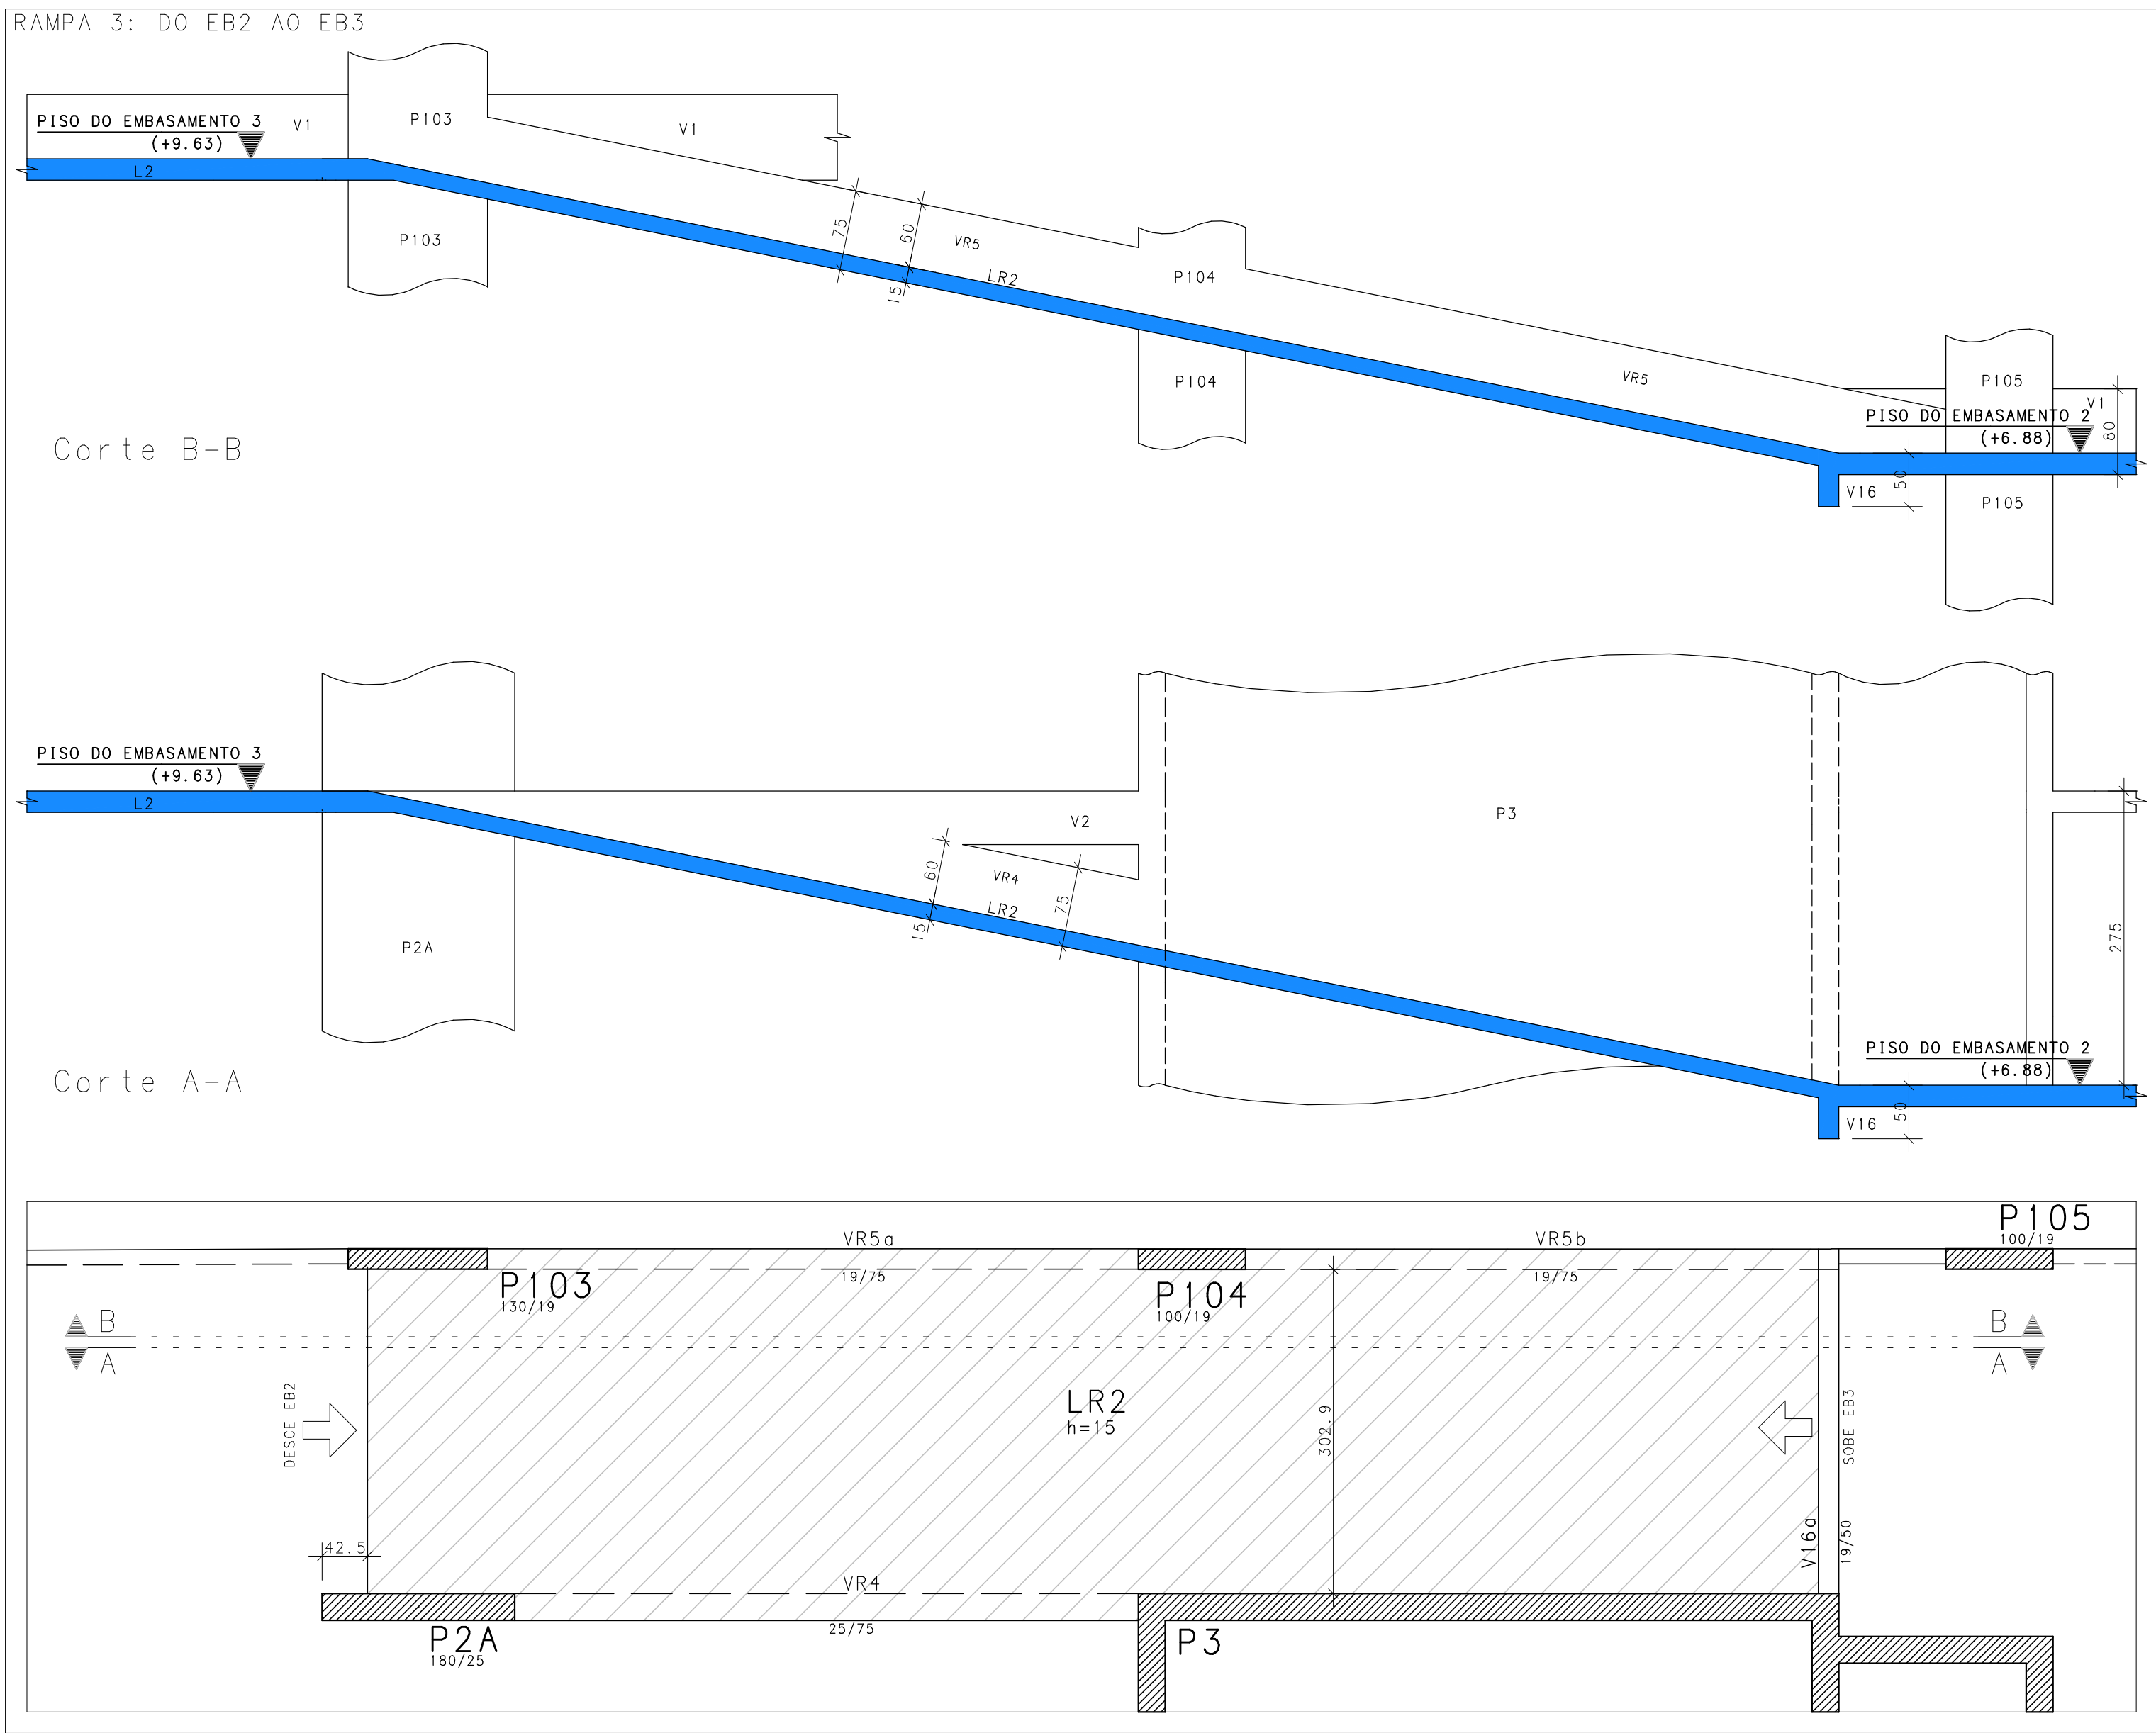


SIGMA 1 - CONSULTORIA & PROJETOS PL PDM-EST-EX-015-PB-RMP-FORM-R00-PLT 22/05/2026 17:23:39

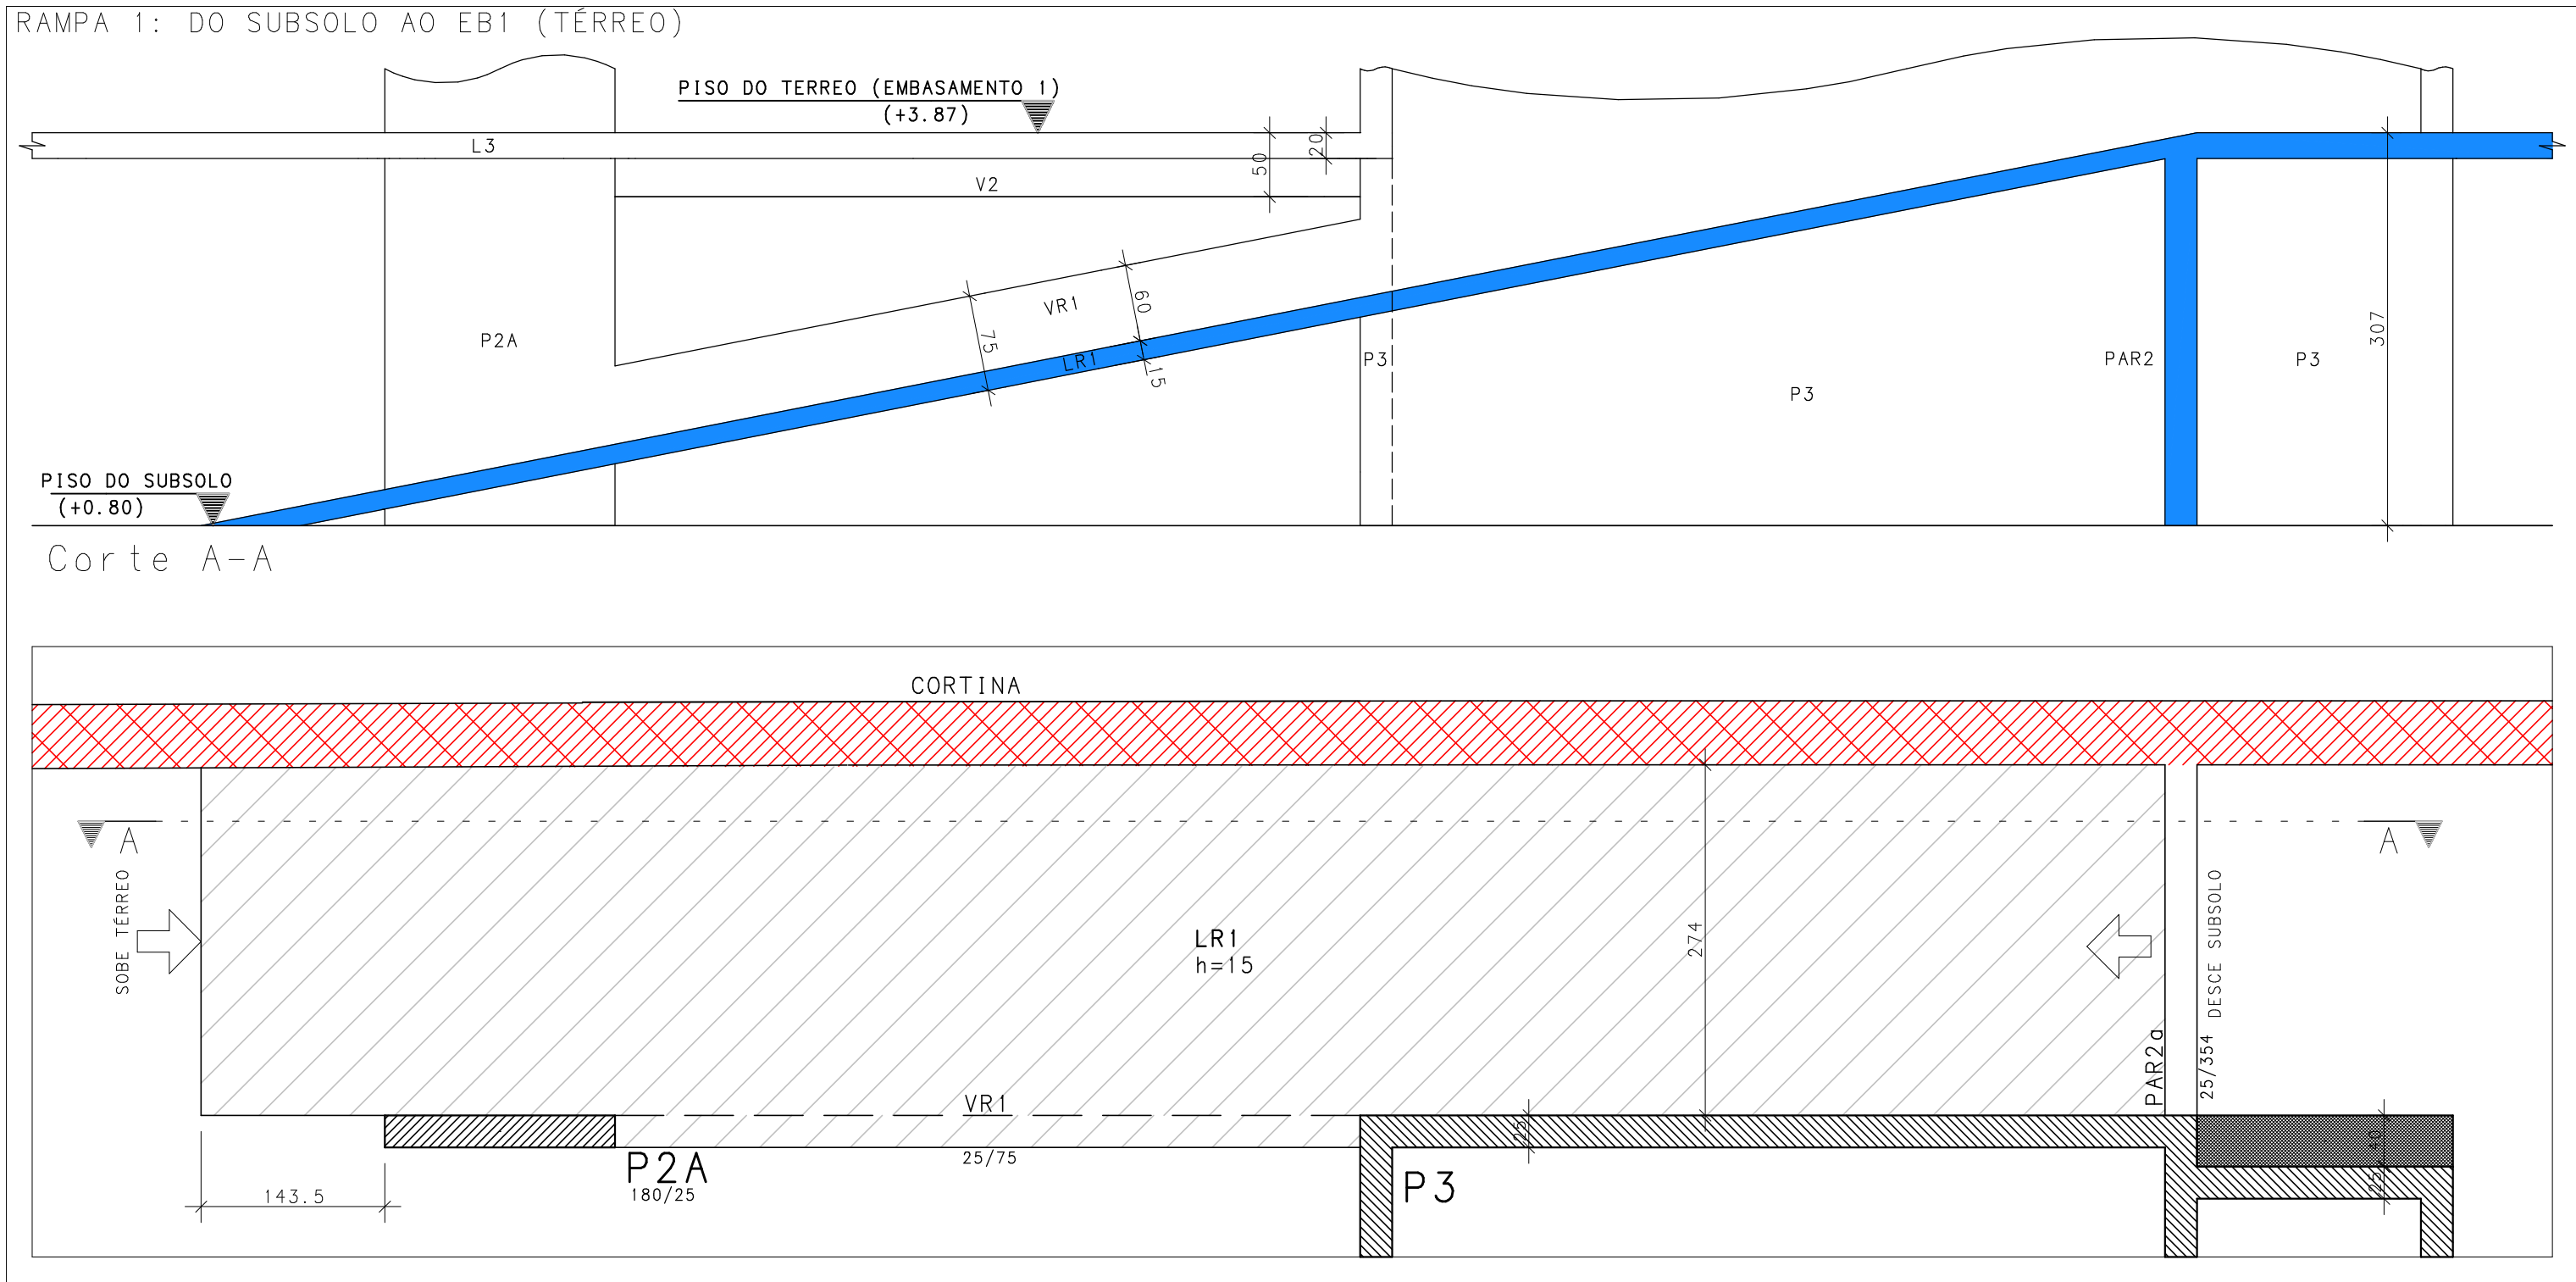

Corte esquemático

TELHADO	27	-	-77.71
CMQ	26	-	-74.28
DEPEN	25	-	-71.72
COBERTURA	24	-	-68.88
17aPAV	23	-	-65.72
18aPAV	22	-	-62.75
19aPAV	21	-	-59.9
14aPAV	20	-	-56.84
13aPAV	19	-	-53.88
12aPAV	18	-	-50.92
11aPAV	17	-	-47.96
10aPAV	16	-	-45.0
9aPAV	15	-	-42.04
8aPAV	14	-	-39.08
7aPAV	13	-	-36.12
6aPAV	12	-	-33.16
5aPAV	11	-	-30.2
4aPAV	10	-	-27.24
3aPAV	9	-	-24.28
2aPAV	8	-	-21.32
1aPAV	7	-	-18.36
EB5	6	-	-15.40
EB4	5	-	-12.44
EB3	4	-	-9.48
EB2	3	-	-6.52
EB1	2	-	-3.56
SUBSOLO	1	-	-0.6
Fundacao	0	-	-7.5

CONVENÇÃO DE PILARES

NASCE	CONTINUA	MORRE
-------	----------	-------

NOTAS GERAIS PARA O USO DESTA PROJETO :

A. DIREITOS AUTORAIS

ESTE PROJETO É PROPRIEDADE DE SIGMA CONSULTORIA & PROJETOS FILIADO A ASSOCIAÇÃO BRASILEIRA DE ENGENHARIA E CONSULTORIA ESTRUTURAL - ABCE, SOB O Nº 0786, NÃO SENDO PERMITIDA SUA UTILIZAÇÃO PARA QUALQUER FINALIDADE QUE NÃO SE RELACIONE COM A EXECUÇÃO ESPECÍFICA DESTA OBRA, SENDO TERMINANTEMENTE VEDADA SUA COLOCAÇÃO À DISPOSIÇÃO DE TERCEIROS.

B. NORMAS TÉCNICAS DE REFERÊNCIA

NBR 6118 PROJETO DE ESTRUTURAS DE CONCRETO

NBR 6120 CARGAS PARA O CÁLCULO DE ESTRUTURAS DE EDIFICAÇÕES

NBR 6123 FORÇAS DEVIDAS AO VENTO EM EDIFICAÇÕES

NBR 5671 PARTICIPAÇÃO DOS INTERVENIENTES EM SERVIÇOS E OBRAS DE ENGENHARIA E ARQUITETURA

NBR 12654 CONTROLE TECNOLÓGICO DE MATERIAIS COMPONENTES DO CONCRETO

NBR 12655 CONCRETO - PREPARO, CONTROLE E RECEBIMENTO

NBR 5738 MOLDEAMENTO E CURA DE CORPOS CILÍNDRICOS OU PRISMA MÁTICOS DE CONCRETO - MÉTODO DE ENSAIO

NBR 5739 CONCRETO - ENSAIO DE COMPRESSÃO DE CORPOS-DE-PROVA CILÍNDRICOS - MÉTODO DE ENSAIO

NBR 8522 CONCRETO - DETERMINAÇÃO DO MÓDULO DE DEFORMAÇÃO ELÁSTICA E DIAGRAMA TENSÃO x DEFORMAÇÃO - MÉTODO DE ENSAIO

NBR 6152 MATERIAIS METÁLICOS-DETERMINAÇÃO DAS PROPRIEDADES MECÂNICAS A TRAÇÃO-MÉTODO DE ENSAIO

NBR 6153 PRODUTO METÁLICO - ENSAIO DE DOBRAMENTO SEMI-GUIADO

NBR 7477 DETERMINAÇÃO DO COEFICIENTE DE CONFORMAÇÃO SUPERFICIAL DE BARRAS E FIOS DE AÇO DESTINADOS A ARMADURA DE CONCRETO ARMADO MÉTODO DE ENSAIO

NBR 7480 BARRAS E FIOS DE AÇO DESTINADOS A ARMADURAS PARA CONCRETO ARMADO - ESPECIFICAÇÃO

C. GEOMETRIA

OS ELEMENTOS DE CONFORMAÇÃO DO PROJETO ESTRUTURAL FAÇA AOS PROJETOS DE ARQUITETURA, INSTALAÇÕES E DEMAIS DISCIPLINAS.TAIS COMO COTAS, NÍVEIS, DIMENSÕES DAS PEÇAS ESTRUTURAIS, POÇOS DE ELEVADORES, ESCADAS, ETC. DEVEM SER VALIDADOS PELOS ARQUITETOS RESPONSÁVEIS PELO DESENVOLVIMENTO DO PROJETO EXECUTIVO.

D. MATERIAIS

01. CONCRETO

VER EM NOTAS GERAIS

02. AÇO EM ARMADURA PASSIVA

02.1. AÇO CA-50A / CA-60B

03. FORMAS E ESCORAMENTOS

O PROJETO E DIMENSIONAMENTO DAS FORMAS E ESCORAMENTOS NÃO FAZ PARTE DO ESCOPO DE NOSSOS SERVIÇOS.

E. EXECUÇÃO DA ESTRUTURA

A EXECUÇÃO DA ESTRUTURA E DE RESPONSABILIDADE DA EMPRESA CONSTRUTORA E DEVERÁ CONTAR COM A CONSULTORIA DE UM TECNOLÓGICO DE MATERIAIS, O ENGENHEIRO RESPONSÁVEL PELA EXECUÇÃO DEVERÁ OBEDECER AS RECOMENDAÇÕES DA NBR-14931-EXECUÇÃO DE ESTRUTURAS DE CONCRETO-PROCESSOS.

F. CARGAS ADOPTADAS PARA ESTE PROJETO

01. FORÇAS DEVIDO AO VENTO : CONFORME NBR 6123

02. CARGAS ACIDENTAIS NÃO PARTICULARES : CONFORME NBR 6120 DE ACORDO COM PROJETO ARQUITETÔNICO APROVADO EM PREFEITURA

03. PESO PRÓPRIO DO CONCRETO : 2500 kgf / m³

04. ALVENARIAS (COM REVESTIMENTOS) : 1500 kgf / m³

+ ESPESURA DA ALVENARIA ACABADA CONFORME PROJ. ARQUITETÔNICO

05. LAJES (CONTRAPISO / REVESTIMENTOS) : 100 kgf / m²

06. AS CARGAS EVENTUALMENTE INFORMADAS NAS PRANCHAS DE FORMAS PREVALECEM SOBRE AS CARGAS AQUI INDICADAS.

G. COBERTIMENTOS

COBERTOS	PAV. REVESTIDOS	DEMAIS PAV.
01. LAJES: POSITIVA/NEGATIVA	2.0/1.5 cm	2.0/2.0 cm
02. VIGAS:	2.5 cm	2.5 cm
03. PILARES:	3.0 cm	3.0 cm
04. BLOCOS SOBRE ESTACAS / SAPATAS:	3.0 cm	
05. CINTAS / LAJES DE SUPRESSÃO:	3.0 cm	
06. PAREDES DE SUBSOLO:	5.0 cm	
07. RESERVATÓRIOS:	5.0 cm	

08. 1) DEVERÁ HAVER CONTROLE RIGOROSO DE QUALIDADE E RÍGIDOS LIMITES DE TOLERÂNCIA DAS MEDIDAS DURANTE A EXECUÇÃO.

2) COBERTIMENTOS INFORMADOS NOS DESENHOS DE ARMADURA PREVALECEM EM RELAÇÃO À TABELA ACIMA.

H. MEMORIAL DESCRITIVO PARA DESCIMBRAMENTO DA ESTRUTURA

(PAR DESENVOLVIMENTO DA RESISTÊNCIA DO CONCRETO ATENDENDO AS EXPECTATIVAS DE VALORES A 7, 14, 21 E 28 DIAS)

TEMPO DECORRIDO APÓS A CONCRETAGEM (DIAS)

TEMPO DECORRIDO APÓS A CONCRETAGEM (DIAS)	% ESCORAMENTO A SER MANTIDO
0	>100%
7	100%
14	50%
21	25%
28	SEM ESCORAMENTO

I. FUNDAÇÕES

01. O PROJETO DE FUNDAÇÕES, DETERMINAÇÃO DA TAXA ADMISSÍVEL NO TERRENO, DISPOSIÇÃO E DIMENSIONAMENTO DE ESTACAS, COTA DE IMPLANTAÇÃO, METODOLOGIA DE ESCAVAÇÃO, INTERAÇÃO COM VIZINHOS, ETC., É DE RESPONSABILIDADE DA EMPRESA DE CONSULTORIA DE FUNDAÇÕES DEVENDO SEGUIR AS RECOMENDAÇÕES DA NBR-6122 - PROJETO E EXECUÇÃO DE FUNDAÇÕES

J. FURAÇÕES

01. FUROS EM LAJES E VIGAS DEVERÃO RECEBER ARMADURA DE REFORÇO PADRÃO.

02. FUROS NÃO INDICADOS SÓ PODERÃO SER EXECUTADOS COM NOSSA APROVAÇÃO.

NOTAS GERAIS

1- DIMENSÕES EM CENTÍMETRO. NÍVEIS EM METRO

2- PROPRIEDADES DO CONCRETO:

- $f_{ck} > 40 \text{ MPa}$ (400 kg/cm²)

- MÓDULO DE DEFORMAÇÃO TANGENTE INICIAL $> 32 \text{ GPa}$

- CONSUMO MÍNIMO DE CIMENTO: 350 kg/m³

- FATOR ÁGUA/CIMENTO MÁXIMO: 0,55

3- UTILIZAR OBRIGATORIAMENTE EM CONJUNTO COM O DESENHO DE FURAÇÃO

ATENÇÃO/PLOTAGEM

- OS ARQUIVOS DXF SERVEM APENAS COMO BASE PARA A ARQUITETURA E DEMAIS COMPLEMENTARES.

- PLOTAR APENAS O ARQUIVO PDF-COLORIDO CASO CONTRÁRIO PODERÁ HAVER PERDA DE INFORMAÇÕES

05		
04		
03		
02		
01		
00	22/05/2026	EMIÇÃO INICIAL
REV.	DATA	DESCRIÇÃO
SIGMA CONSULTORIA & PROJETOS SIGMA CONSULTORIA & PROJETOS RUA URUGUAIANA, 10-SALA 2307- CENTRO- RIO DE JANEIRO-RJ TEL/FAX: (55-21)2508-8541 E-MAIL: admin@sigmaconsultoria.com.br www.sigma-eng.br ENG. EDUARDO VIDAL GABRAL CREA: 18837/O ENG. MAURÍCIO DOS SANTOS SGARBI CREA: 20051/0508		
NÚMERO DA OBRA 578		
RESPONSÁVEL MAURÍCIO SGARBI		
COORDENADOR VINÍCIUS CORDEIRO		
PROJETISTA VINÍCIUS C.		
DESENHO Nº ST 015		
EMPRESAMENTO E LOCAL PDM 1050 RUA PRUDENTE DE MORAIS, 1050 - IPANEMA, RIO DE JANEIRO - RJ		
TÍTULO DO DESENHO FORMA DAS RAMPAS		
PROJETO ESTRUTURA		
FASE EXECUTIVO		
ESCALA 1:50		
DATA 22/05/2026		
ARQUIVO PDM-EST-EX-015-PB-RMP-FORM-R00		