



PROJETO DE DEMOLIÇÃO

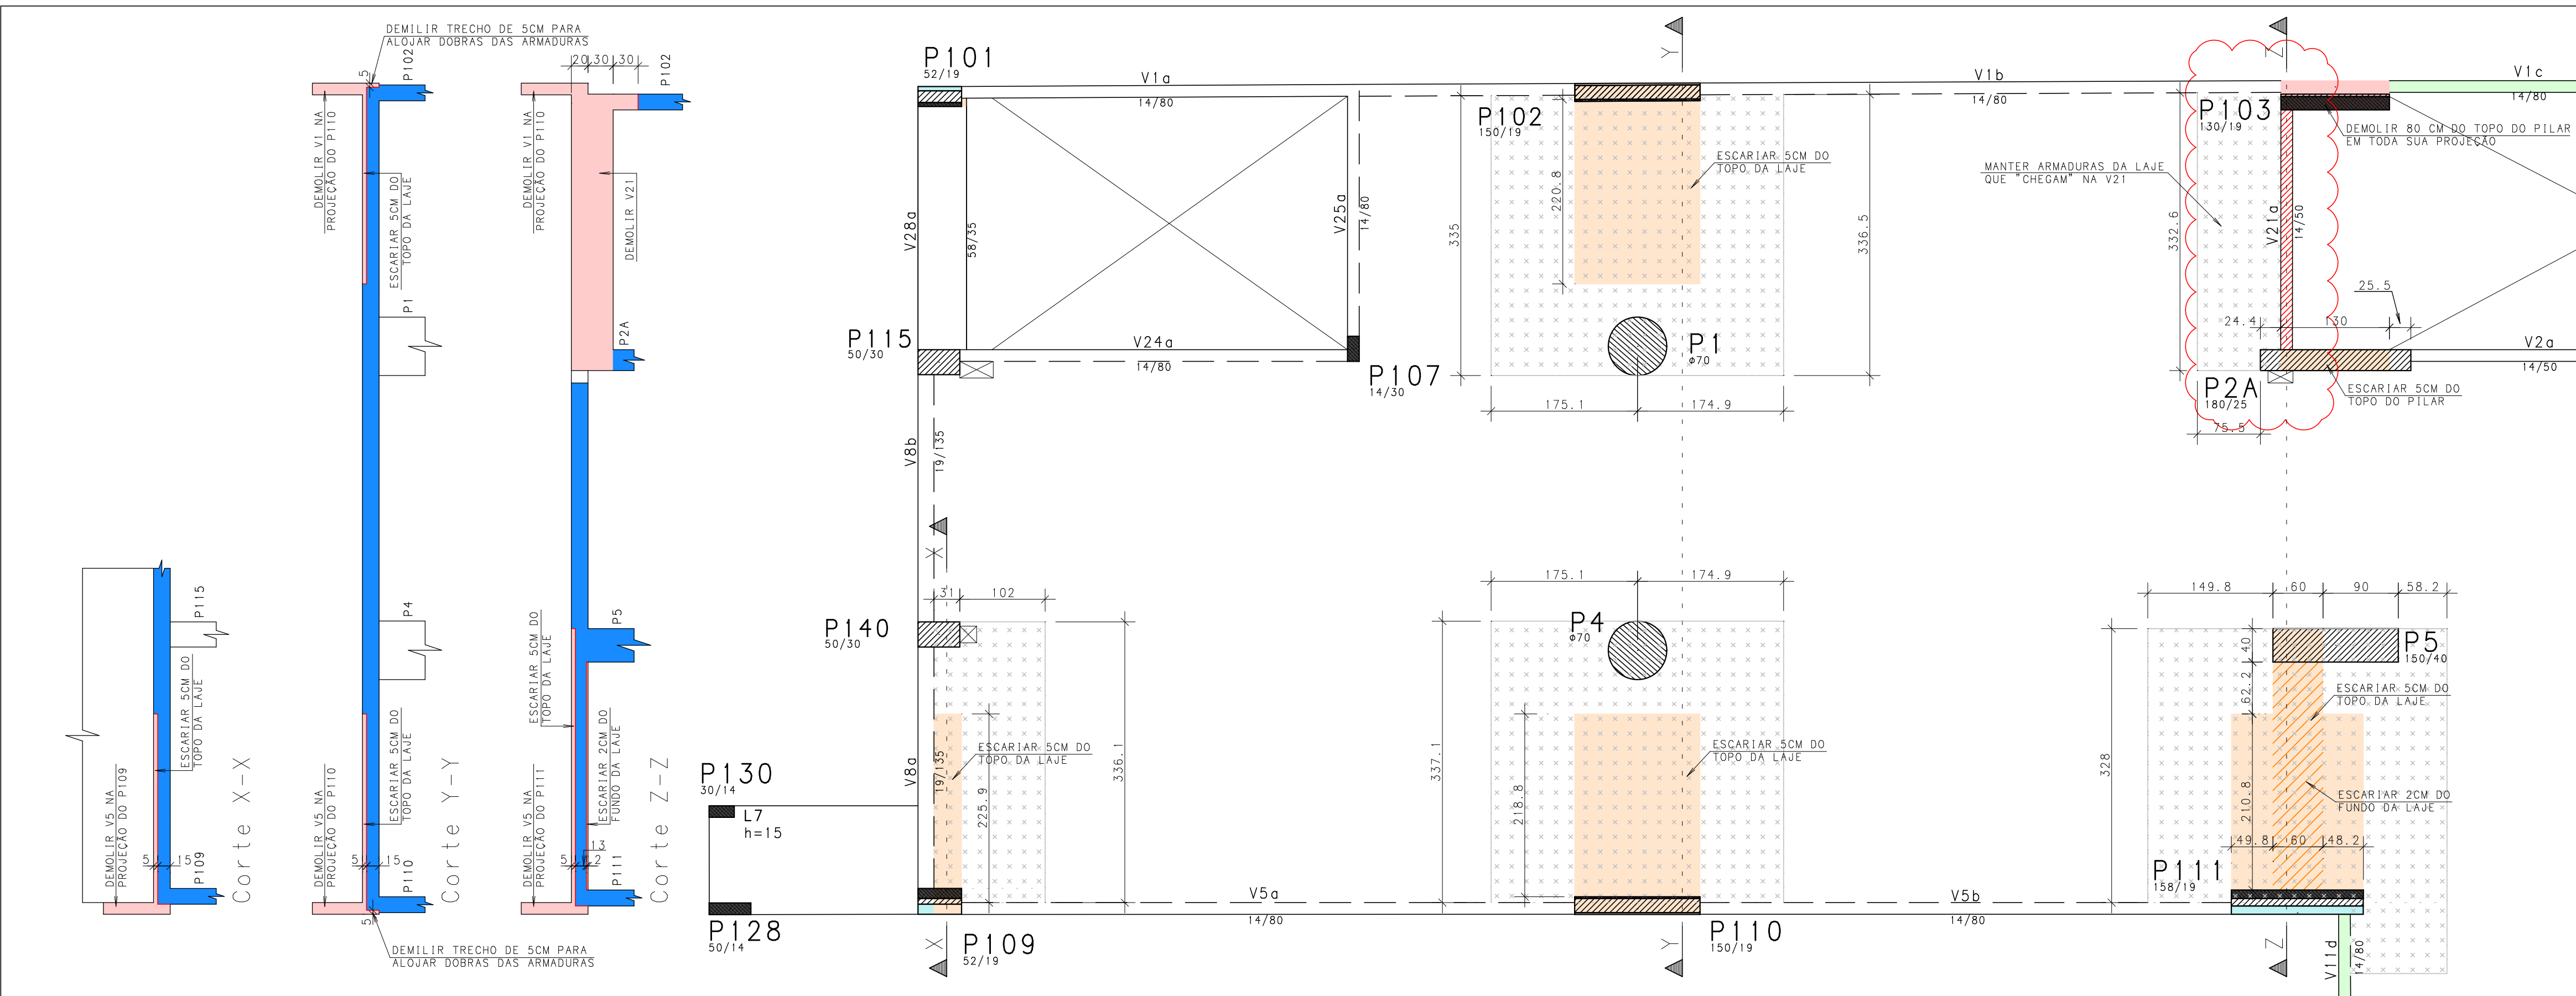

PROJETO DE RECONSTRUÇÃO

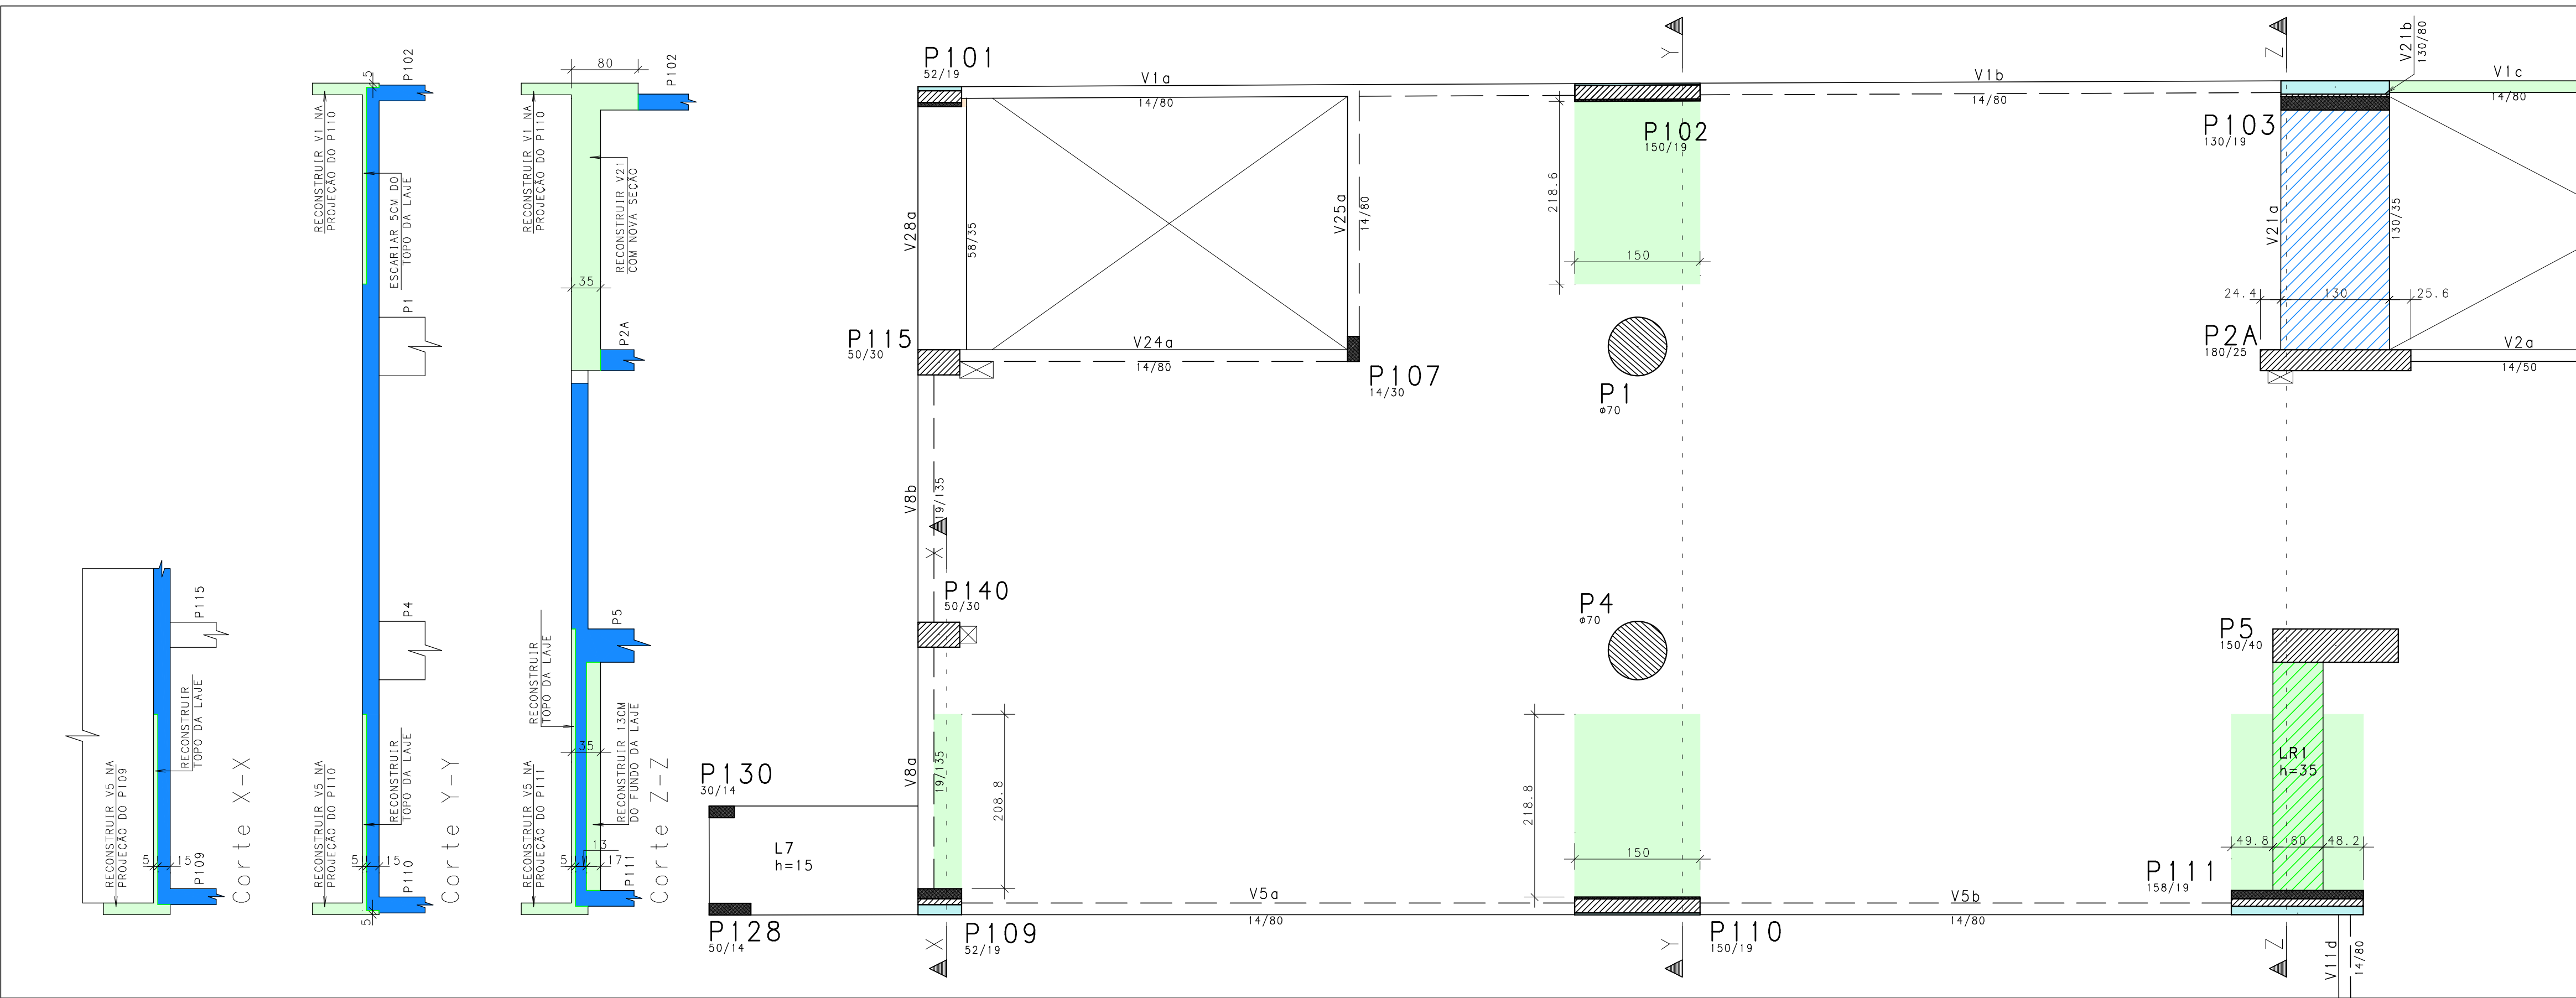

PAV. EB2 - ARMAÇÃO SUPERIOR DE REFORÇO

